


CANOPY ROOF SHEETING PLAN (TYP

CANOPY ROOF FRAMING PLAN (TYP

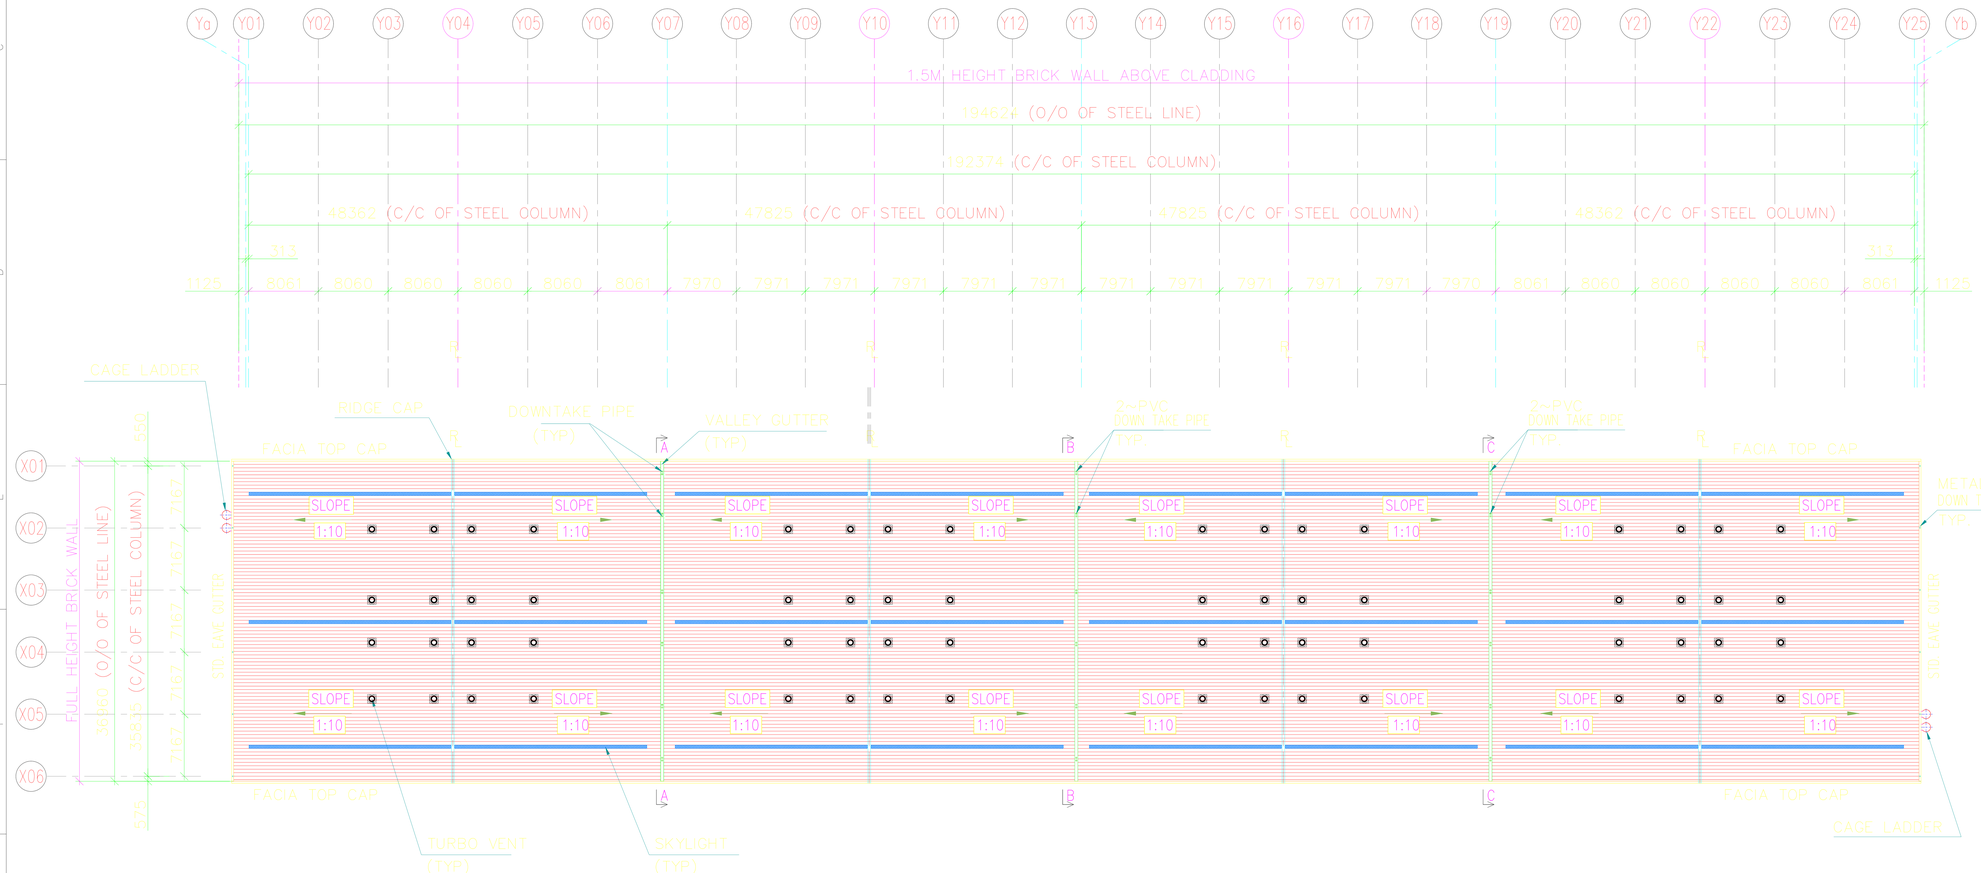

ROOF SHEETING PLAN

FOR PRIMARY AND SECONDARY TYPICAL CONNECTION DETAILS REFER SHEET GA-014/015/016/017
FOR TYPICAL PORTAL BRACING ELEVATION DETAILS REFER SHEET GA-009
FOR SKYLIGHT DETAILS REFER SHEET GA-014
RIGDE CAP DETAIL [REFER GA-14]

GOOD FOR RECORDS

ISSUED FOR APPROVAL

SENT ON .....

IN ORDER TO SCHEDULE THIS PROJECT IN THE MOST EFFICIENT MANNER, RETURN THESE DOCUMENTS, MARKED WITH YOUR COMMENTS, WITHIN TWO WEEKS FROM THE ABOVE MENTIONED DATE. ANY CHANGES MADE AFTER APPROVAL OF THESE DRAWINGS MAY DELAY THE FABRICATION AND DELIVERY PROCESS.

THESE DRAWINGS ARE NOT FOR CONSTRUCTION.

1. ☐ APPROVED
NO CHANGES, PROCEED WITH FABRICATION.
2. ☐ APPROVED AS NOTED
FABRICATION MAY PROCEED ON THE BASIS OF CORRECTIONS INDICATED.
3. ☐ NOT APPROVED, RE-SUBMIT FOR APPROVAL.

REVIEWED BY .....
NAME
.....
SIGNATURE ..... DATE

Rev.	Description	Name	Checked	Date
R2	GOOD FOR RECORDS	P.B./B.R.	A.A./M.S.	26/09/2023
R1	REVISED AS PER CLINT COMMENT	P.B./B.R.	A.A./M.S.	18/09/2023
R0	ISSUED FOR APPROVAL	P.B.	A.A./M.S.	30/03/2023

REVISIONS

Project: Pre Engineering Building At GMR-DELHI INTERNATIONAL AIRPORT LTD. NEW DELHI

Client: GMR-DELHI INTERNATIONAL AIRPORT LTD. NEW DELHI

Process Consultant:

Detailed Engineering Consultant:

Building: GA PARKING

Drawing Title: ROOF SHEETING PLAN

everest
Everest Industries Limited
ESBS Division, Level 3, Tower 14, Solitaire Corporate Park, Chakala, Andheri (E), Mumbai-400093, India.
Website : www.everestind.com

Drawn by:	P.B.	Scale:	1:500	Date:	30/03/2023
Checked by:	A.A./M.S.	Project No:	ESBS/PB-02434:01.01.01	Drawing No:	GA-001
Design By	A.A.			Revision:	R2

NOTE:-
1. All rights reserved. This drawing contains proprietary information which is protected by copyright. No part of this drawing may be reproduced, translated in computer language, or transmitted in any form whatsoever without the prior written consent of EVEREST INDUSTRIES LIMITED.

SHEET SIZE-A3