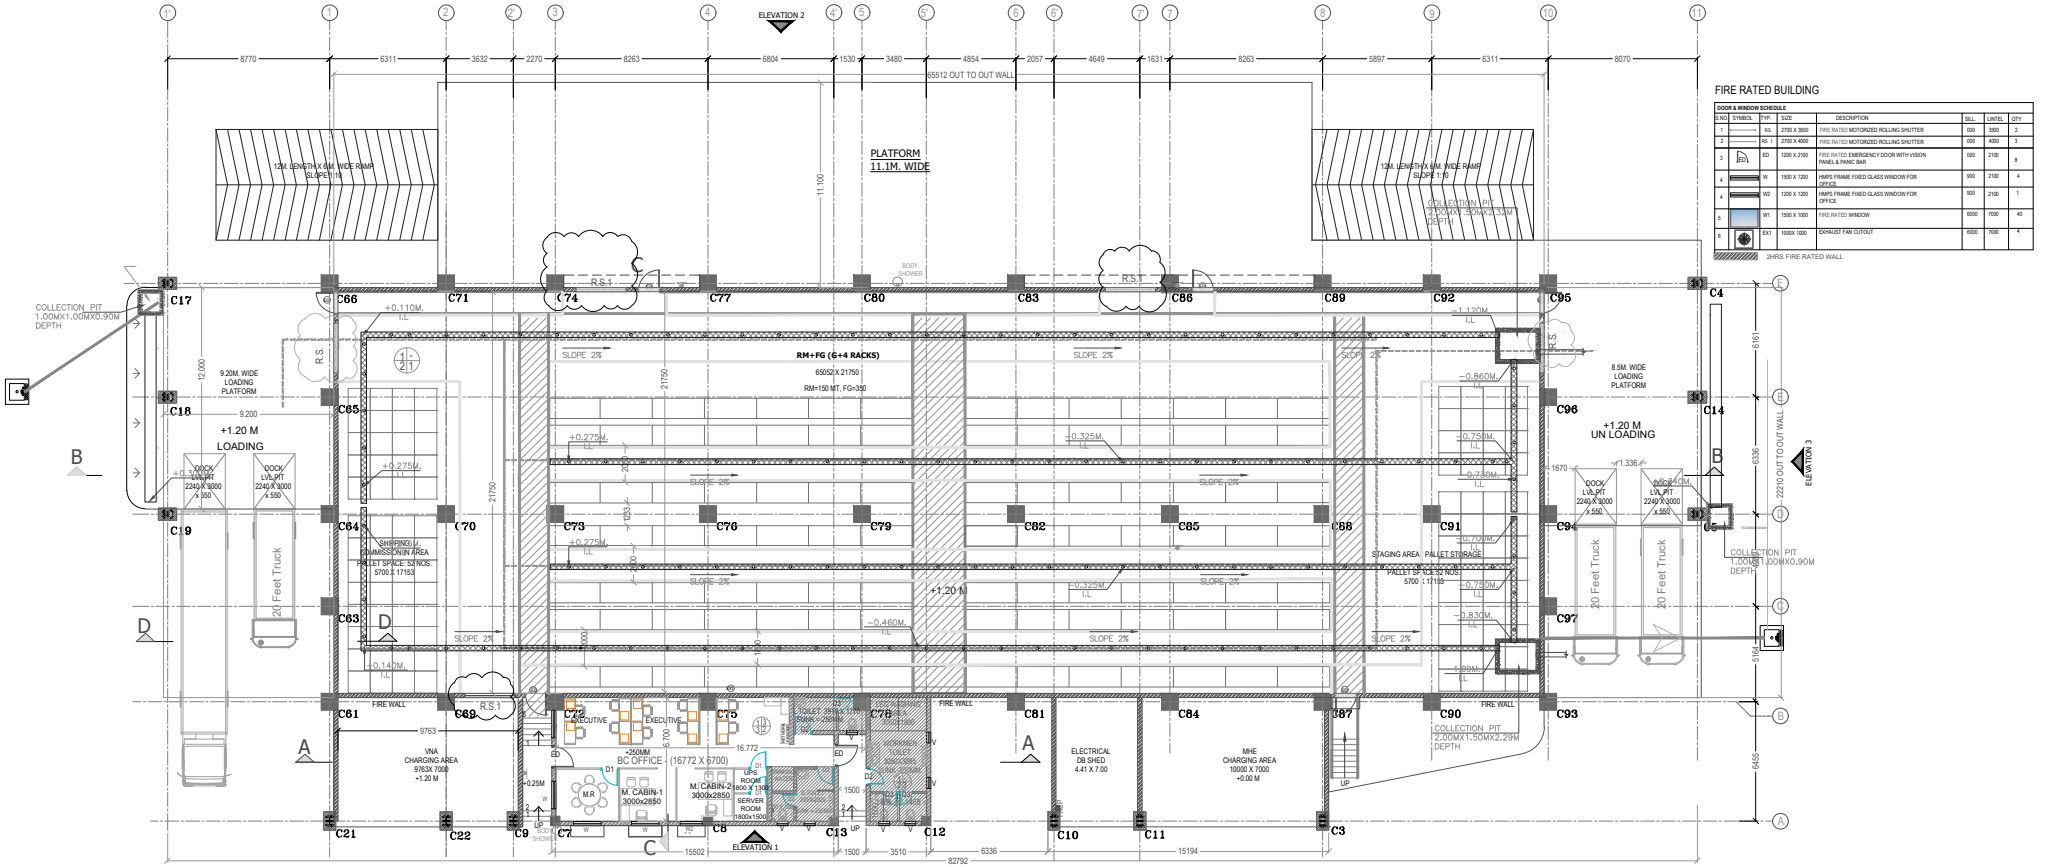


FIRE RATED BUILDING

DOOR & WINDOW SCHEDULE

S.NO	SYMBOL	TYP.	SIZE	DESCRIPTION	SILL	LINTEL	QTY
1		RS	2700 X 3500	FIRE RATED MOTORIZED ROLLING SHUTTER	000	3500	2
2		RS 1	2700 X 4000	FIRE RATED MOTORIZED ROLLING SHUTTER	000	4000	3
3		ED	1200 X 2100	FIRE RATED EMERGENCY DOOR WITH VISION PANEL & PANIC BAR	000	2100	8
4		W	1500 X 1200	HMPS FRAME FIXED GLASS WINDOW FOR OFFICE	900	2100	4
4		W2	1200 X 1200	HMPS FRAME FIXED GLASS WINDOW FOR OFFICE	900	2100	1
5		W1	1500 X 1000	FIRE RATED WINDOW	6000	7000	40
6		EX1	1000X 1000	EXHAUST FAN CUTOUT	6000	7000	4

2HRS FIRE RATED WALL

GROUND FLOOR PLAN