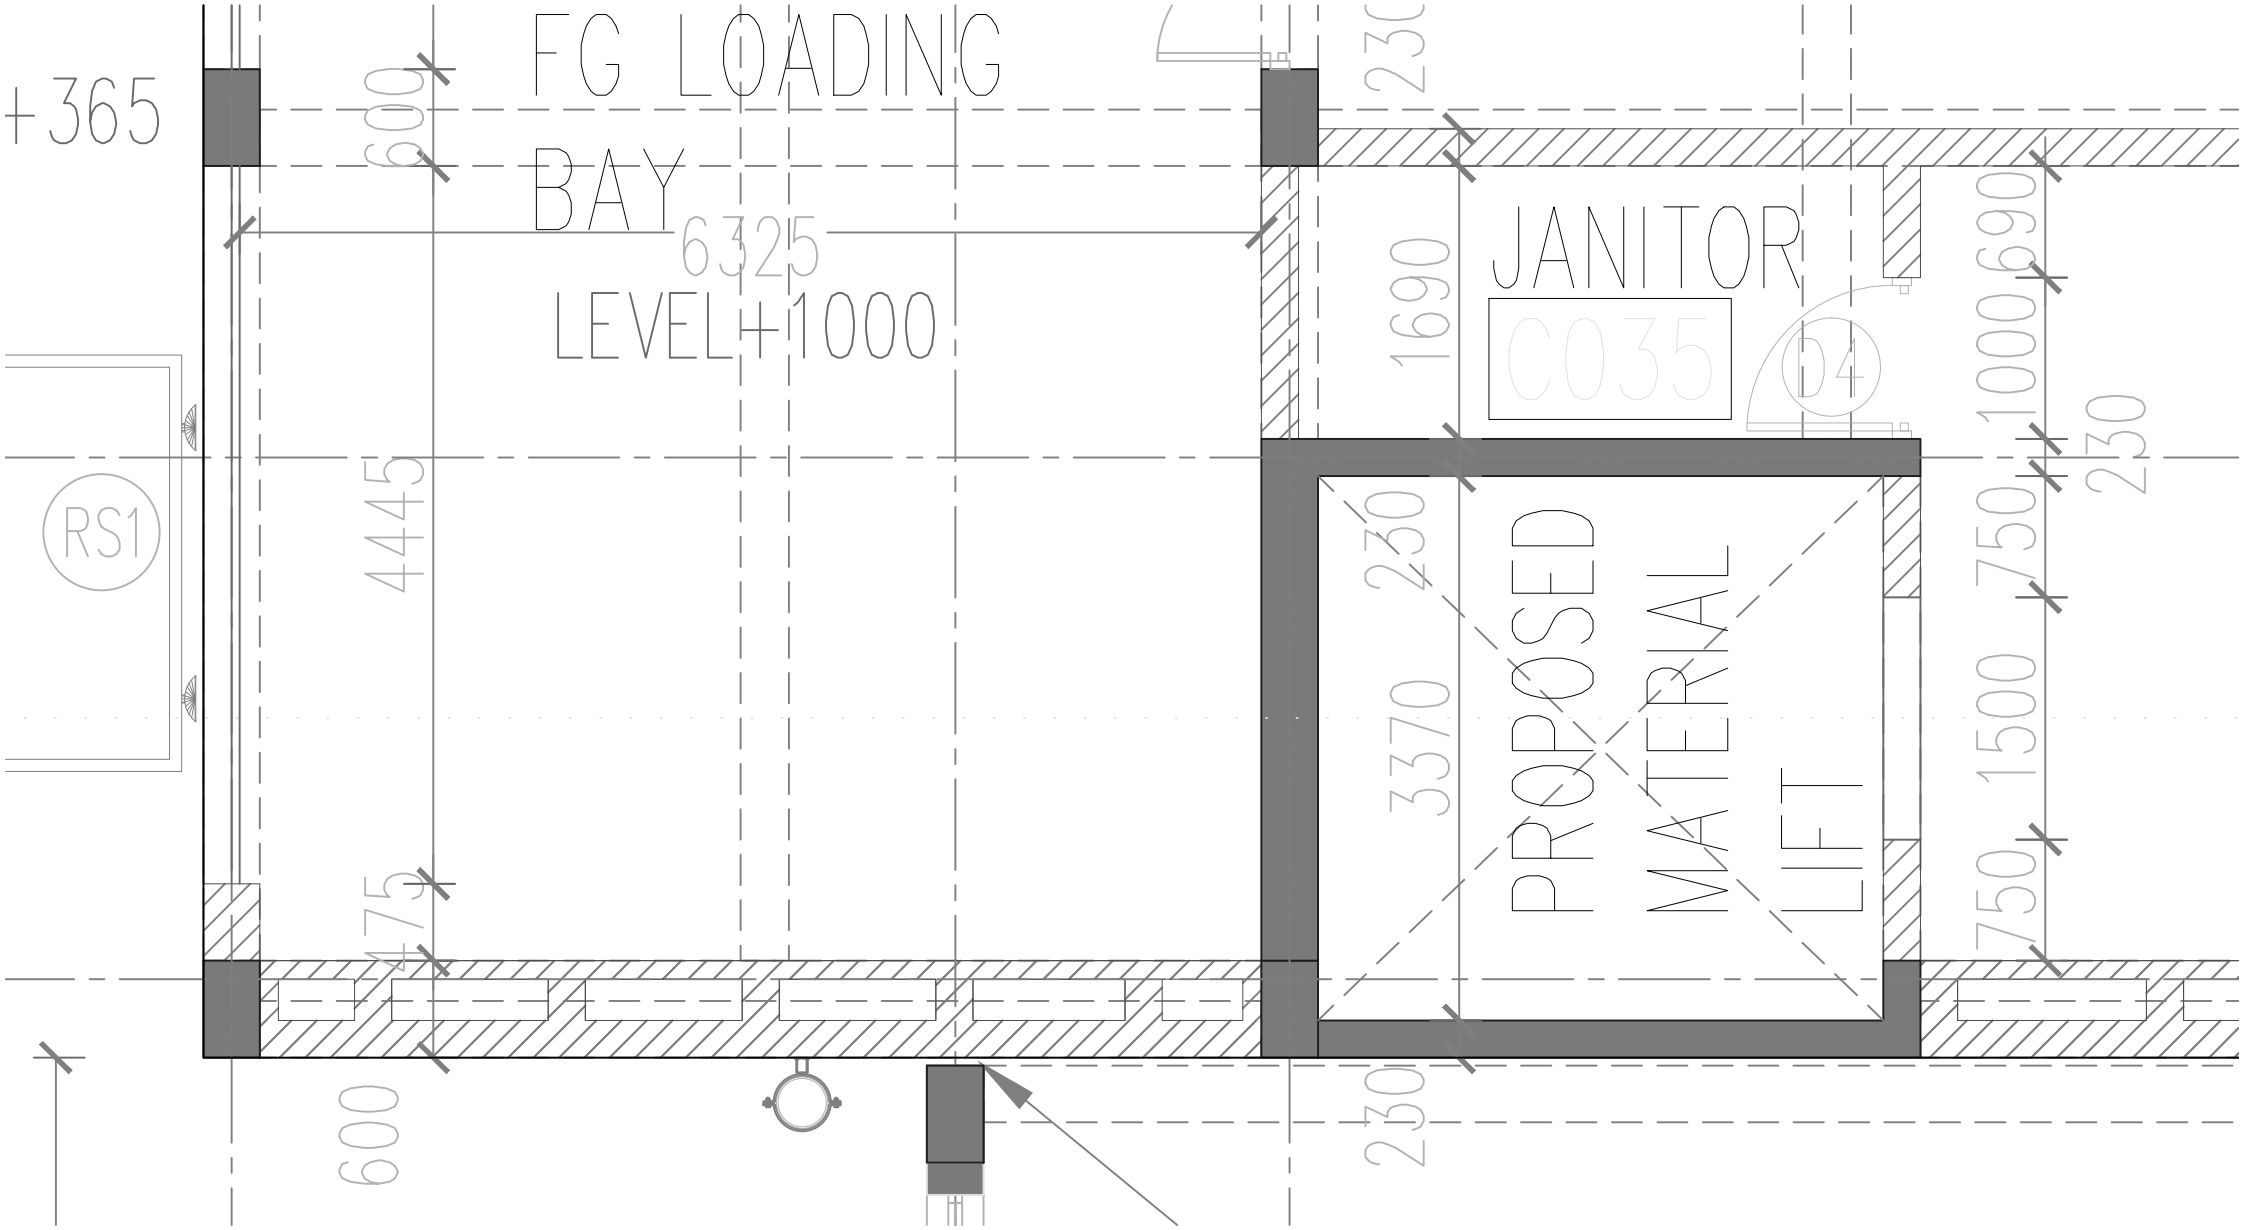
+365
FG LOADING
BAY
6325
LEVEL+1000
600
4445
475
600
RS1
230
1690
JANITOR
C035
04
1000
690
230
230
3370
PROPOSED
MATERIAL
LIFT
750
1500
750
230