


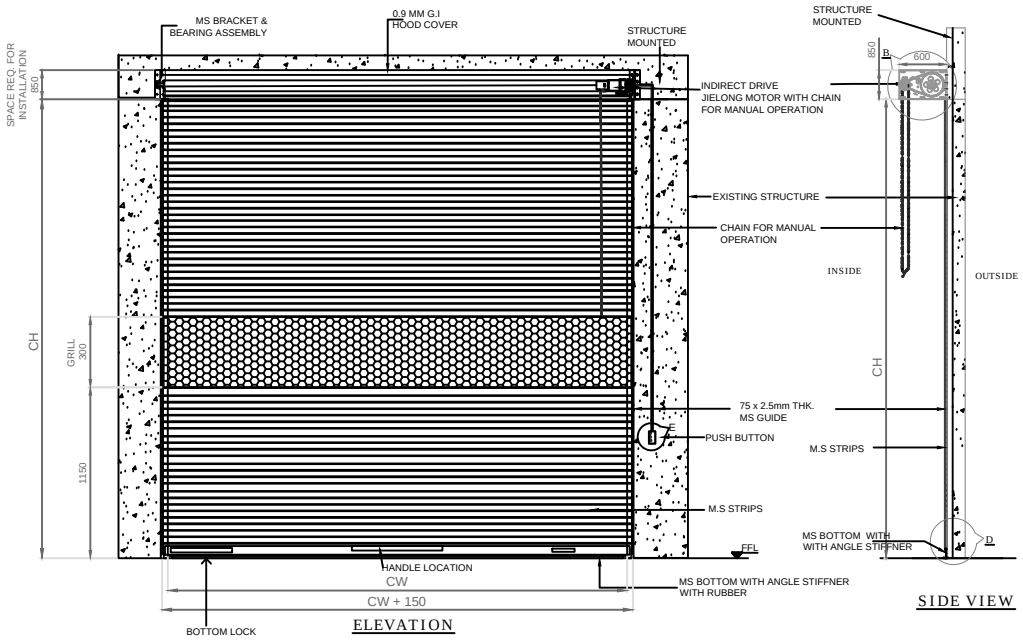


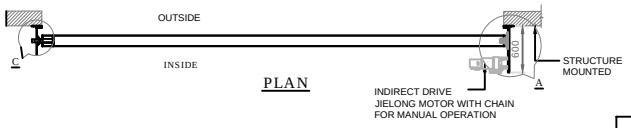


PLAN

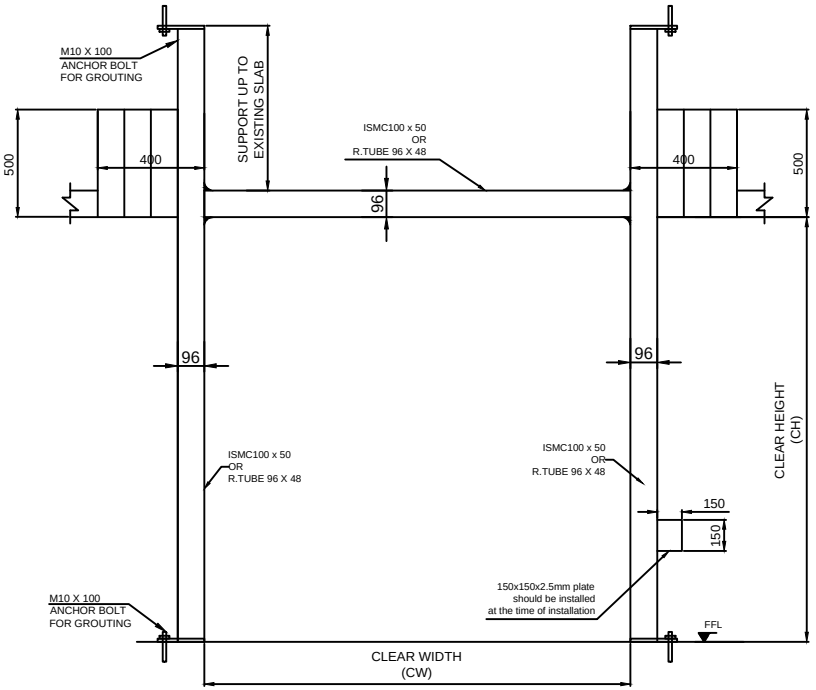


STRUCTURE

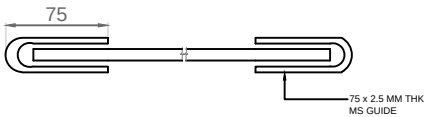


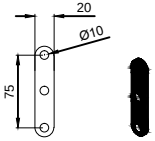


5mm THK. LINK

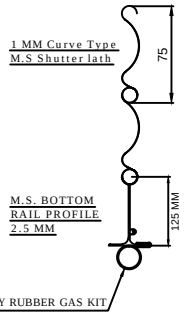


DETAILS : D

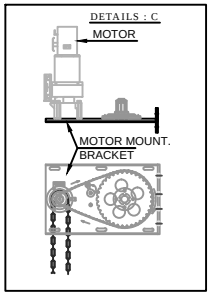

DETAILS : A & B

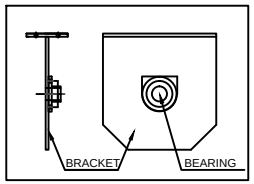

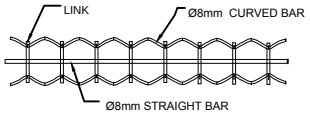

NOTE:
1. REQUIRED TECHNICAL M.S STRUCTURE FOR SHUTTER IN CLIENT SCOPE.
2. TWO COATS OF PRIMER AND TWO COAST OF SYNTHETIC ENAMEL OR POWDER COATING.

RAL CODE-RAL 5002 ULTRA MARINE BLUE

2500	2200	2	RAL -
CLEAR WIDTH (CW)	CLEAR HEIGHT (CH)	QUANTITY	RAL COLOR POWER COATING

REV NO	DATE	DRAWN	REMARK
R02	28.09.20	S.S.	CLEAR HEIGHT CHANGED
R01	28.07.20	P.A	1. STRUCTURE DETAILS ADDED

This drawing & design is the property of NIHVA TECHNOLOGIES. Not to be sold or copied to any other concern.

TITLE: MOTORIZED ROLLING SHUTTER

	NAME	SIGN	DATE
DRAWN	P.A		20.07.2020
CHECK	G.J		20.07.2020
APPRD.			

If any queries contact : design@nihva.com

ALL DIMENSION ARE IN mm

NIHVA TECHNOLOGIES PVT. LTD.
NIHVA TECHNOLOGIES PVT. LTD. PUNE
Tel : 020 66304033
Email:- info@nihva.com
Website:- www.nihva.com

CLIENT -HUHTAMAKI PPL LTD

PROJECT -

SITE LOCATION - KHOPOLI

DWG. NO. : NIHVA/20-21/0034/R02 | REV- R02

SCALE: NTS | WT: | SHEET: