
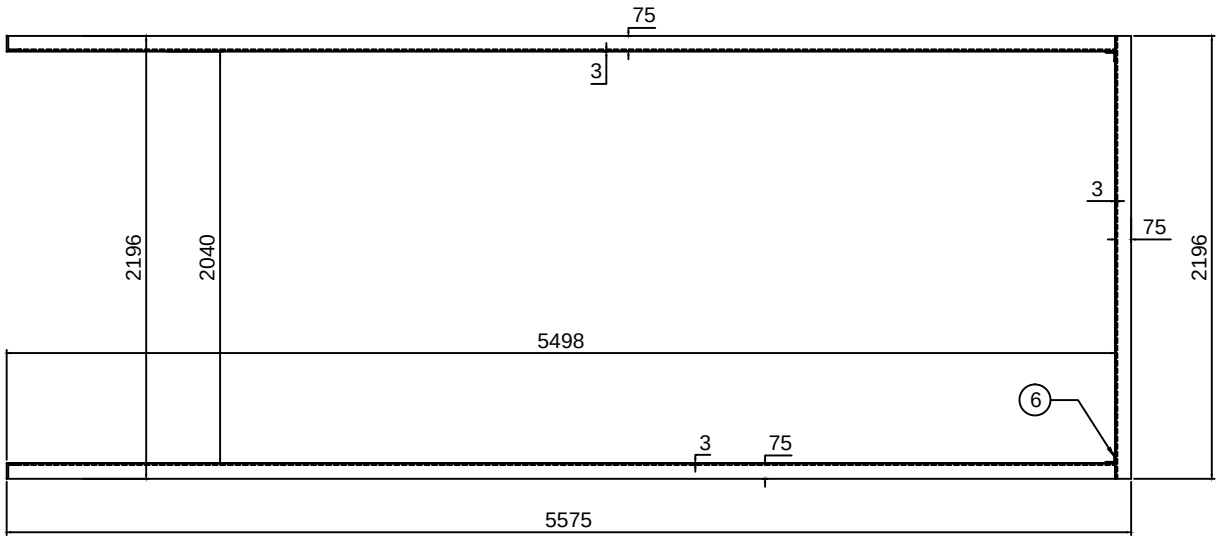


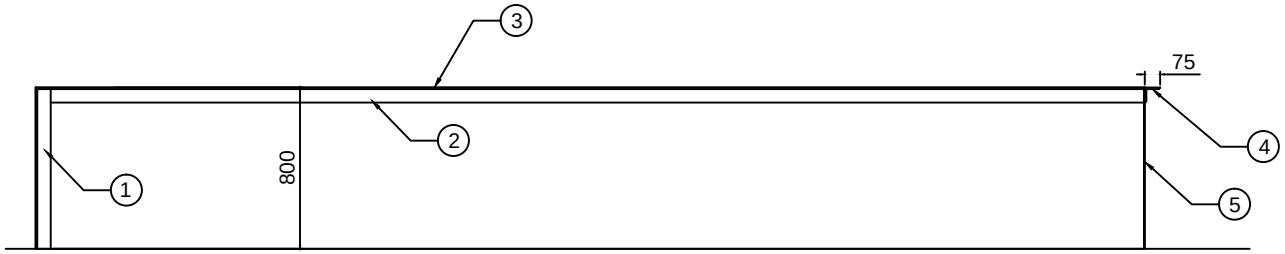

1. ISA 75 X 8 X 800L = 2 NOS
2. ISA 75 X 8 X 5490L = 2 NOS
3. SHEET 800 X 3 X 5498L = 2 NOS
4. ISA 75 X 8 X 2196L = 1 NO
5. SHEET 800 X 3 X 2196L = 1 NO
6. ISA 50 X 5 X 700L = 2 NOS

TOLERANCE :- ± 10mm

This drawing & design is the property of NIHVA TECHNOLOGIES. Not to be sold or copied to any other concern.

TITLE	PIT FRAME ASSLY		
	NAME	SIGN	DATE
DRAWN	P.A		08.08.2020
CHECK	G.J		08.08.2020
APPRD.			

NIHVA TECHNOLOGIES PVT. LTD.
Website:- www.nihva.com
NIHVA TECHNOLOGIES PVT. LTD. PUNE
Tel : 020 66304033
Email:- info@nihva.com

CLIENT -

PROJECT -

SITE LOCATION -

If any queries contact : design@nihva.com

DWG. NO. : NIHVA/20-21/VDR/0036 | REV- R00

ALL DIMENSION ARE IN mm

SCALE: NTS | WT: | SHEET: 01 OF 01