




Client scope
* Drainage area or pipe need to be shift from right side *Roof need to be shift at top Approx 300mm *Gutter need to be close till pipe

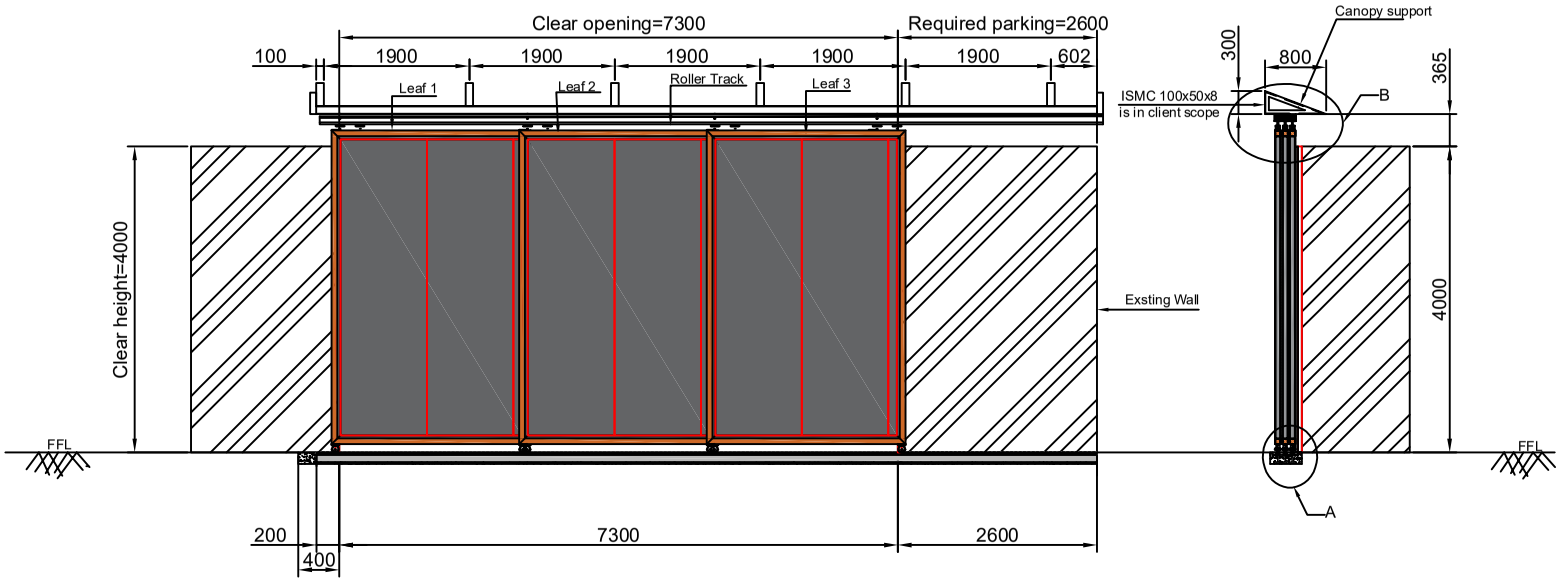

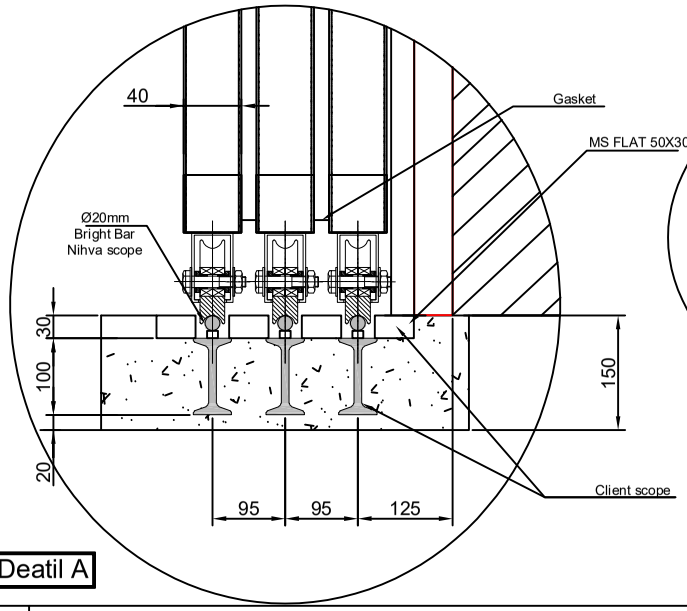

Deatil A

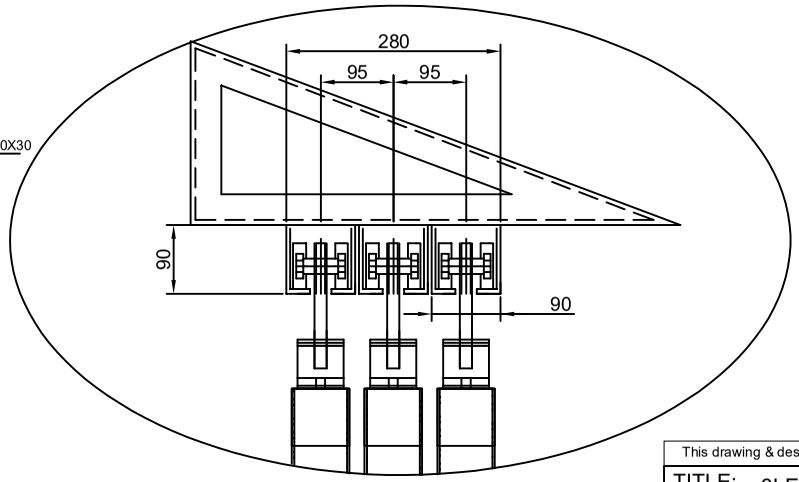

Deatil B

Color code	Color	Approval
9002	Offwhite	
5012	Lightblue	

Note:--

1. All dimension are in MM
2. All Civil work will be in client scope
3. For 7300mm opening we required exact 2600mm parking space if not there will be opening reduce by 100mm
4. Manufacturing,civil and installation tolerance will be ±10mm
5. Top and Bottom track should be in parallal within ±3mm

Rev No.	Revision	Date	Revised By

This drawing & design is the property of NIHVA TECHNOLOGIES. Not to be sold or copied to any other concern.

TITLE:- 3LEAF RIGHT SIDE CRM DOOR 03

NIHVA TECHNOLOGIES PVT. LTD.

NIHVA TECHNOLOGIES PVT. LTD. PUNE
Tel : 020 66304033
Email:- info@nihva.com
Website:- www.nihva.com

	NAME	DATE	SIGN
DRAWN	SUJATA	26/04/2022	
CHECK	M.SUTAR	26/04/2022	
APPRD.	V.TARAK	26/04/2022	

If any queries contact : design@nihva.com

ALL DIMENSION ARE IN mm

CLIENT - LESTECH

LOCATION - POSCO MANGAON

PRODUCT - SLIDING DOOR

DWG NO:-NIHVA/22-23/CLT/0015 | REV- 0

SCALE: NTS | SCALE:-- 1:1 | SHEET: 01 OF 01