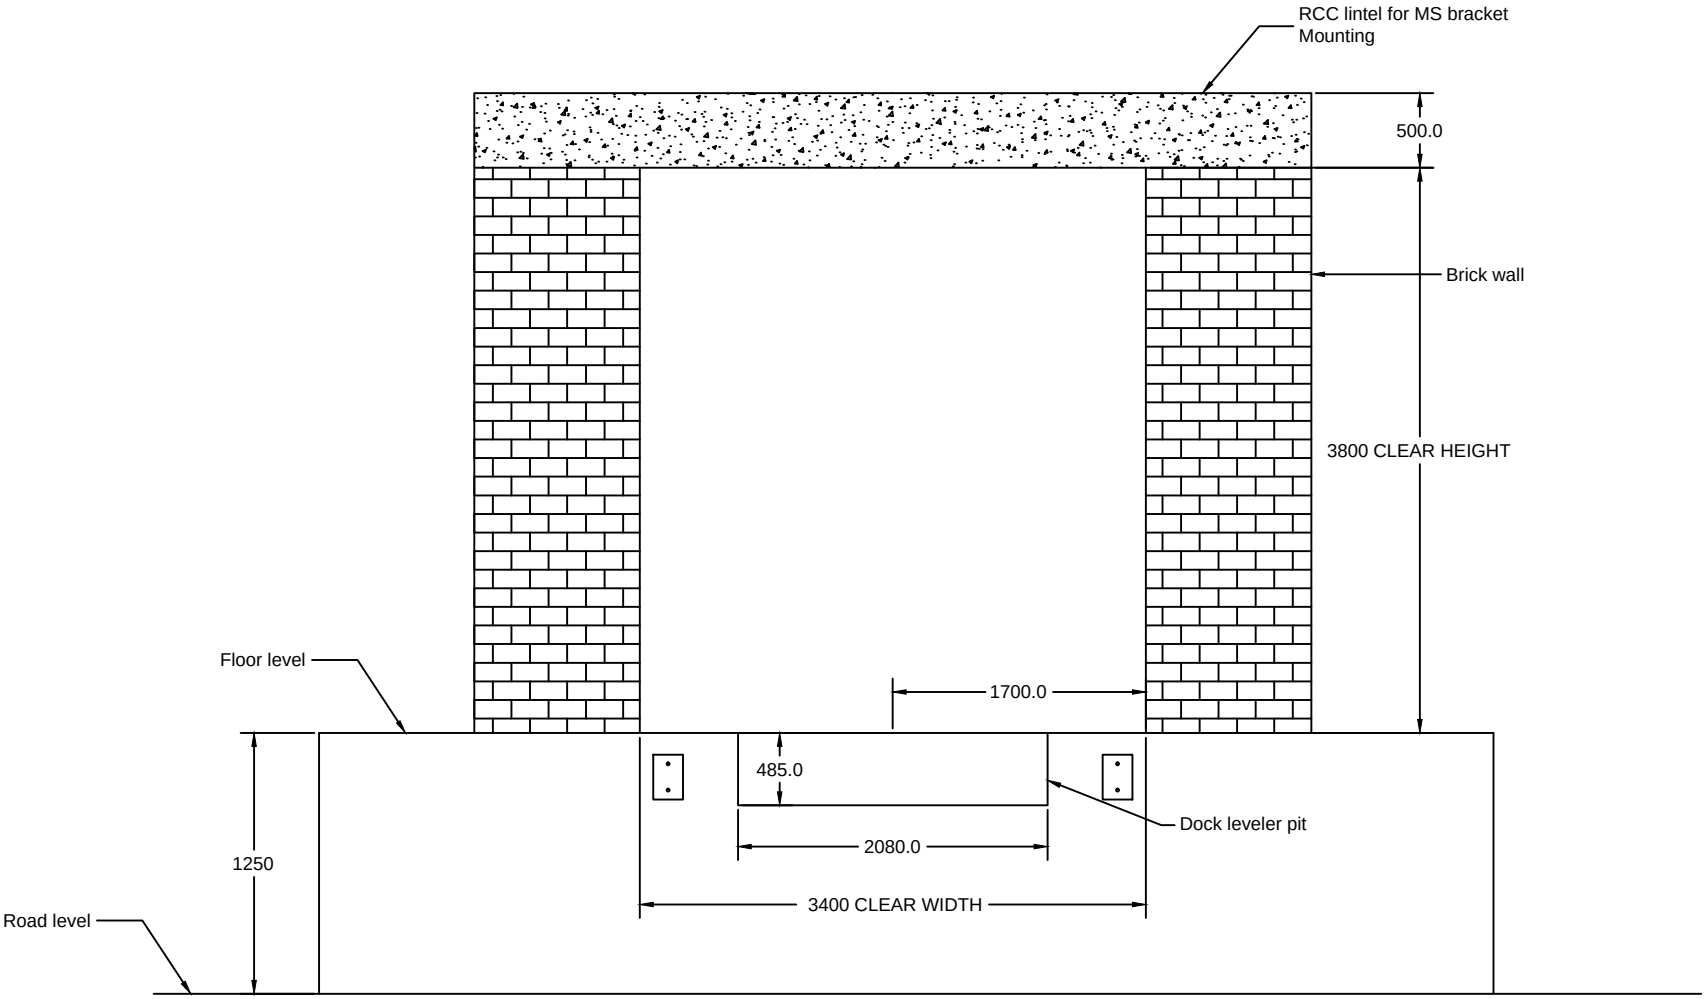

OUTSIDE ELEVATION

This drawing & design is the property of NIHVA TECHNOLOGIES. Not to be sold or copied to any other concern.

TITLE STRUCTURE (OPTION 1) FOR SHUTTER & DOCK SHELTER		
	SIGN	DATE
DRAWN	OMKAR	11/04/17
CHECK	SAGAR P.	11/04/17
REV.		
APPROVAL		
If any queries contact : projects@nihva.com		
ALL DIMENSION ARE IN mm		

NIHVA TECHNOLOGIES PVT. LTD.
NIHVA TECHNOLOGIES PVT. LTD. PUNE
Tel : 020 66304033
Email:- info@nihva.com
Website:- www.nihva.com

CLIENT - ITC		
PROJECT -		
SITE - GUNTUR, A.P.		
DWG. NO. : NIHVA/17-18/0006		
SCALE: NTS	WT:	SHEET: 01 OF 01