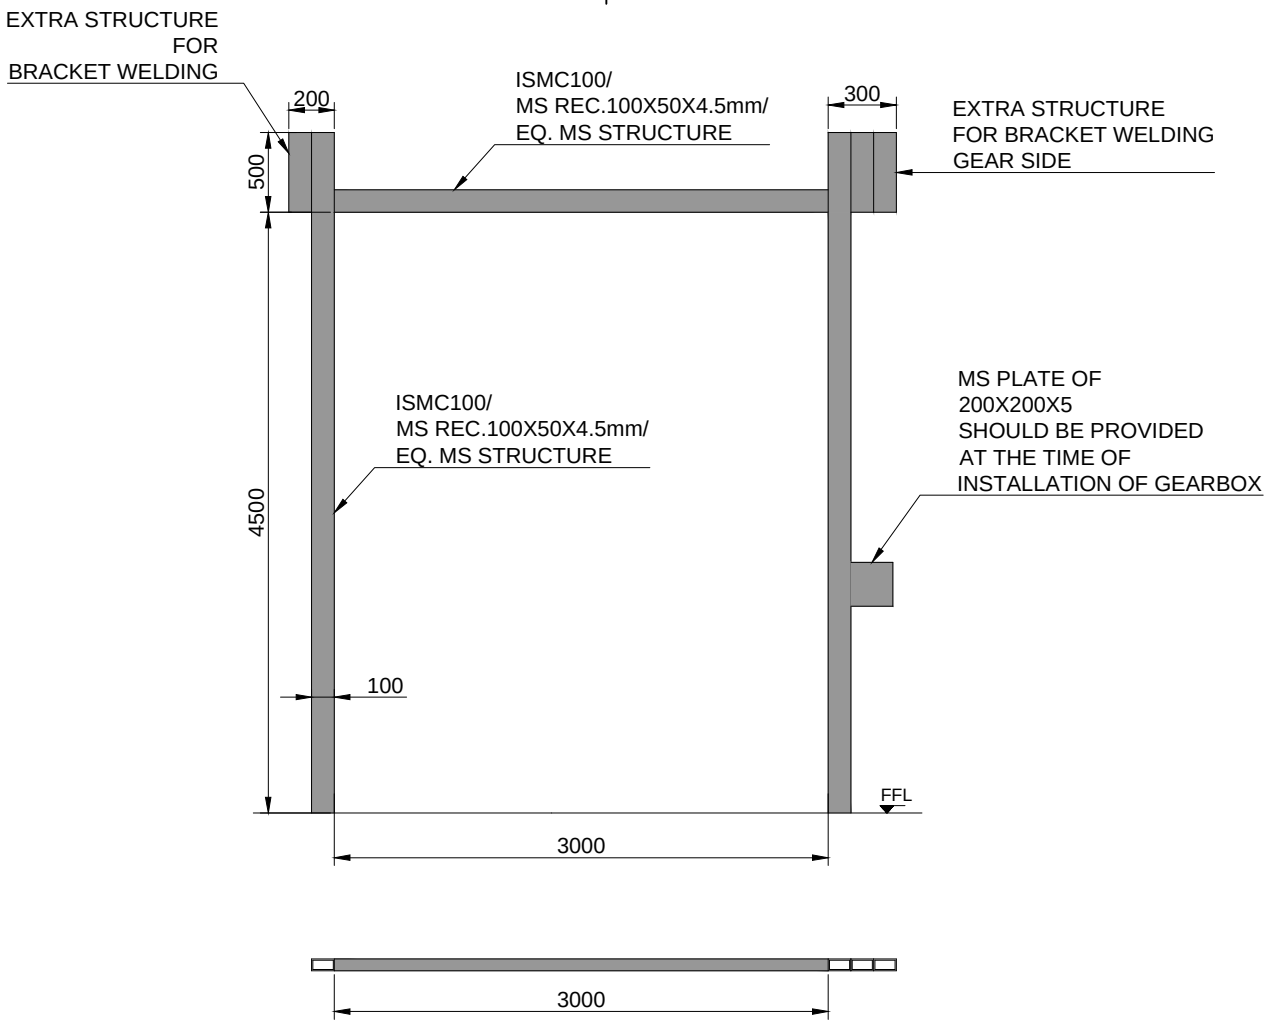


TOLERANCE - ±10mm

This drawing & design is the property of NIHVA TECHNOLOGIES. Not to be sold or copied to any other concern.

TITLE	GEAR OPERATED ROLLING SHUTTER 3m X 4.5 m STRUCTURE			NIHVA TECHNOLOGIES PVT. LTD. PUNE Tel : 020 66304033 Email:- info@nihva.com Website:- www.nihva.com
	NAME	SIGN	DATE	
DRAWN	P.A		16.10.2019	CLIENT - PROGRESSIVE INFRA PROJECT PVT. LTD.
CHECK	G.J		16.10.2019	PROJECT -
APPRD.				SITE LOCATION - PUNE
If any queries contact : design@nihva.com				DWG. NO. : NIHVA/19-20/0137 / REV- R00
ALL DIMENSION ARE IN mm				SCALE: NTS / WT: / SHEET: 01 OF 01

NOTE-
1. ALL CIVIL WORK WILL BE CLIENT'S SCOPE.
2.STRUCTURE REQUIRED FOR SHUTTER IS IN CLIENT'S SCOPE.
3.FINAL FINISH OF SHUTTER WILL BE IN POWDER COATING OF APPROVED COLOR.