
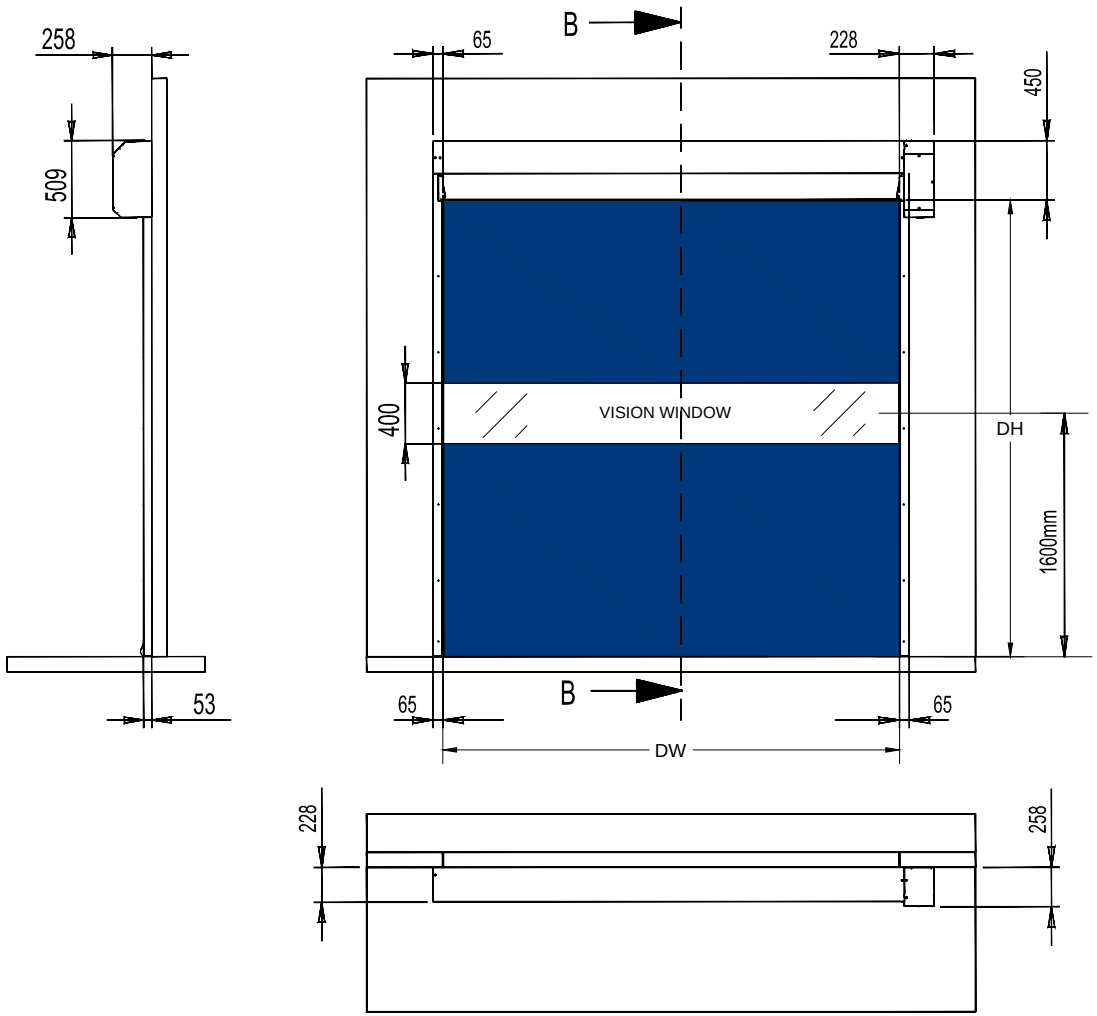


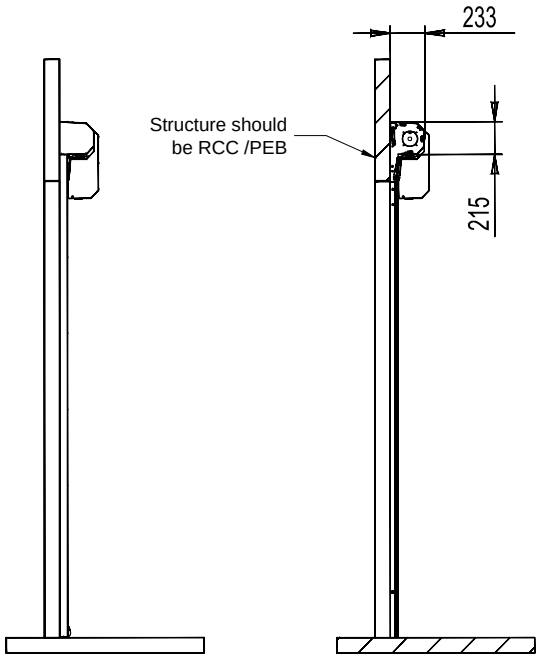

SECTION B-B

DOOR DIMENSION				
SR NO	DW	DH	MOTOR LOCATION	QUANTITY
1	2500	2500	RIGHT HAND SIDE	03
2	3000	3000	RIGHT HAND SIDE	02

REV 1 (21-04-18)- 1. Qty of door of size 3000x3000mm increased by one.
2. color of door curtain would be standard RAL 5002.
Color of door curtain- Ultramarine Blue(RAL 5002)

Note-
1. All Civil work will be in clients scope.
2. Client has to choose motor side (Right/left) according to the site conditions. Standard door comes with Right side Motor mounting.

This drawing & designing is the property of NIHVA TECHNOLOGIES. Not to be sold or copied to any other concern.

TITLE: HIGH SPEED DOOR HS9020G

NIHVA TECHNOLOGIES PVT. LTD. PUNE
Tel : 020 66304033
Email:- info@nihva.com
Website:- www.nihva.com

	NAME	SIGN	DATE
DRAWN	OMKAR		28/03/18
CHECK	PRADEEP		28/03/18
APPROVAL	PRADEEP		28/03/18

If any queries contact : design@nihva.com

ALL DIMENSION ARE IN mm

CLIENT - Mastpro Consulting Engineers Pvt. Ltd.
PROJECT - Mars International India Pvt. Ltd.
SITE - Khed City, Pune
DWG. NO. : NIHVA/17-18/0405/R01 REV- 01
SCALE: NTS WT: SHEET: 01 OF 01