
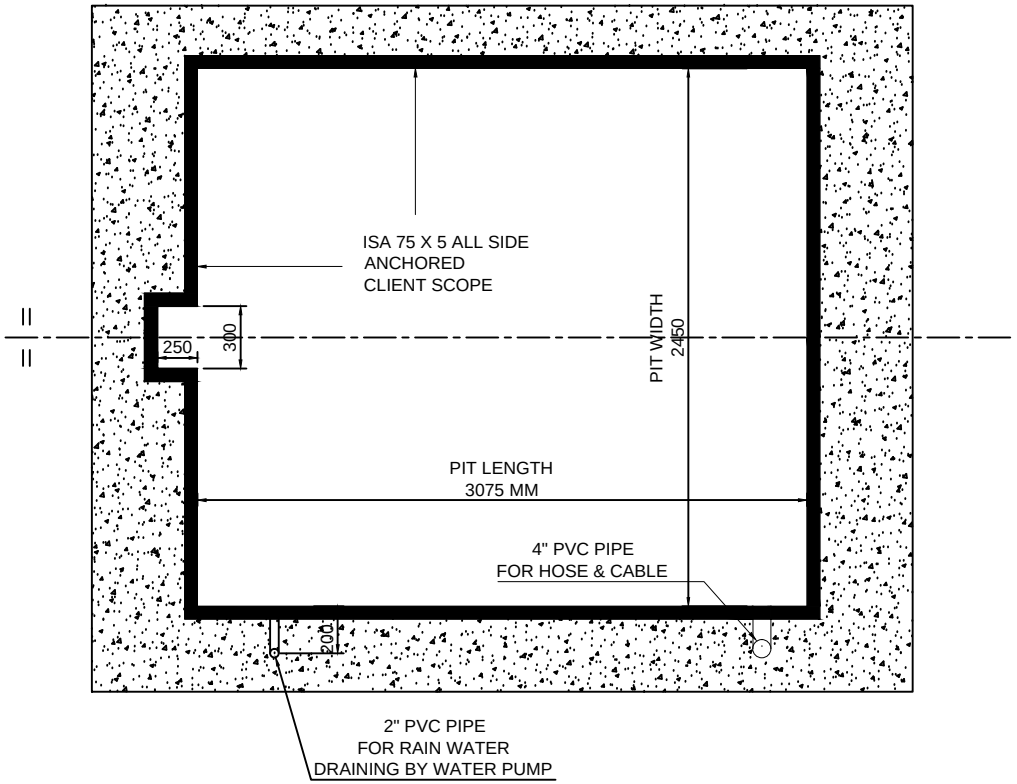


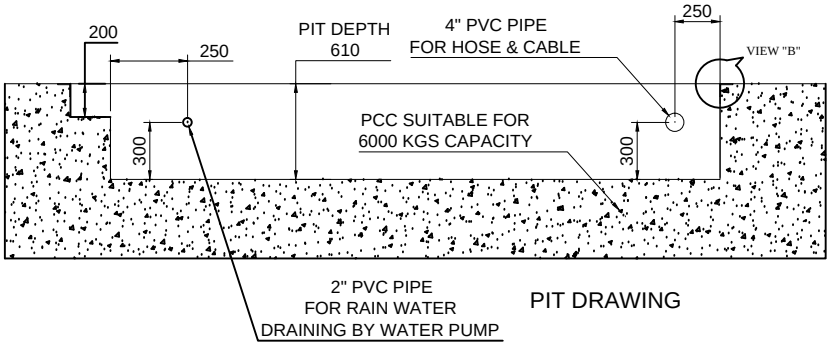


PIT DRAWING

NOTE :

1. HYDRAULIC HOSE LENGTH : 12 MTR
2. ELECTRICAL CABLE : 12 MTR
3. PIT / CIVIL / PVC PIPE WILL BE IN CLIENT SCOPE.
4. COLOR : a. GOLDEN YELLOW.
   b. ULTRA MARINE BLUE.
5. INPUT SUPPLY : 3 PHASE 400 VOLT WITH NEUTRAL.
6. CLEAR PIT DIMENSIONS WITHOUT SKIRTING ISA 75 X 5 = 2460W X 3085L X 610H.

DETAILS B

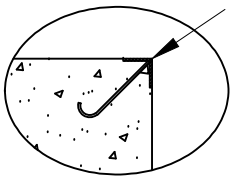

75x75x6 Angle -
Anchored in civil work
(Client scope)

REV NO	DATE	DRAWN	REMARK
R02	28.01.20	P.A	1. DETAILS ADDED.
R01	24.01.20	P.A	1. DRAIN ARRANGEMENT ADD

This drawing & design is the property of NIHVA TECHNOLOGIES. Not to be sold or copied to any other concern.

TITLE	ELECTRO HYDRAULIC SCISSOR LIFT PIT DRG		

NIHVA TECHNOLOGIES PVT. LTD.
NIHVA TECHNOLOGIES PVT. LTD. PUNE
Tel : 020 66304033
Email:- info@nihva.com
Website:- www.nihva.com

	NAME	SIGN	DATE
DRAWN	P.V.A		15.11.2019
CHECK	V.M.T		15.11.2019
APPRD.			

CLIENT - IKEA
PROJECT -
SITE LOCATION -

If any queries contact : design@nihva.com
DWG. NO. : NIHVA/19-20/0153/R02
REV- R02
ALL DIMENSION ARE IN mm
SCALE: NTS
WT:
SHEET: 01 OF 01