


C2 - FIX PANEL
QTY - 2

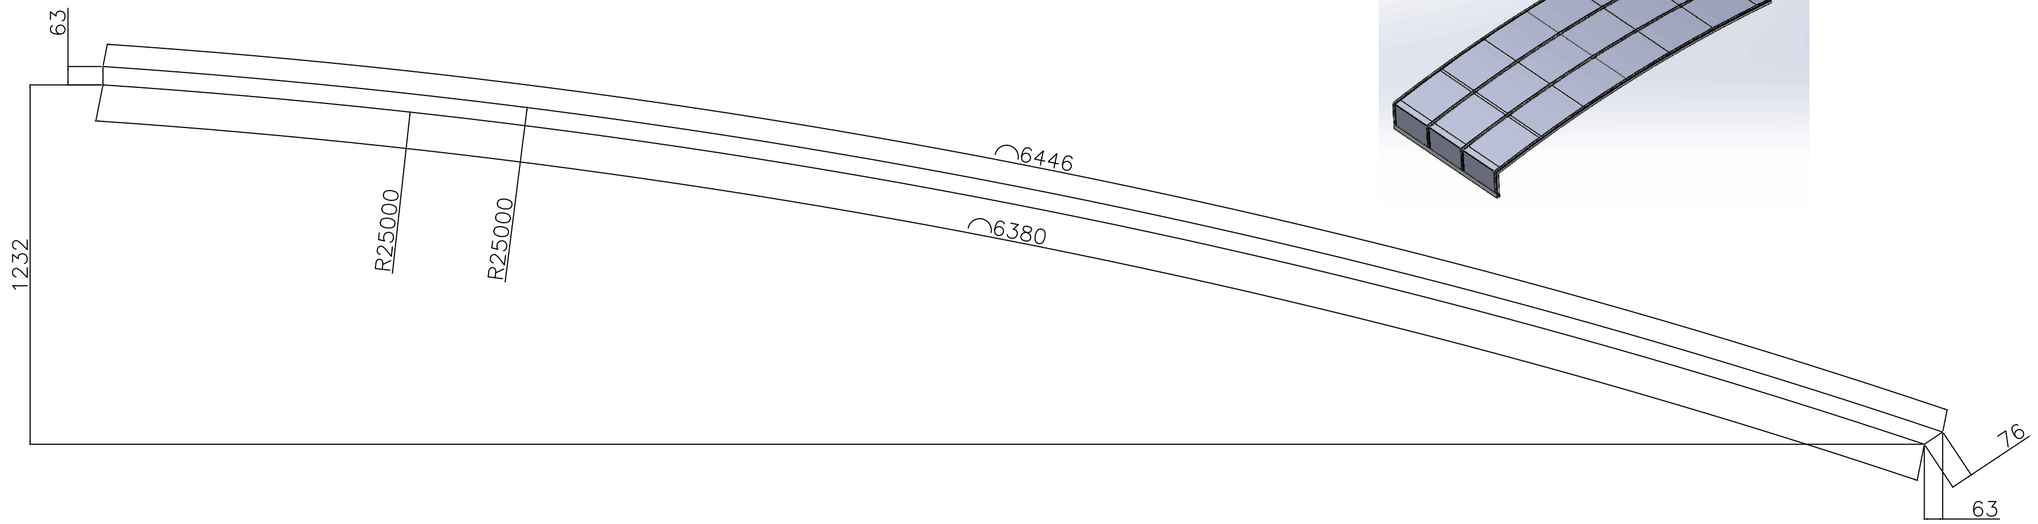


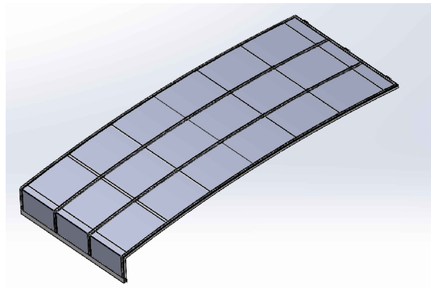


SP4 QTY - 2

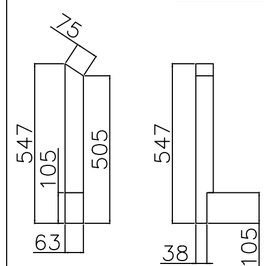

SP5 QTY - 2

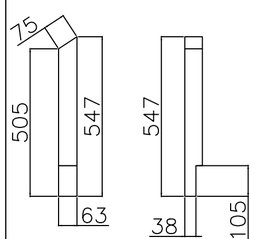

SP6 QTY - 4

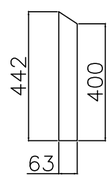

REV NO.	DESCRIPTION	Date	Revised By

	NAME	DATE	SIGN
DRAWN	MAHESH S.	22/10/22	
CHECK	MAHESH S.	22/10/22	
APPRD.	VIJAY T.	22/10/22	

TITLE:- PANEL - 2

NIHVA TECHNOLOGIES PVT. LTD.

NIHVA TECHNOLOGIES PVT. LTD. PUNE
Tel : 020 66304033
Email:- info@nihva.com
Website:- www.nihva.com

CLIENT - NIHVA TECHNOLOGIES PVT.LTD

LOCATION -

PRODUCT: FIX & RETRACTABLE ROOF

If any queries contact : design@nihva.com

DWG NO:-NIHVA/22-23/MFG/0048 REV- 0

ALL DIMENSION ARE IN mm

SCALE: NTS SCALE:-- 1:1 SHEET: 01 OF 01