

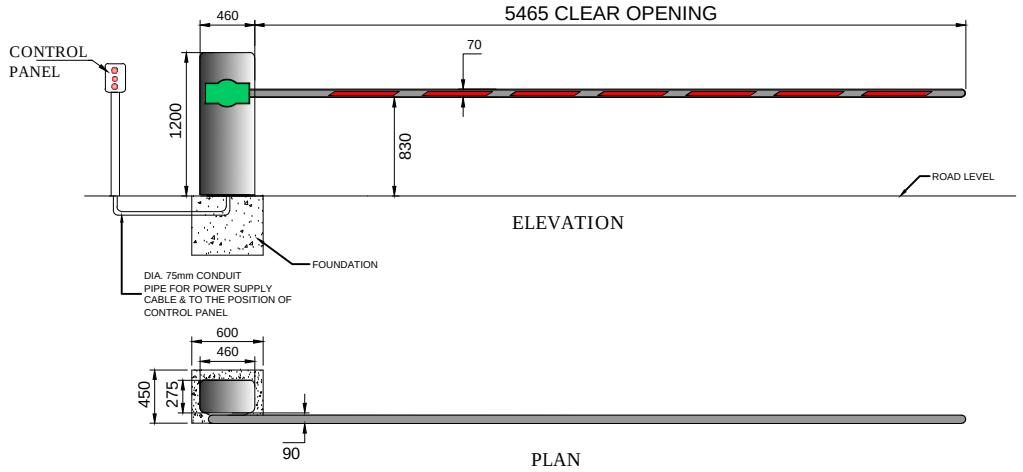


ELEVATION

PLAN

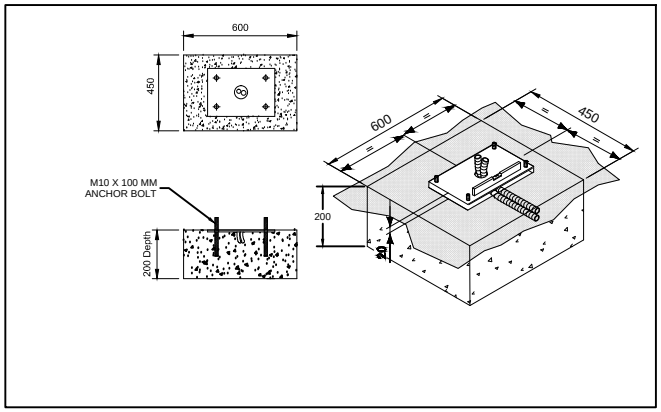

FOUNDATION DETAILS

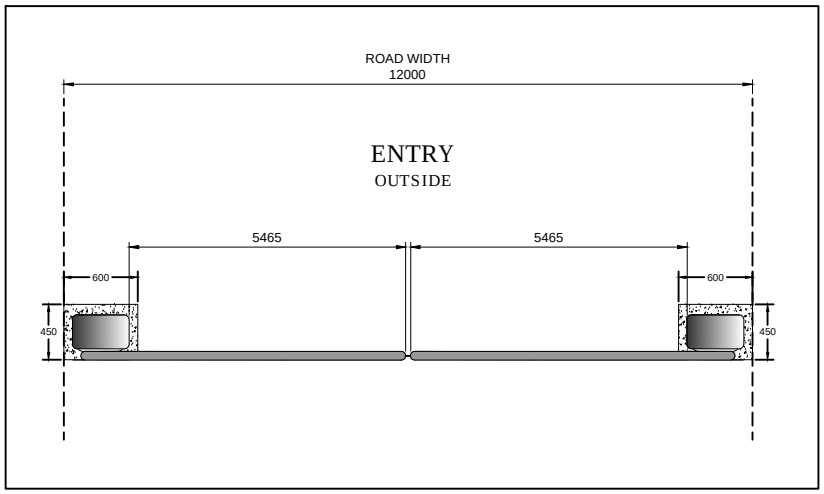

REV NO	DATE	DRAWN	REMARK
R02	14-09-2020	S.S	FOUNDATION DETAILS CHANGE
R01	14-09-2020	S.S.	BOOM LENGTH CHANGED

TOLERANCE - ±10mm

This drawing & design is the property of NIHVA TECHNOLOGIES. Not to be sold or copied to any other concern.

TITLE: BOOM BARRIER

NIHVA TECHNOLOGIES PVT. LTD. PUNE
Tel : 020 66304033
Email:- info@nihva.com
Website:- www.nihva.com

	NAME	SIGN	DATE
DRAWN	P.A		05.09.2020
CHECK	G.J		05.09.2020
APPROVAL			

CLIENT - INOX AIR PRODUCTS PVT LTD

PROJECT -

SITE LOCATION - PUNE

DWG. NO. : NIHVA/20-21/0049/R01 | REV-R01

If any queries contact : projects@nihva.com

SCALE: NTS | WT: | SHEET: 01 OF 01

ALL DIMENSION ARE IN mm