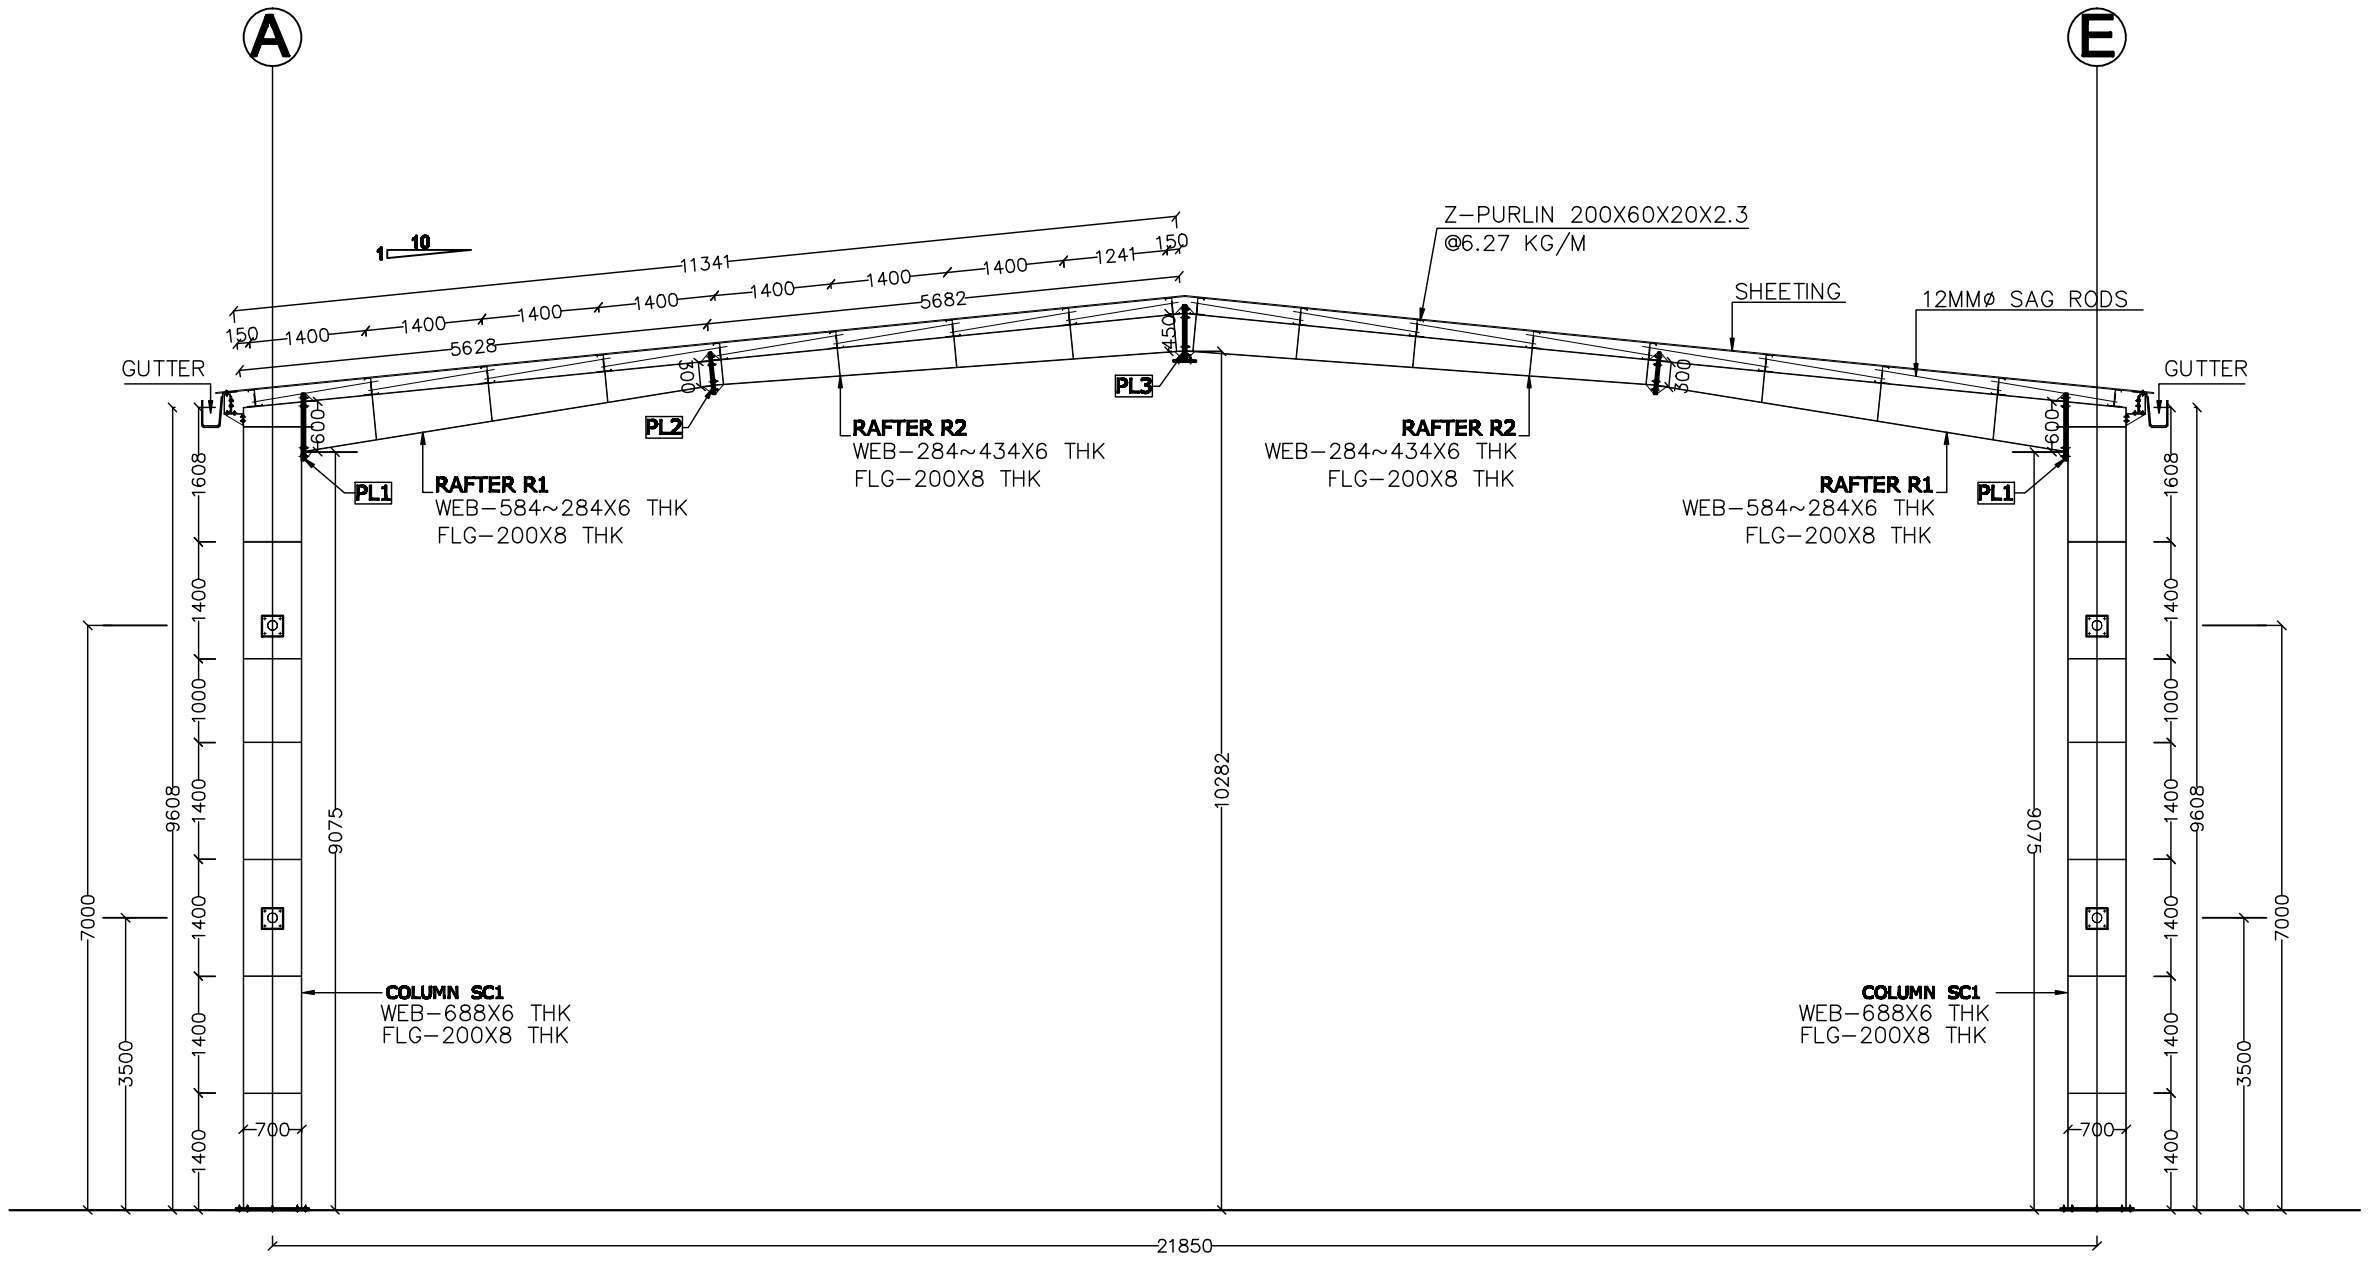


PORTAL FRAME 2 ELEVATION
GRID LINE -03 TO 05

KEY PLAN :-

LEGEND :-

REINFORCED CONCRETE

230MM THK BRICK WALL

STRUCTURAL GLAZING

N

GENERAL NOTES :

*ALL DIMENSIONS ARE IN MILLIMETRES AND ARE UNFINISHED DIMENSIONS UNLESS OTHERWISE SPECIFIED.

*ALL LEVELS ARE IN METRES AND ARE UNFINISHED LEVELS UNLESS OTHERWISE SPECIFIED.

*DO NOT SCALE DRAWINGS, ONLY WRITTEN DIMENSIONS SHALL BE FOLLOWED, ANY DISCREPANCIES NOTED SHALL BE BROUGHT TO THE NOTICE OF THE ARCHITECT PRIOR TO EXECUTION.

SCHEDULE OF JOINERY

TYPE	DESCRIPTION	SIZE	NO.

STRUCTURAL NOTES :

REV.	DESCRIPTION	DATE	BY	CHD.

AMENDMENT

GRAPHIC SCALE: 0 0.5M 2M 4M / 0.5M 0 1M 3M 5M

CLIENT:
HANGER
AT PUNE

PROJECT LOCATION:
PUNE

DRAWING TITLE:
GENERAL ARRANGEMENT DRAWINGS

PROJECT ID:

DRAWING NO:

Astre Infra
Private Limited
imagine and its done
691, Bemciel Indl. Estate,
Khanapur Rd.
Udyambag, Belgaum- 590008.
www.astreinfra.com

THESE DRAWINGS ARE UNDER COPYRIGHT AND ARE THE PROPERTY OF ASTRE INFRA PVT. LTD.. NONE OF THE DRAWINGS AND RELATED DOCUMENTS CAN BE REPRODUCED, COPIED IN WHOLE OR IN PART WITHOUT PRIOR EXPRESSED WRITTEN CONSENT OF ASTRE INFRA PVT.LTD. THESE DRAWINGS ARE NOT TO BE USED FOR ANY OTHER PURPOSE THAN WHICH IT HAS BEEN LOANED. AFTER FULFILLING THE PURPOSE OF ISSUE THE DRAWINGS SHALL BE RETURNED TO ASTRE INFRA PVT.LTD.