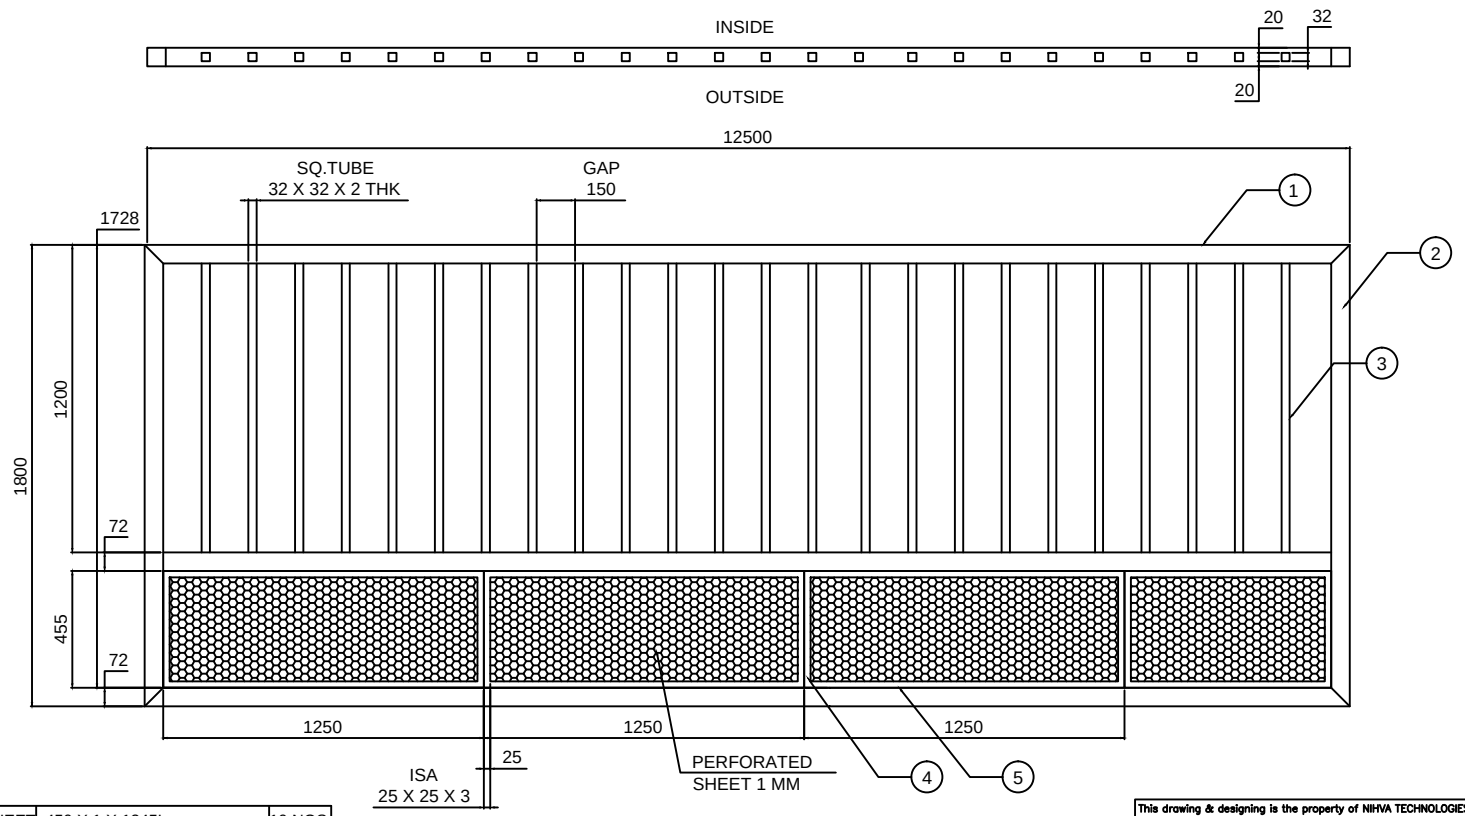


SR NO	DESCRIPTION	SPECIFICATION	QTY
6	PERFO. SHEET	450 X 1 X 1245L	10 NOS
5	ISA	25 X 25 X 3 THK X 1250L	20 NOS
4	ISA	25 X 25 X 3 THK X 455L	22 NOS
3	SQ. TUBE	32 X 32 X 2 THK X 1128L	38 NOS
2	SQ. TUBE	72 X 72 X 3.2 THK X 1800L	2 NOS
1	SQ. TUBE	72 X 72 X 3.2 THK X 12500L	2 NOS

This drawing & designing is the property of NIHVA TECHNOLOGIES. Not to be sold or copied to any other concern.

TITLE: LEAF DRAWING

	NAME	SIGN	DATE
DRAWN	P.A		26.12.19
CHECK	G.J		26.12.19
APPROVAL			

If any queries contact : design@nihva.com

ALL DIMENSION ARE IN mm

NIHVA
NIHVA TECHNOLOGIES PVT. LTD.
NIHVA TECHNOLOGIES PVT. LTD. PUNE
Tel : 020 66304033
Website:- www.nihva.com
Email:- info@nihva.com

CLIENT -

PROJECT -

SITE LOCATION -

DWG. NO. : NIHVA/19-20/VDR/254 REV.:- 0

SCALE: NTS WT: SHEET: 01 OF 01