


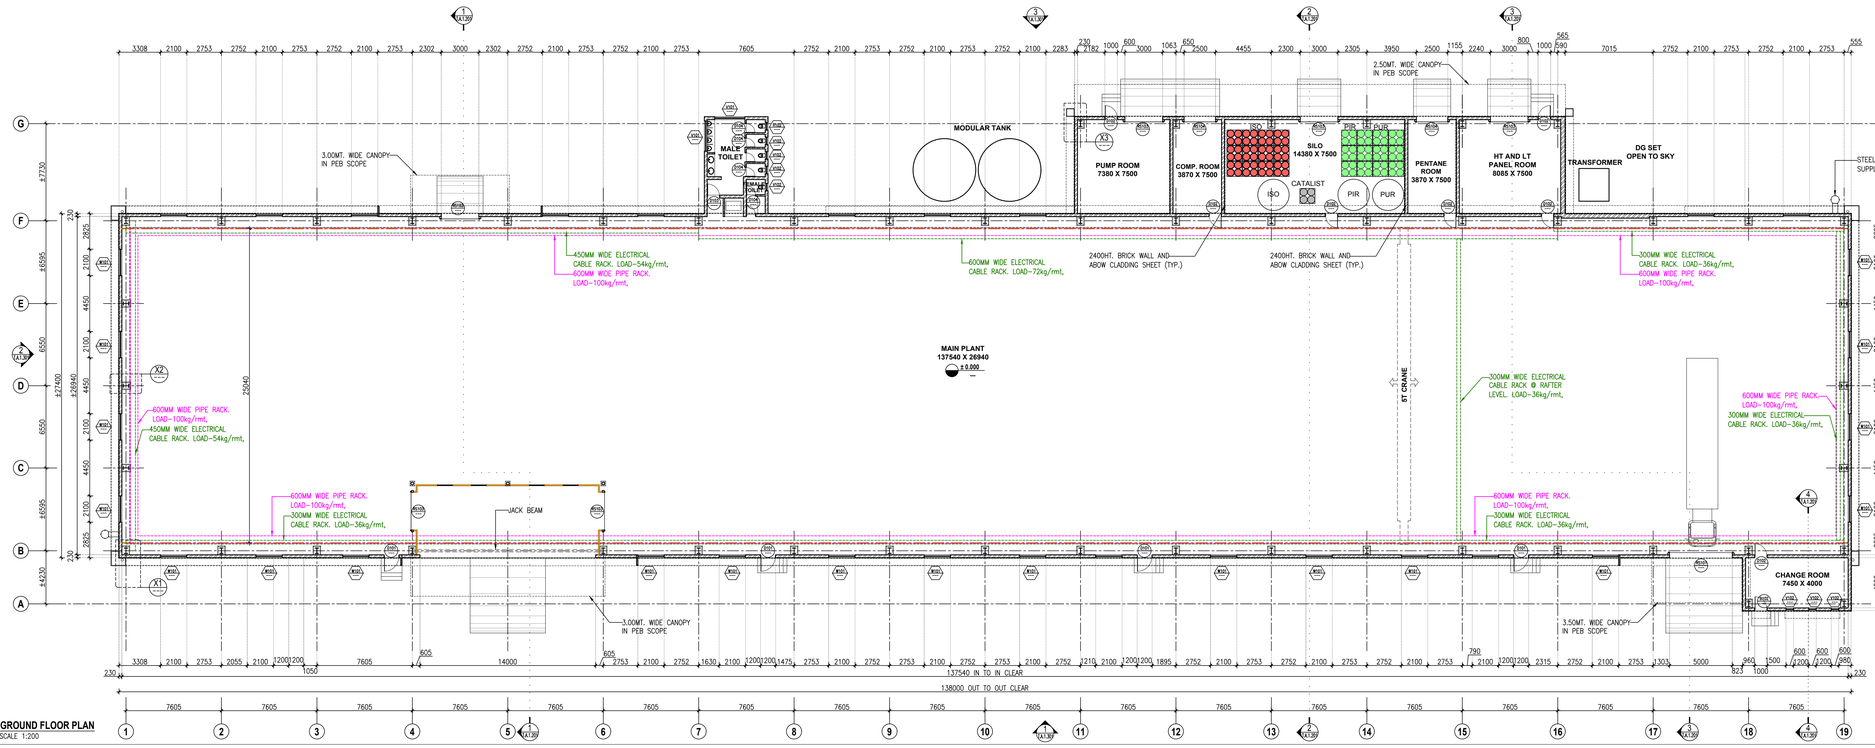

1 GROUND FLOOR PLAN
SCALE 1:200

THIS DRAWING & DESIGN IS THE SOLE PROPERTY OF VMS & SHALL NOT BE COPIED, TRACED OR REPRODUCED BY ANY MEANS WITHOUT PRIOR WRITTEN CONSENT OF THE FIRM.

GENERAL NOTES :

1. ALL THE DIMENSIONS ARE UNFINISHED DIMENSIONS.
2. ALL DIMENSIONS ARE IN MM AND LEVELS ARE IN MT, UNLESS OTHERWISE MENTIONED.
3. ALL THE DIMENSIONS SHALL BE READ & NOT TO BE MEASURED.
4. IN CASE OF ANY DISCREPANCY, BRING IT TO THE NOTICE OF THE ARCHITECT IMMEDIATELY.
5. DETAIL DRAWING PRECEDES THE GENERAL DRAWING

IMPORTANT NOTES :

1. DETAILS SHOWN IN THIS DRAWING ARE INDICATIVE ONLY AND TO PROVIDE GENERAL IDEA OF THE PROPOSED BUILDING.THEY ARE NOT TO BE CONSIDERED AS EXHAUSTIVE AND EXACT REPRESENTATIVE OF THE PROPOSED BUILDING.
2. SUPPORTING STRUCTURE OF ROLLING SHUTTER, CABLE RACKS AND PIPE RACKS WILL BE IN SCOPE OF PEB VENDOR.
3. EXTERNAL COLOR SCHEME, GUTTER, RAIN WATER PIPE SHALL BE AS PER TENDER SPECIFICATIONS.
4. TENDERER SHALL VISIT THE SITE AND GET THOROUGHLY ACQUAINTED WITH THE SITE CONDITION BEFORE SUBMITTING THE BID.
5. SCOPE OF PEB VENDOR TO BE STRICTLY FOLLOW AS PER TENDER DOCUMENT.

STANDARD DRAWING SYMBOLS:

- + FINISHED LEVEL
- + UNFINISHED LEVEL

SECTION SYMBOL
UPPER HALF INDICATES DIAGRAM NO. (NUMERICAL VALUE) IN DRAWING SHEET & LOWER HALF INDICATES DRAWING NO.

ELEVATION SYMBOL
UPPER HALF INDICATES DIAGRAM NO. IN DRAWING SHEET & LOWER HALF INDICATES DRAWING NO.

WINDOW SYMBOL
UPPER HALF INDICATES WINDOW NO. & LOWER HALF INDICATES DRAWING NO.

DOOR SYMBOL
UPPER HALF INDICATES DOOR NO. & LOWER HALF INDICATES DRAWING NO.

GRAPHIC LEGEND :

BRICK WALL CUT IN PLAN/SECTION.

RCC COLUMN CUT IN PLAN.

SCHEDULE OF OPENINGS:


MKD.	SIZE	SILL HT.	REMARKS
RS101	5000 X 5000	---	MECHANICALLY OPERATED M.S. ROLLING SHUTTERS.
RS102	3000 X 4000	---	MECHANICALLY OPERATED M.S. ROLLING SHUTTERS.
RS103	3000 X 3000	---	MECHANICALLY OPERATED M.S. ROLLING SHUTTERS.
RS104	2500 X 3000	---	MECHANICALLY OPERATED M.S. ROLLING SHUTTERS.
D101	1200 X 2100	---	FIRE RATED DOOR
D102	1000 X 2100	---	G.I. DOOR
D103	1000 X 2100	---	ALUMINUM FRAME WITH BOTH SIDE LAMINATED FLUSH DOOR
D104	750 X 2100	---	ALUMINUM FRAME WITH BOTH SIDE LAMINATED FLUSH DOOR
W101	2100 X1200	900	ALUMINUM FRAME WITH PARTLY FIXED GLASS AND PARTLY FIXED ALUMINUM LOUVERS WITH S.S. MOSQUITO NET
V101	2400 X600	1500	ALUMINUM FRAME WITH FIXED GLASS LOVERS
V102	600 X600	1500	ALUMINUM FRAME WITH FIXED GLASS LOVERS

FOR TENDER

NO.	DATE	DESCRIPTION	DRAWN BY	CHECKED BY
R0	-	-	-	-

REVISION HISTORY

KEY PLAN
SCALE : N.T.S.

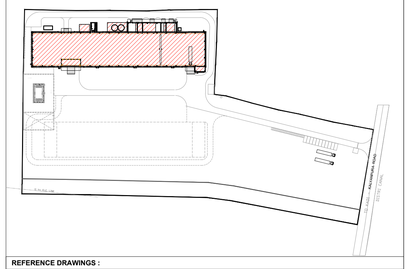

REFERENCE DRAWINGS :

01. ARCHITECTURAL :	-
02. STRUCTURAL :	-
03. HVAC :	-
04. ELECTRICAL :	-
05. UTILITIES :	-

GROUND FLOOR PLAN AND DETAILS

MAIN PLANT BUILDING

SUCHI FOAMS PVT. LTD. AT - KHAVAD, TA - KADI.

PROJECT NO.			
1219	SCALE : 1:200	DRAWN :	PARESH
		CHECKED:	PARESH
	DATE : 26-07-2019	APPROVED:	NITESH
		COORDINATION CHECKED:	NITESH

VMS ENGINEERING & DESIGN SERVICES (P) LTD.
CHITRAKOOT FLATS, B/H TIMES OF INDIA, OFF ASHRAM ROAD,
AHMEDABAD-380 009. PHONE: +91 (079) 2658-8829, 4023-6236
WWW.VMSCONSULTANTS.COM

SHEET SIZE	DRAWING NO.	TENDER	REVISION:
600x 1000	T.A.1.101	T	R0