
THIS PRINT IS THE PROPERTY OF NIHVA IT IS TO BE USED ONLY FOR THE PURPOSE FOR WHICH IT WAS LENT
AND MUST NOT BE USED IN ANY WAY DERTIMENTAL TO THE INTEREST OF THIS COMPANY AND IS SUBJECT TO RETURN ON DEMAND.

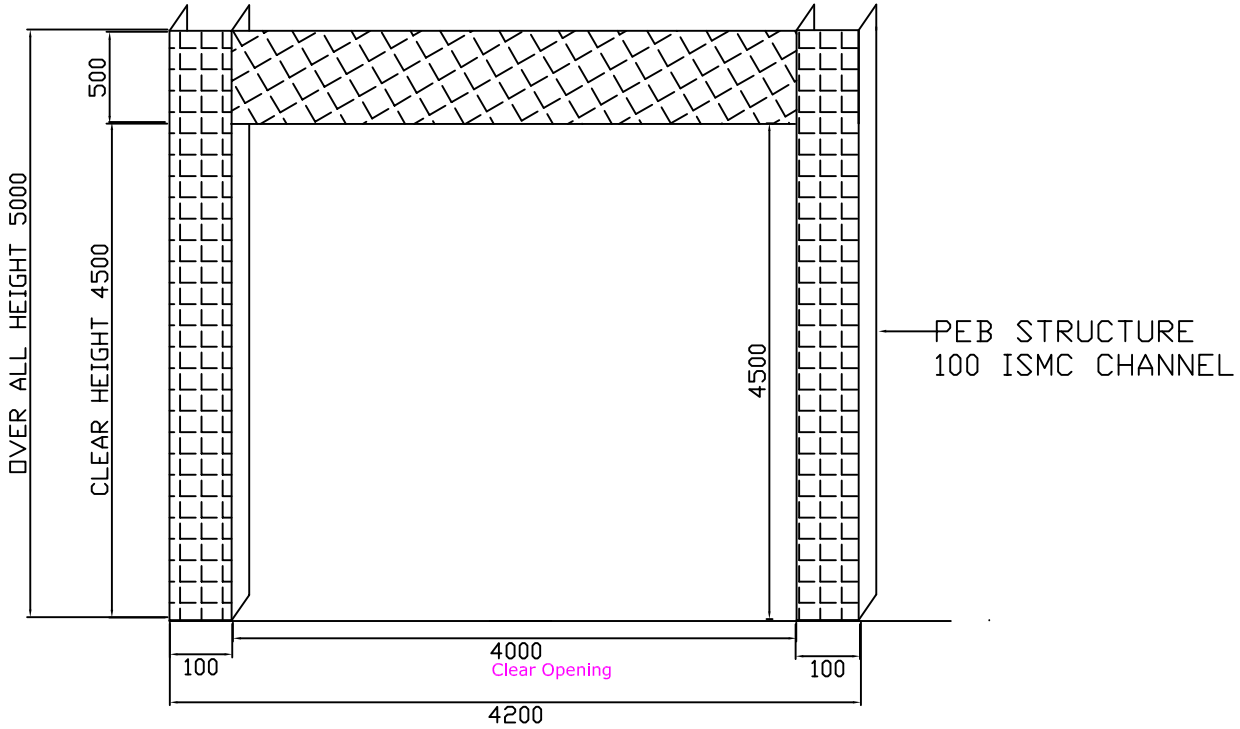

FRONT VIEW

SIZE :- (W)4.0M X (H)4.5M

QTY :- 08 NOS

TITLE: MOUNTING STRUCTURE FOR FIRE RATED ROLLING SHUTTER	DO NOT SCALE DRAWING		NIHVA TECHNOLOGIES PVT. LTD. Pune-411044 Tel : 020 66304033 , Email:-info@nihva.com
		SIGN / DATE	
CLIENTS APPROVEL:–	DRAWN	ANIL	
	CHECK		CLIENT:
	ENG		PROJECT / SITE:
	APPRD.		PRODUCT NAME:
ALL DIMENSION ARE IN M.M.	PROD		
If any querles CONTACT: projects@nlhva.com	MFG		DWG. NO.:–
	Ref. No.		SCALE: NTS SHEET: 1 OF 1