

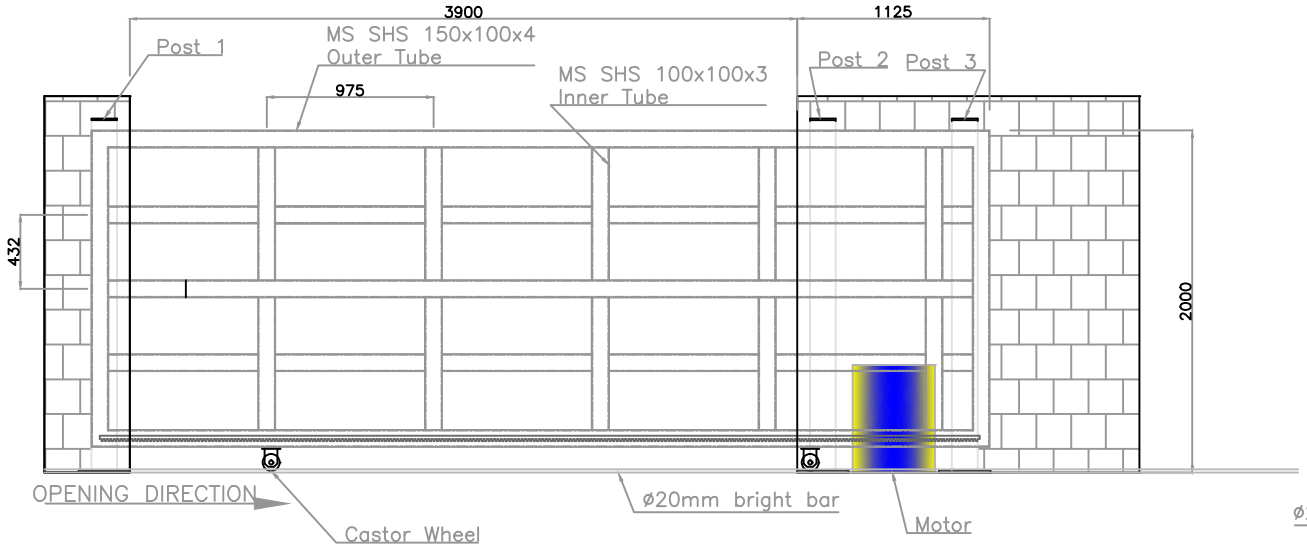


ELEVATION VIEW

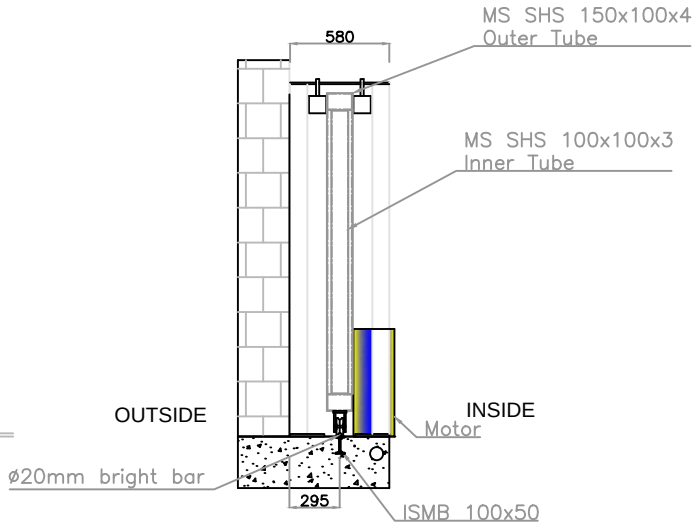

SIDE VIEW

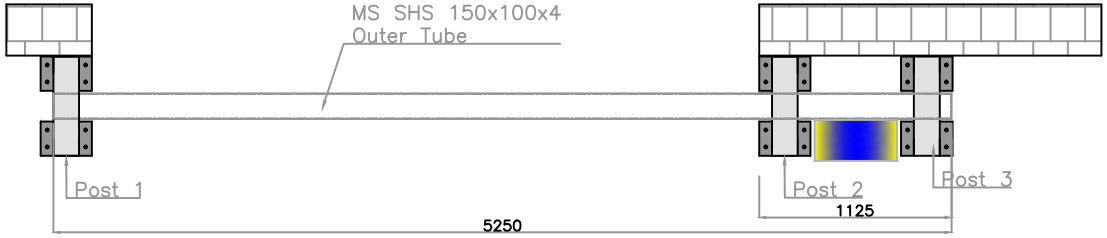

PLAN

Technical Specs of Motorized Sliding Gate

1. Opening length - 3900mm
2. Gate Height - 2000mm
3. Parking length required - 5250mm
4. Outer tube size - MS SHS 150x100x4mm
5. Inner tube size - MS SHS 100x100x3mm
6. Bottom Rail - Bright bar Ø20mm
7. Post size - MS SHS 150x100x4mm
8. Total leaf weight ≈ kg
9. Safety feature - Photocell and flashing light
10. Operation - Push button from side

Note-

1. All dimension are in mm.
2. All civil work is under client scope.
3. 3" PVC pipe in the foundation to be provided by client.
4. Power supply single phase 230v, 50hz.
5. Cable for power supply 2.5 sqmm 3 core
6. Cable for photocell - 1.5 sqmm 4 core

This drawing & design is the property of NIHVA TECHNOLOGIES. Not to be sold or copied to any other concern.

TITLE
SLIDING GATE

	NAME	SIGN	DATE
DRAWN	G.P.		10.08.21
CHECK	A.K.		10.08.21
APPRD.	V.T.		10.08.21


If any queries contact : design@nihva.com

ALL DIMENSION ARE IN mm


NIHVA
NIHVA TECHNOLOGIES PVT. LTD.

NIHVA TECHNOLOGIES
PVT. LTD. PUNE
Tel : 020 66304033
Email:- info@nihva.com
Website:- www.nihva.com

CLIENT -HAIMAVATHY PROPERTIES PVT. LTD.
LOCATION - MUMBAI
PRODUCT - SLIDING GATE 3900 X 2000
NIHVA\20-21\0192 REV- 0
SCALE: NTS
SHEET: 01 OF 02

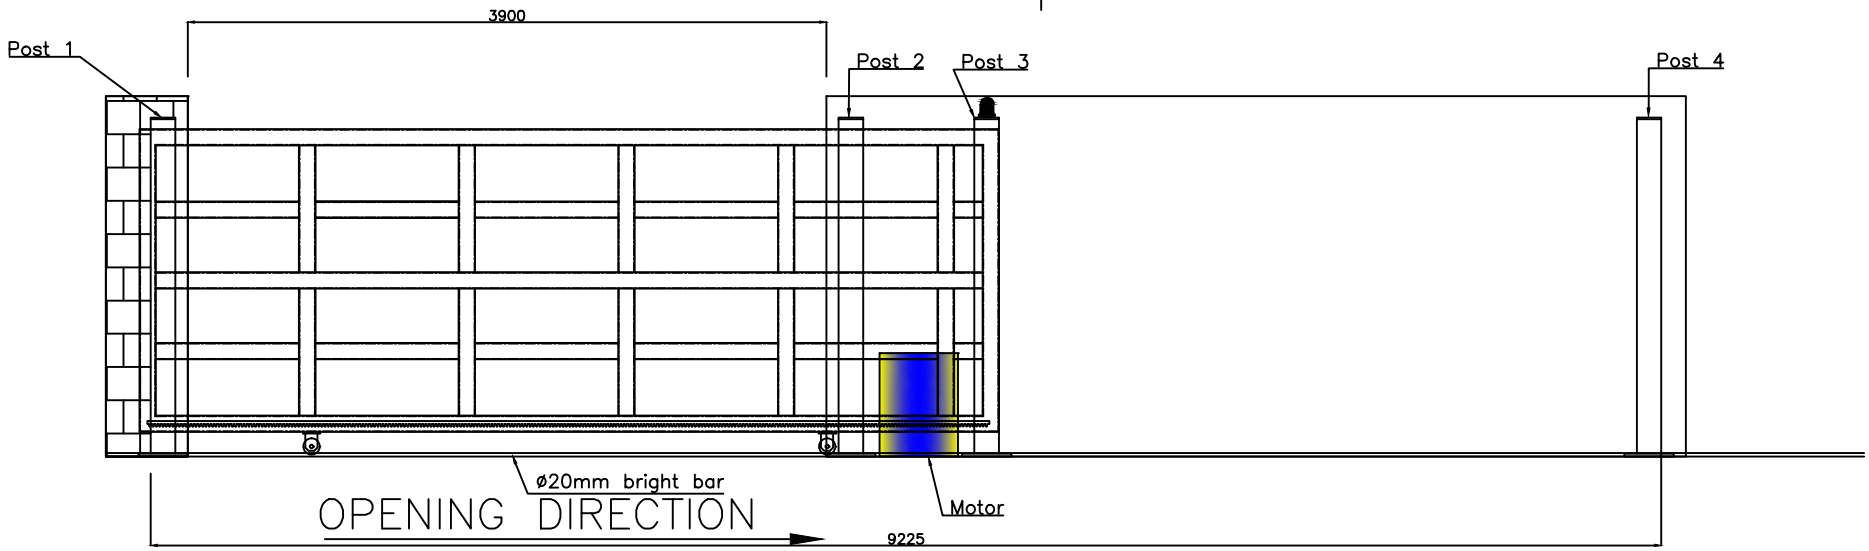

CLOSED GATE ELEVATION

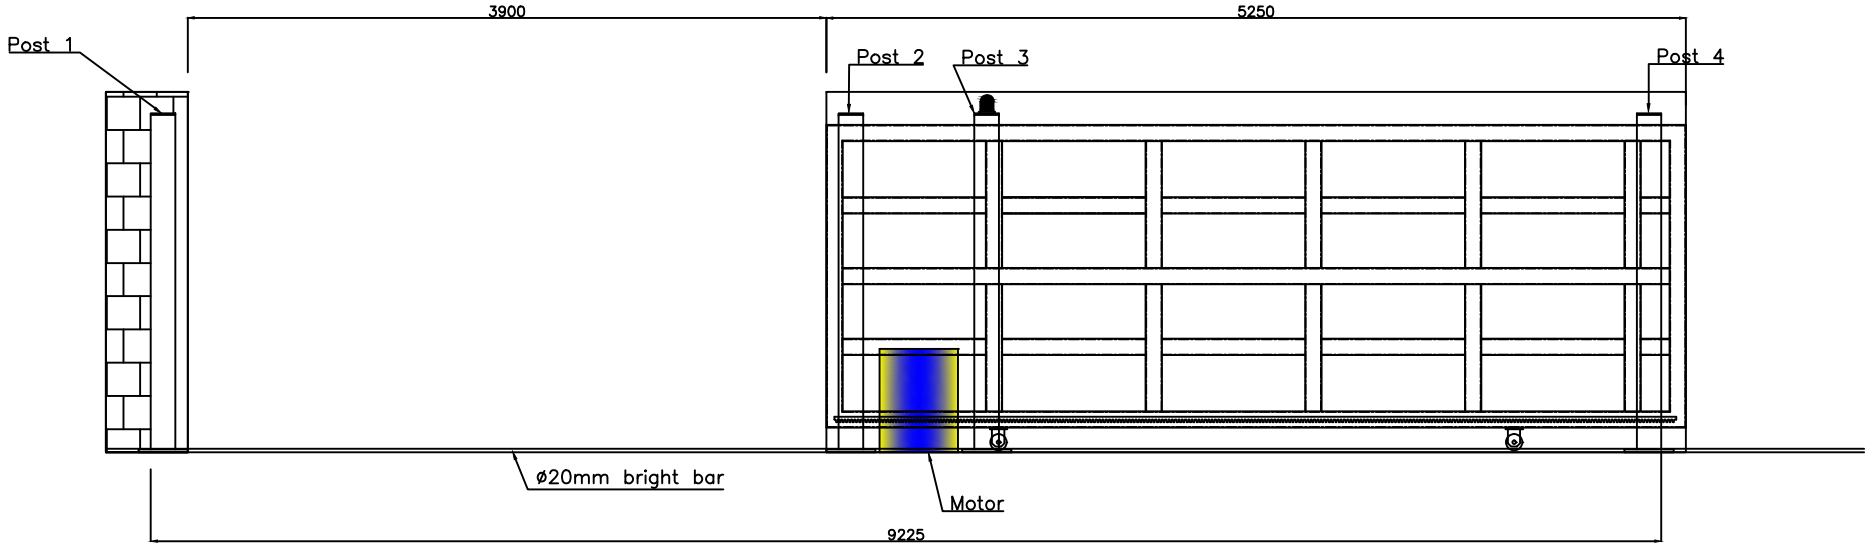

STACKED GATE ELEVATION

This drawing & design is the property of NIHVA TECHNOLOGIES. Not to be sold or copied to any other concern.

TITLE			
SLIDING GATE			
	NAME	SIGN	DATE
DRAWN	G.P.		10.08.21
CHECK	A.K.		10.08.21
APPRD.	V.T.		10.08.21
If any queries contact : design@nihva.com			
ALL DIMENSION ARE IN mm			

NIHVA TECHNOLOGIES PVT. LTD.
NIHVA TECHNOLOGIES PVT. LTD. PUNE
Tel : 020 66304033
Email:- info@nihva.com
Website:- www.nihva.com

CLIENT -HAIMAVATHY PROPERTIES PVT. LTD.	
LOCATION - MUMBAI	
PRODUCT - SLIDING GATE 3500 X 2000	
NIHVA\20-21\0192	REV- 0
SCALE: NTS	SHEET: 02 OF 02