# ENCLOSED PLAN

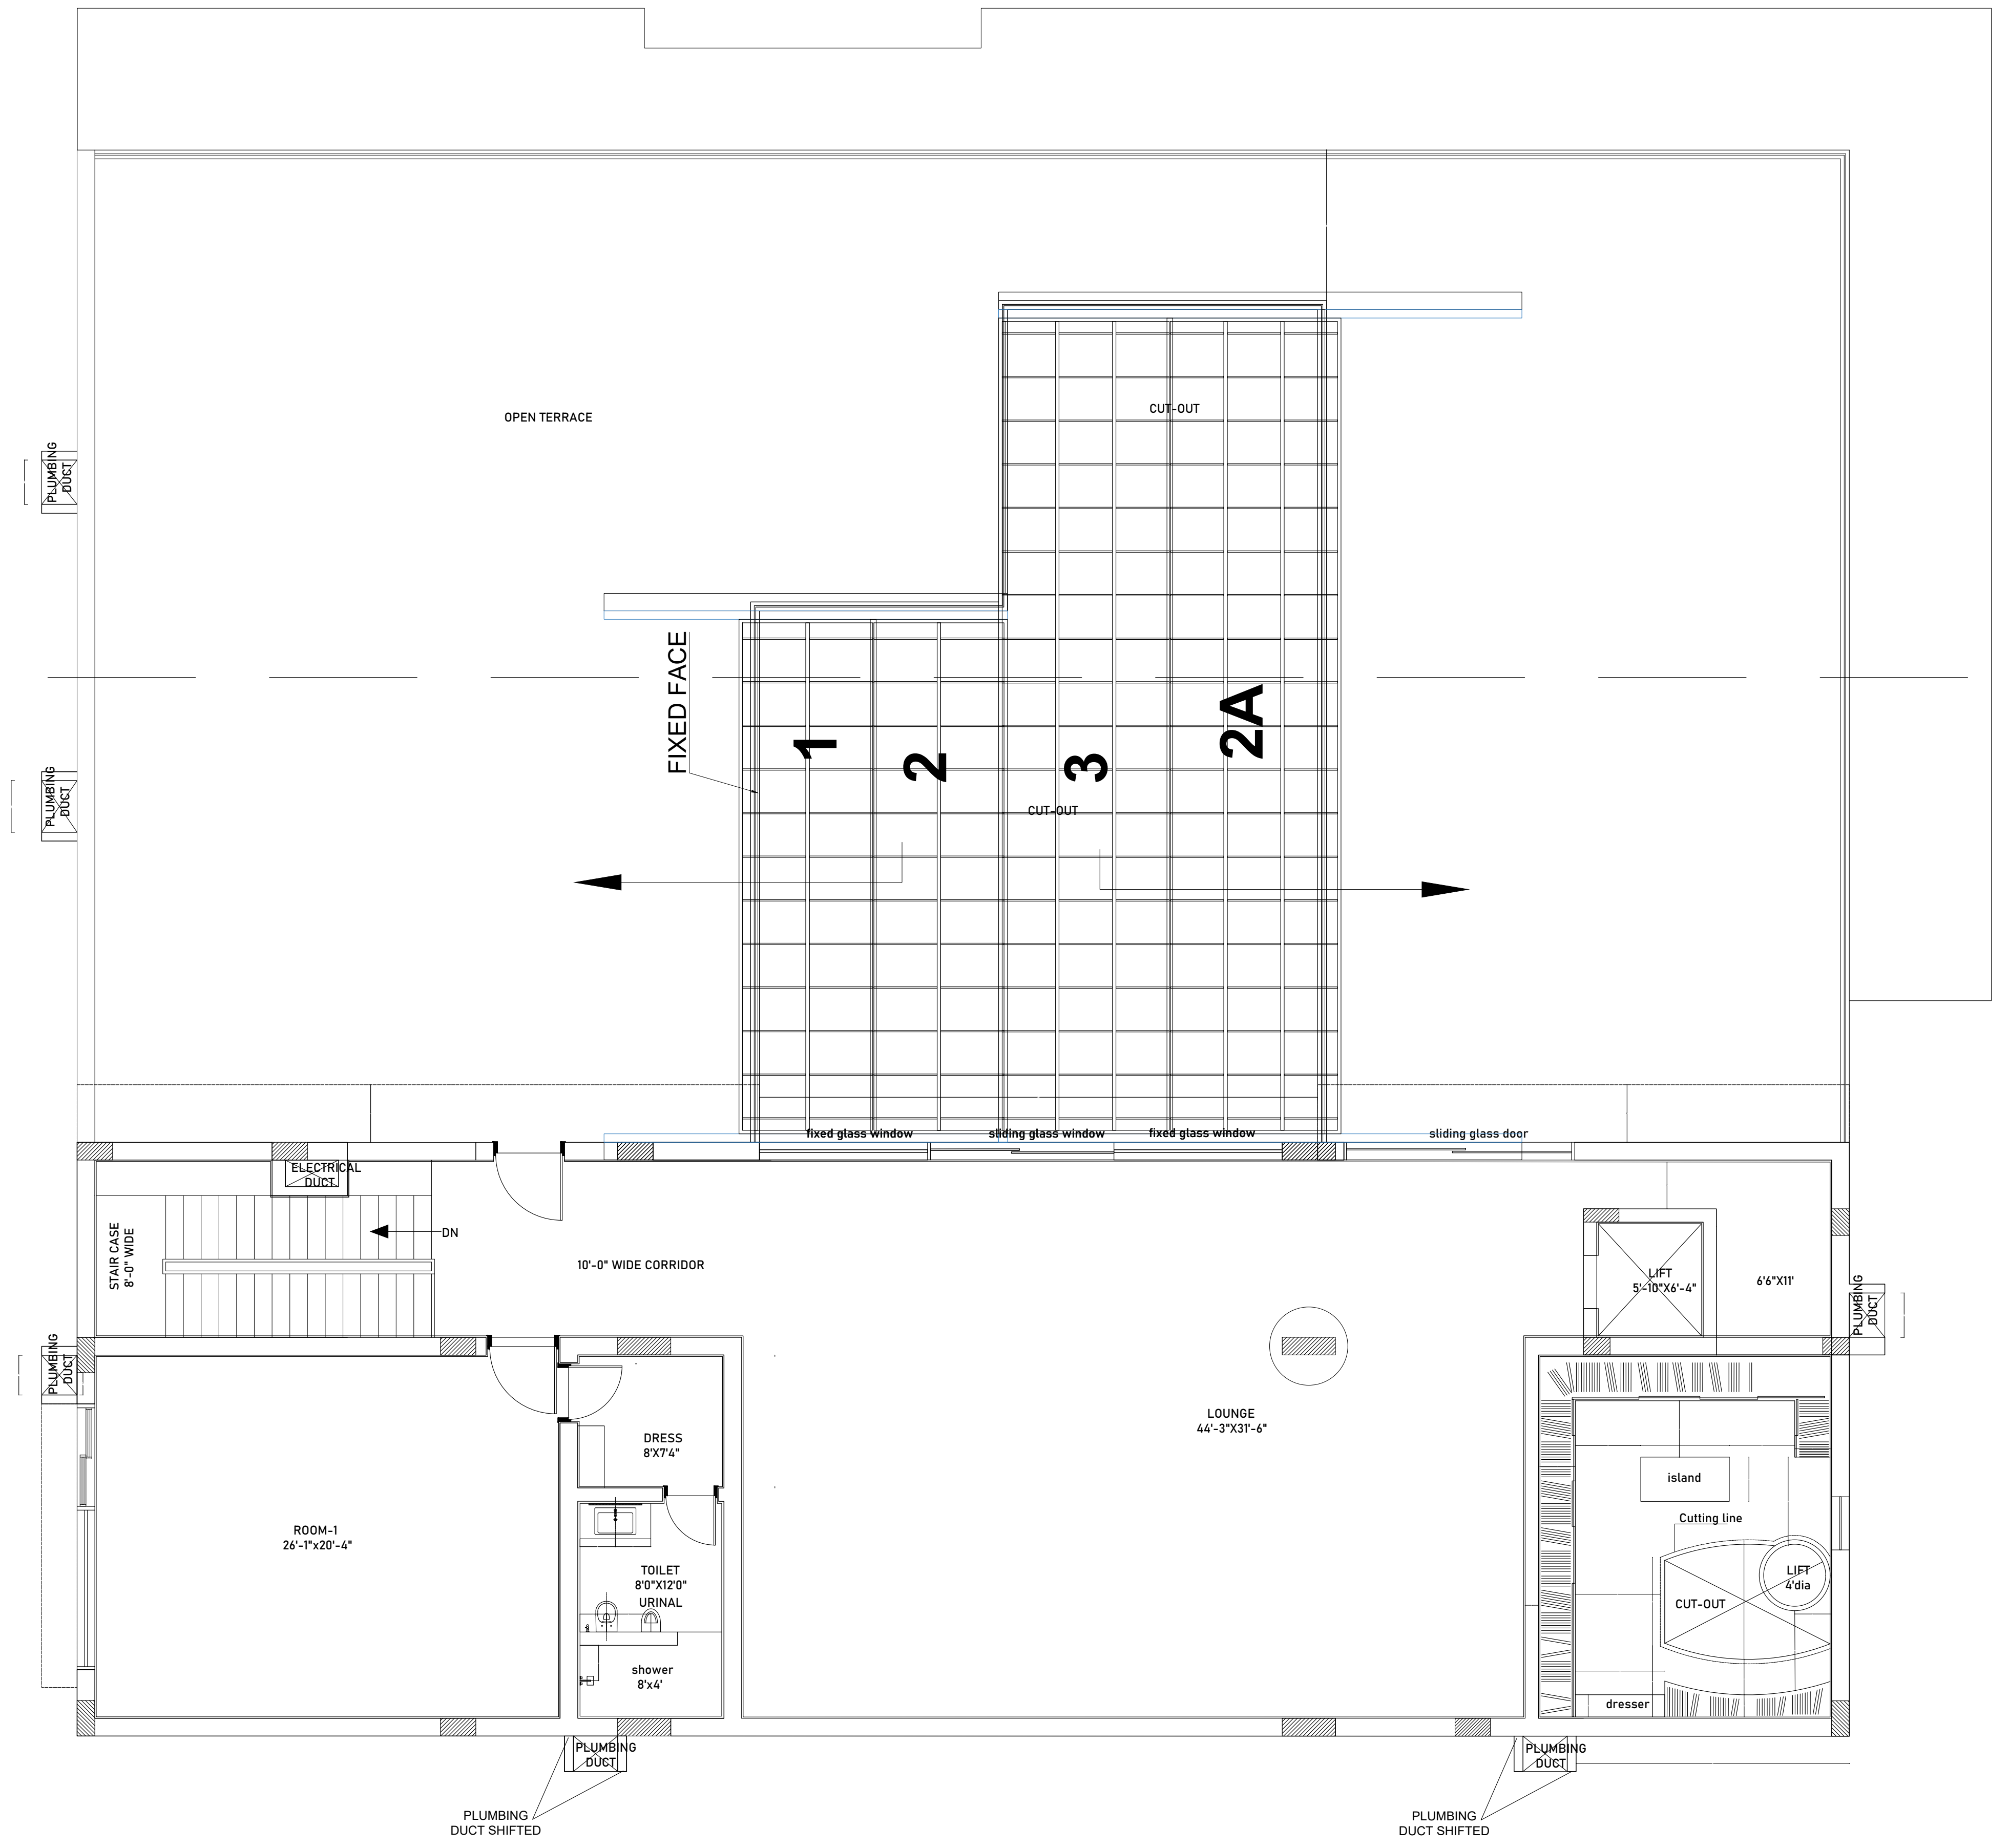

SECOND FLOOR PLAN

**NOTE:**

▬ 12" WALLS CONSTRUCTING

▬ 9" WALLS CONSTRUCTING

Second floor flooring area : 2857.75 SFT

PROJECT:
HARISH RESIDENCE

CLIENT NAME:
MR.HARISH

STRUCTURAL CONSULTANTS:
NEEV CONSULTANTS
#102,Amba Nivas, Prashant Nagar, Hyd-8
email : neev.structures@gmail.com
rajtiwari82@gmail.com

HVAC CONSULTANTS:
E SQUARE TECHNICAL CONSULTANTS
Flat no 401 , Trinetra Apts near Rahul Richland
Apts Sirimalle Nagar Colony Hyderguda
Attapur Hyd 48

ELECTRICAL CONSULTING
DPOWER CONSULTING ENGINEERS,
C/o Roxana Properties, 2nd Floor, Moin Court,
AC Guards, Opposite: Maphar Hussain Cavalry Apartments,
Lakdikapool,
Hyderabad.

LIGHTING CONSULTANTS:
LDA
LUMA DESIGN ARTS LIGHTS

PLUMBING CONSULTANTS:
SARATHI CONSULTANTS
P.NO-20-A, AVANTHI NAGAR COLONY(EAST)
BEHIND VIJETHA PUBLIC SCHOOL-
AG GLASS FACTORY ROAD - MOTHI NAGAR
HYDERABAD-500018
M.NO- 09848590135

ARCHITECTS:
SHILPALAYA ASSOCIATES
info@shilpalaya.com
FLAT NO .601 BLOCK C SIRI SIGNATURE
APARTMENTS CYBERHILLS, MADHAPUR,
HYDERABAD-500081
PHONE NO : 040-40200300
EMAIL : shilpalaya@gmail.com

INTERIORS ARCHITECTS & PMC:
New Designer Web Pvt Ltd
Plot no.78, II Floor, Phase 1, Kavuri Hills,
Hyderabad - 500081,
Telangana, India.
Tel: +91- 40 - 23348454 / 23348455
www.designerweb.in

GFC DRAWINGS

DRAWING TITLE:
SECOND FLOOR PLAN
BRICK MARKING PLAN

DRAWN BY: RAJITHA
CHECKED BY: AR. MANOJ WAHI
APPROVED BY : AR. MANOJ WAHI
DRAWN No.

DATE: 04.07.2025
REVISION: 1
SCALE: N.T.S
NORTH

Copyright in these drawings, designs and specifications are the property of SHILPALAYA ASSOCIATES., and must not be used,reproduced or copied, wholly or in part, without the written permission of SHILPALAYA ASSOCIATES. These drawings shall not be changed, altered or amended by party for any purpose other than by SHILPALAYA ASSOCIATES.

---

# STACKED PLAN

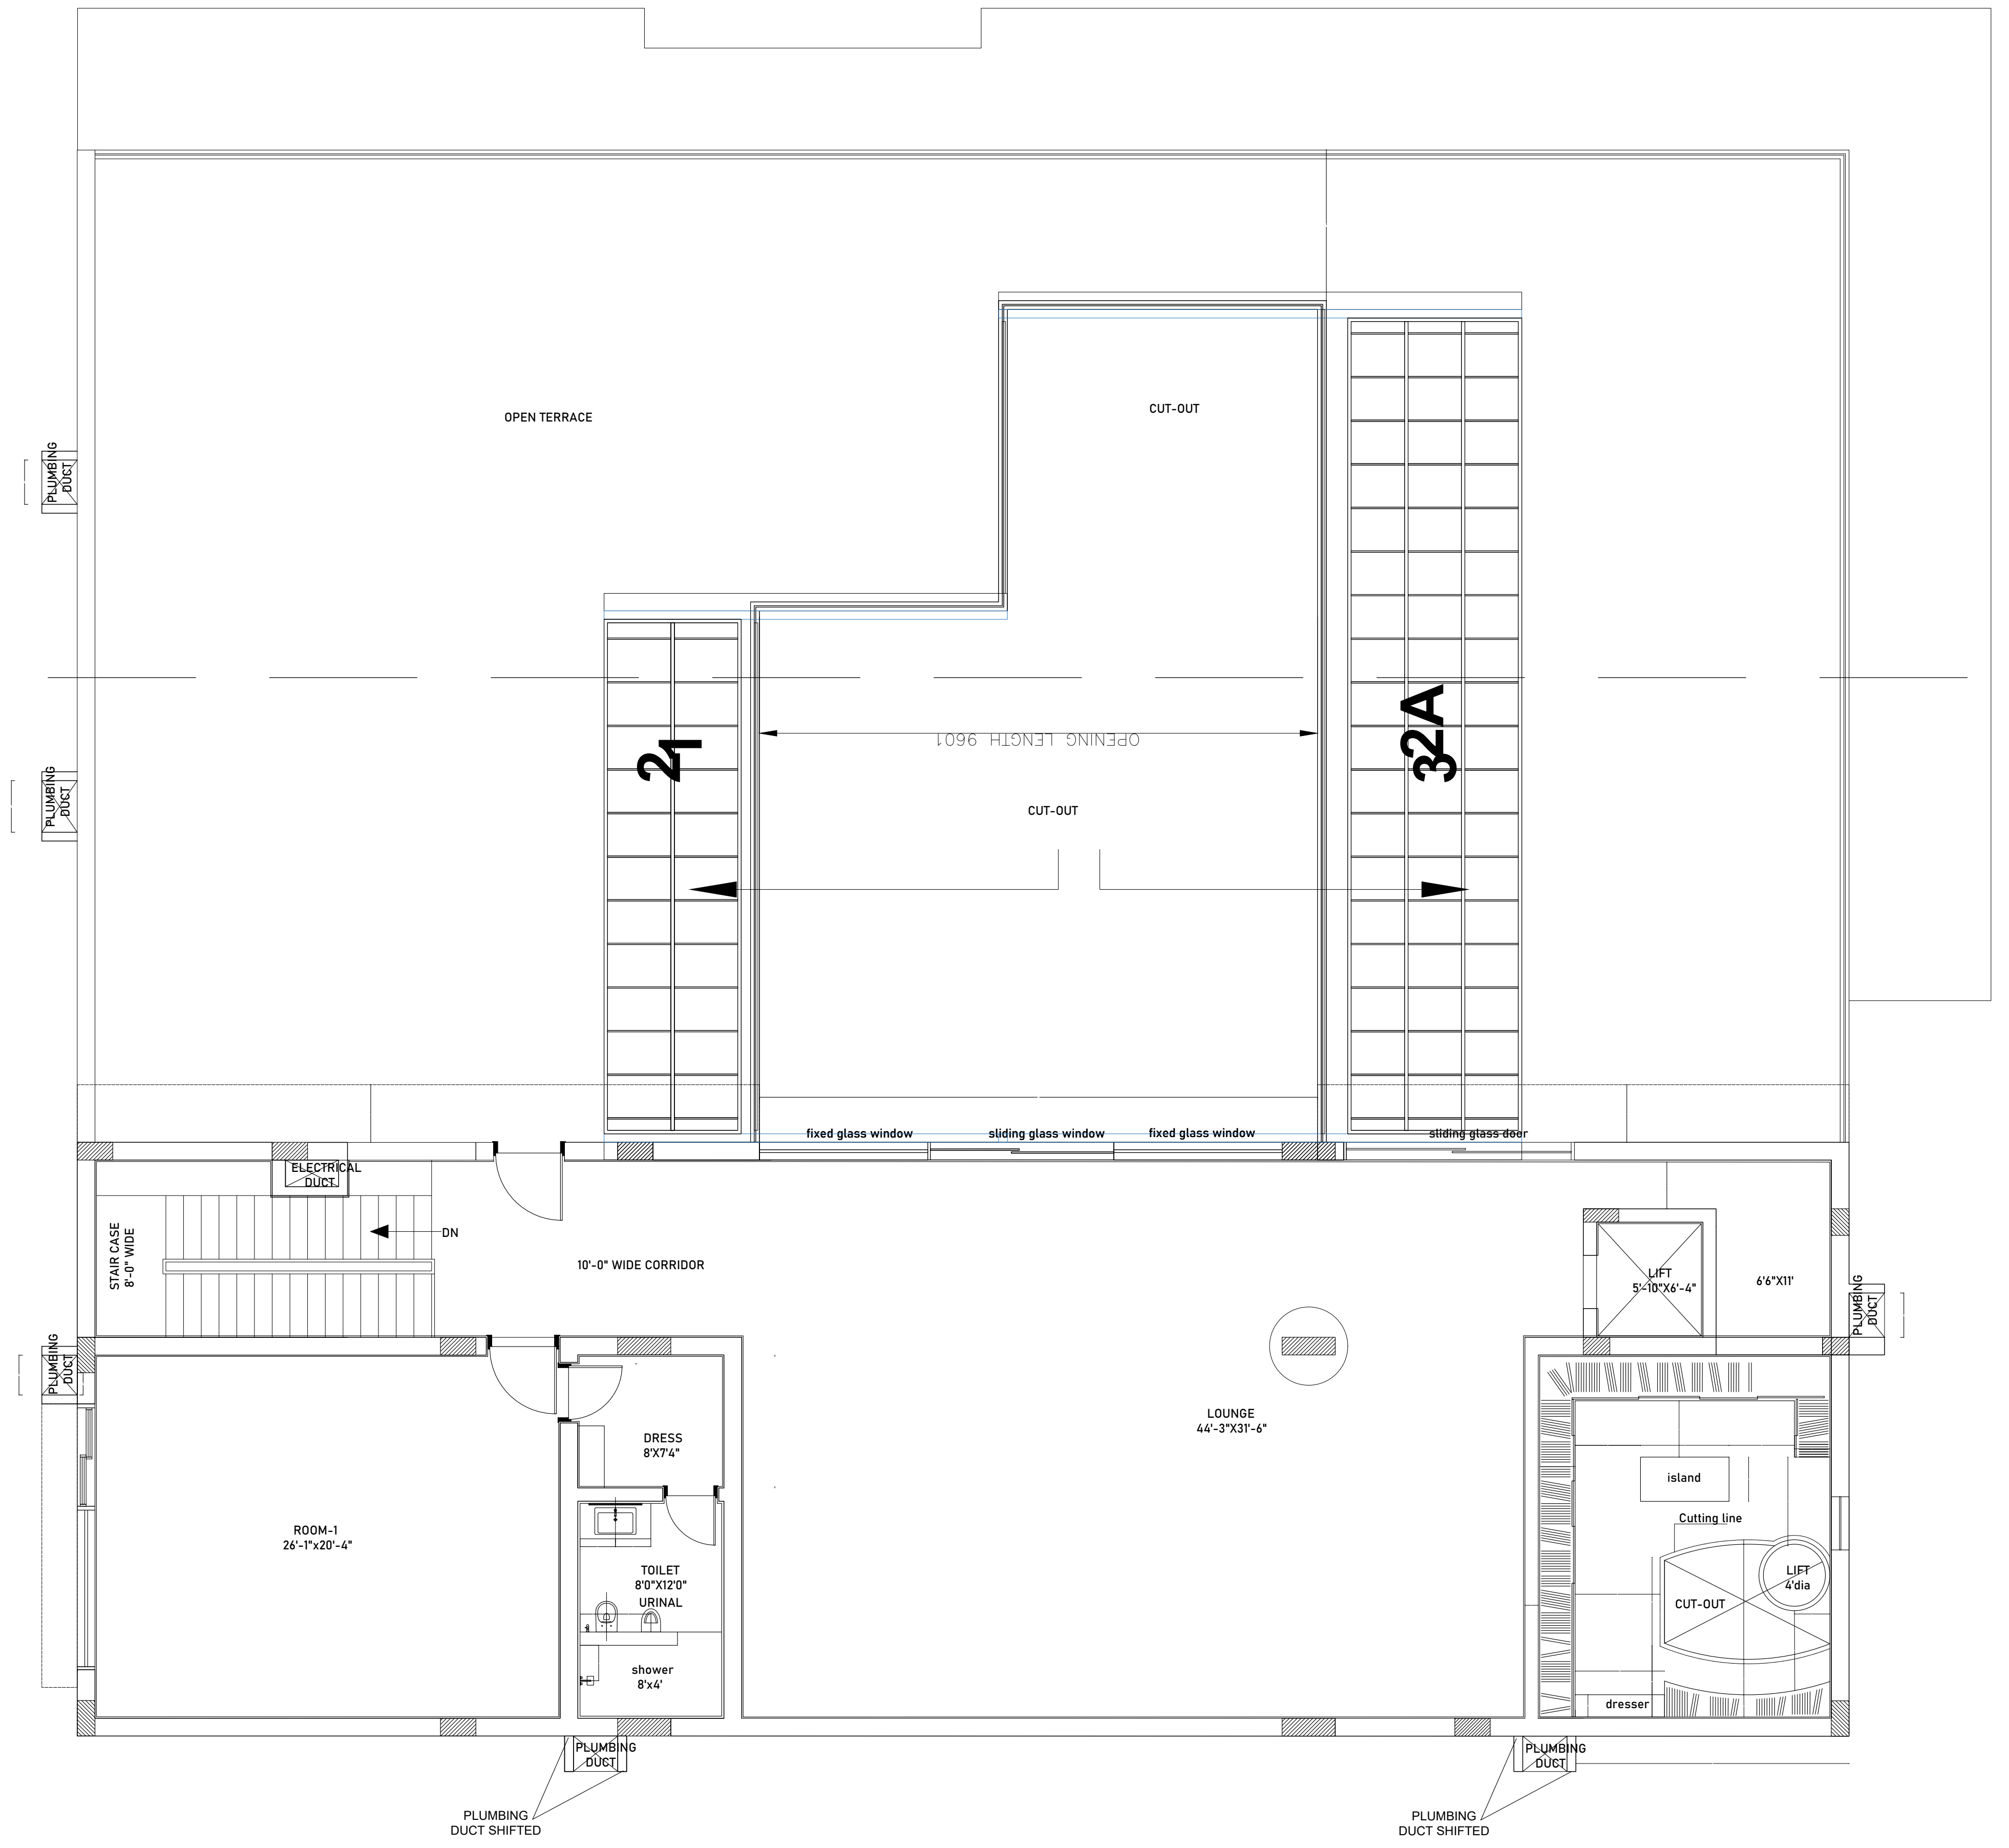

SECOND FLOOR PLAN

**NOTE:**

▬ 12" WALLS CONSTRUCTING

▬ 9" WALLS CONSTRUCTING

Second floor flooring area : 2857.75 SFT

PROJECT:
HARISH RESIDENCE

CLIENT NAME:
MR.HARISH

STRUCTURAL CONSULTANTS:
NEEV CONSULTANTS
#102,Amba Nivas, Prashant Nagar, Hyd-8
email : neev.structures@gmail.com
rajtiwari82@gmail.com

HVAC CONSULTANTS:
E SQUARE TECHNICAL CONSULTANTS
Flat no 401 , Trinetra Apts near Rahul Richland
Apts Sirimalle Nagar Colony Hyderguda
Attapur Hyd 48

ELECTRICAL CONSULTING
DPOWER CONSULTING ENGINEERS,
C/o Roxana Properties, 2nd Floor, Moin Court,
AC Guards, Opposite: Maphar Hussain Cavalry Apartments,
Lakdikapool,
Hyderabad.

LIGHTING CONSULTANTS:
LDA
LUMA DESIGN ARTS LIGHTS

PLUMBING CONSULTANTS:
SARATHI CONSULTANTS
P.NO-20-A, AVANTHI NAGAR COLONY(EAST)
BEHIND VIJETHA PUBLIC SCHOOL-
AG GLASS FACTORY ROAD - MOTHI NAGAR
HYDERABAD-500018
M.NO- 09848590135

ARCHITECTS:
SHILPALAYA ASSOCIATES
info@shilpalaya.com
FLAT NO .601 BLOCK C SIRI SIGNATURE
APARTMENTS CYBERHILLS, MADHAPUR,
HYDERABAD-500081
PHONE NO : 040-40200300
EMAIL : shilpalaya@gmail.com

INTERIORS ARCHITECTS & PMC:
New Designer Web Pvt Ltd
Plot no.78, II Floor, Phase 1, Kavuri Hills,
Hyderabad - 500081,
Telangana, India.
Tel: +91- 40 - 23348454 / 23348455
www.designerweb.in

GFC DRAWINGS

DRAWING TITLE:
SECOND FLOOR PLAN
BRICK MARKING PLAN

DRAWN BY: RAJITHA
CHECKED BY: AR. MANOJ WAHI
APPROVED BY : AR. MANOJ WAHI
DRAWN No.

DATE: 04.07.2025
REVISION: 1
SCALE: N.T.S
NORTH

Copyright in these drawings, designs and specifications are the property of SHILPALAYA ASSOCIATES., and must not be used,reproduced or copied, wholly or in part, without the written permission of SHILPALAYA ASSOCIATES. These drawings shall not be changed, altered or amended by party for any purpose other than by SHILPALAYA ASSOCIATES.