




COMPOUND WALL FRONT ELEVATION

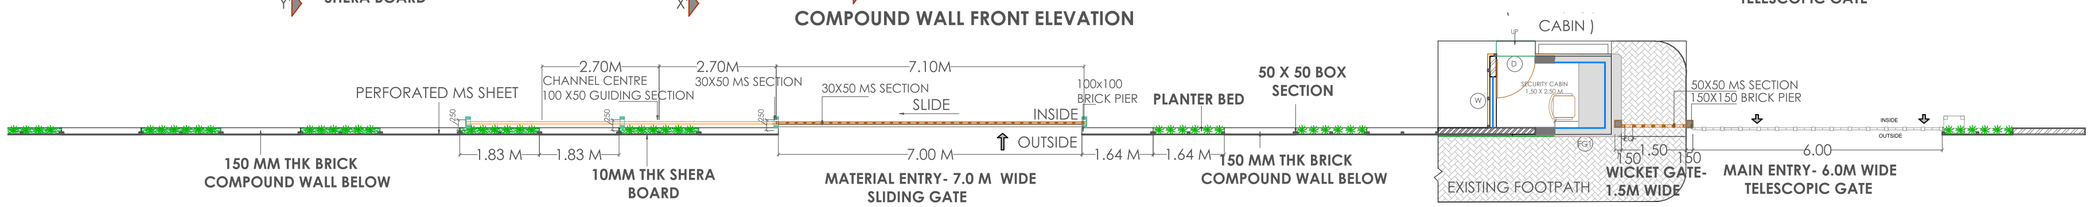


DETAIL PLAN OF SLIDING GATE (SCALE- 1:100)

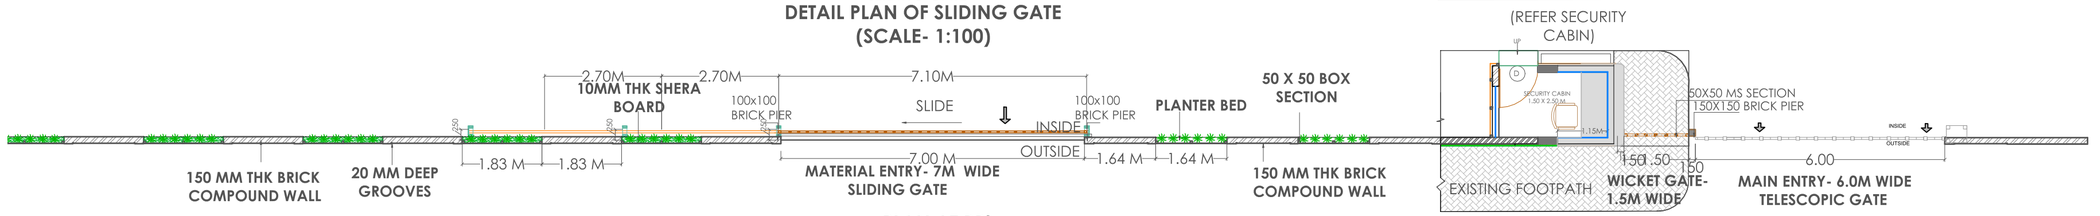


PLAN AT BB' (SCALE- 1:100)

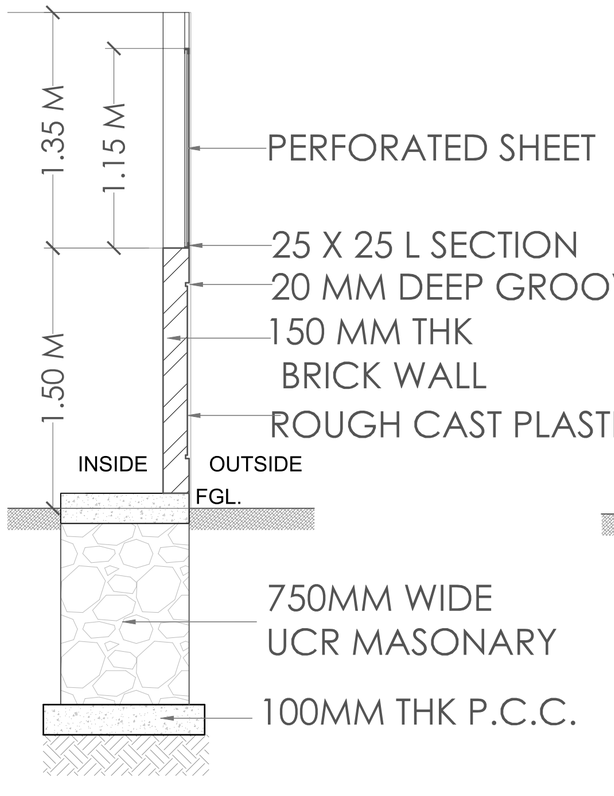

SECTION YY' (SCALE- 1:25)

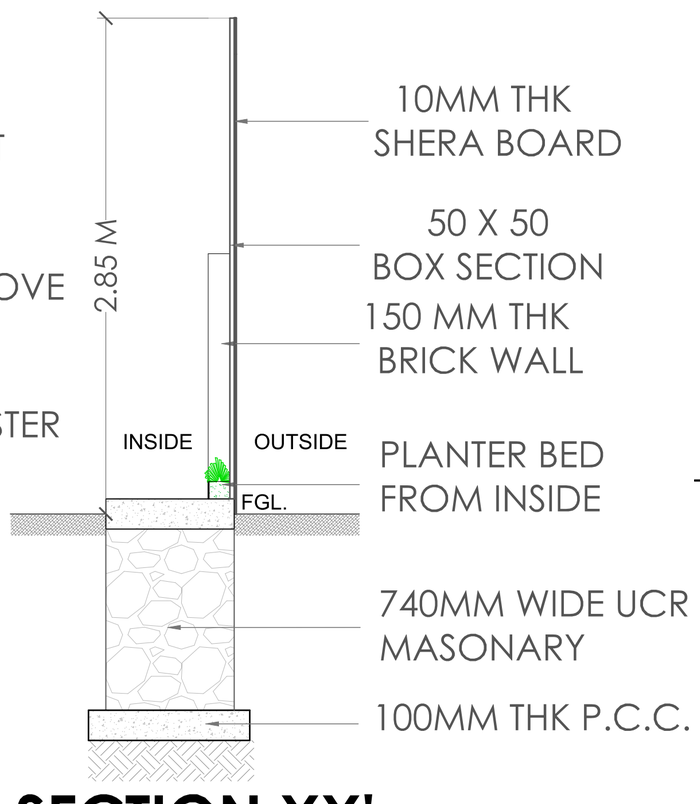


SECTION XX' (SCALE- 1:25)

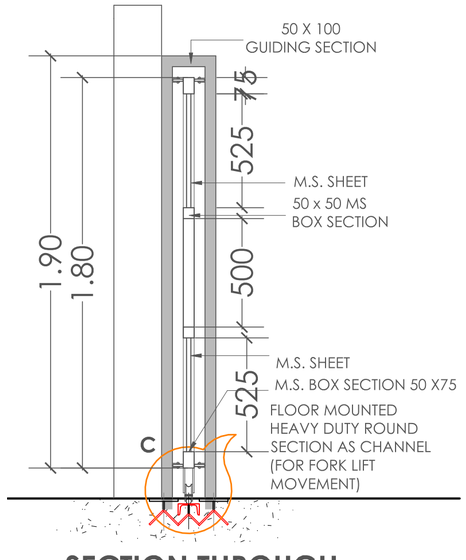

SECTION THROUGH SLIDING GATE SECTION ZZ

SCALE 1:20

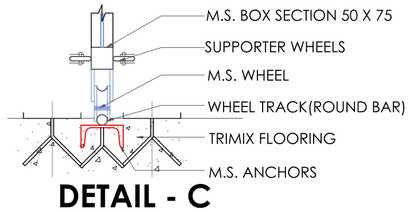

DETAIL - C (SCALE 1:10)

SHEET NO - 09

PATH- \\192.9.200.225\Design\PDA Design\Project\Indus - Tc Architectural\04 Working\02 WORKING DETAILS\Comp FINAL.dwg

NOTE :- EXISTING FRONT COMPO WALL TO BE DEMOLISHED.

REVISION NO.

NO.	DATE	DESCRIPTION

*** NOTES:
1. PLEASE DO NOT SCALE THE DRAWING. FOLLOW W DIMENSIONS.
2. ALL DIMENSIONS GIVEN ARE IN MILLIMETERS
3. IN CASE OF CONTROVERSIES CONTACT THE ARCH IMMEDIATELY.
4. FOR STRUCTURAL DETAILS PLEASE REFER R.C.C. DW
5. DO NOT REFER PREVIOUS DWG
6. REFER STRUCTURAL DRAWING ALONG WITH THIS DRAWING.

SIGN / SEAL -

PRASHANT DESHMUKH & ASSOCIATI
ARCHITECTURAL & ENGINEERING CONSULTA

FRONT COMPOUND WALL & ENTRANCE GATE DETAIL

PRASHANT DESHMUKH AND ASSOCIA
ARCHITECTURAL & ENGINEERING CONSULTAN
1/62-B, PADMADARSHAN SOC.,
PUNE - SATARA ROAD, PUNE - 411 009.
TELEFAX :- 2422 78 96 32907142 24218714

CLIENT	INDUS ENGINEERS PVT LTD.,TALOJA.		
PROJECT	PROPOSED PRODUCTION AREA (SHOP FLOOR) NAVI MUMBAI.		
SCALE	DATE	DEALT BY	DWG No
AM	31.01.2022	CHAITRALI	PDA/829/AR/WD/SD/COMPO WALL DETAIL/06
CHK BY		IRA	