

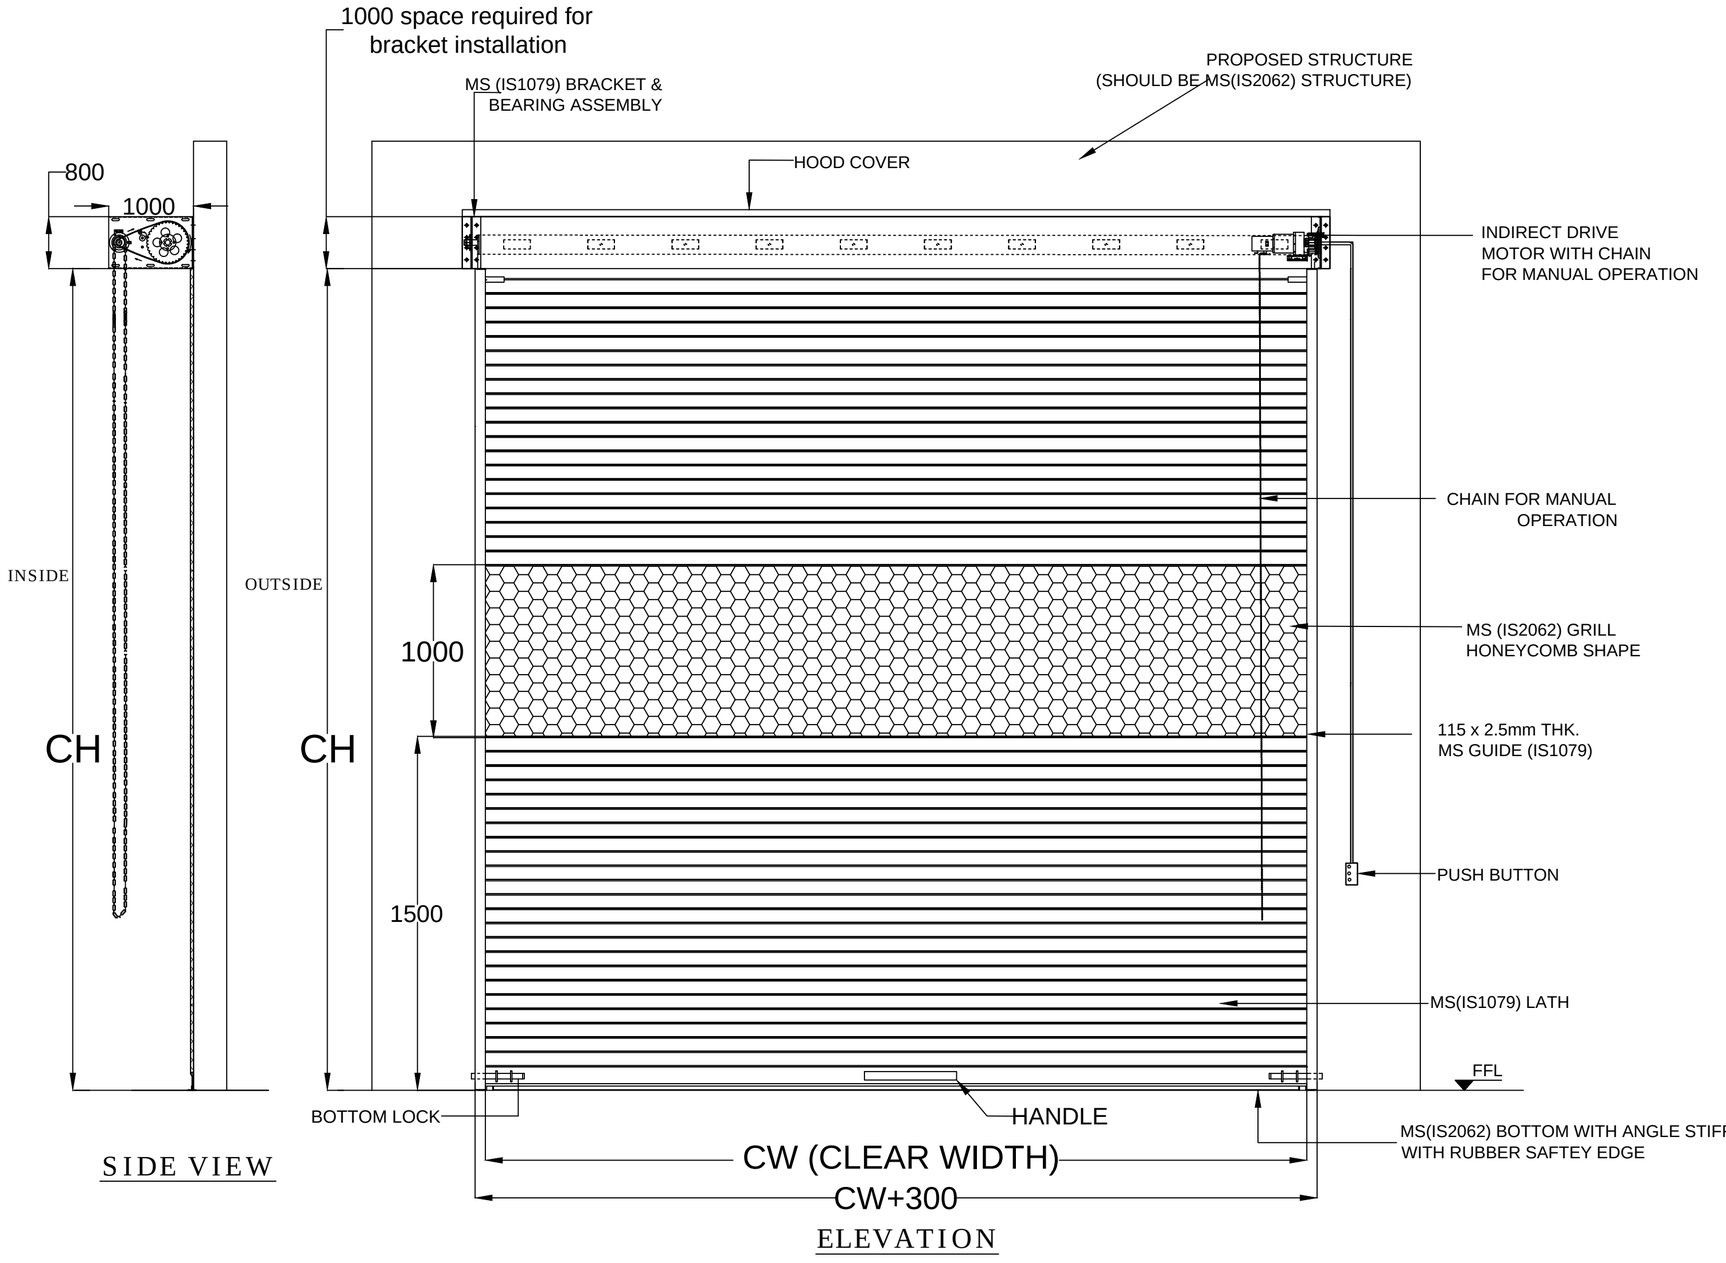


SIDE VIEW

ELEVATION

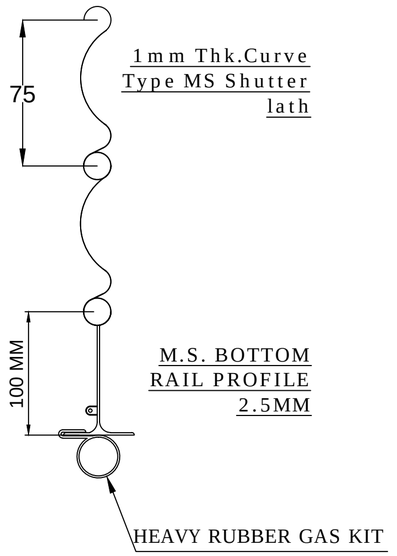


M.S. BOTTOM RAIL PROFILE 2.5MM

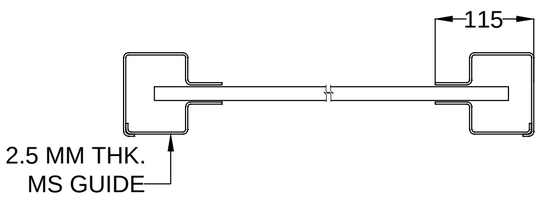

COLOR:- 1.RAL7035(LIGHT GRAY)
2.RAL9016(TRAFFIC WHITE)
3.RAL5005(SIGNAL BLUE)
4.RAL7004(SIGNAL GRAY)
5.RAL5015(SKY BLUE)

CLEAR WIDTH (CW)	CLEAR HEIGHT (CH)	GRILL SIZE (CW) X (CH)	QUANTITY
7000	7000	7000 X 1000	04

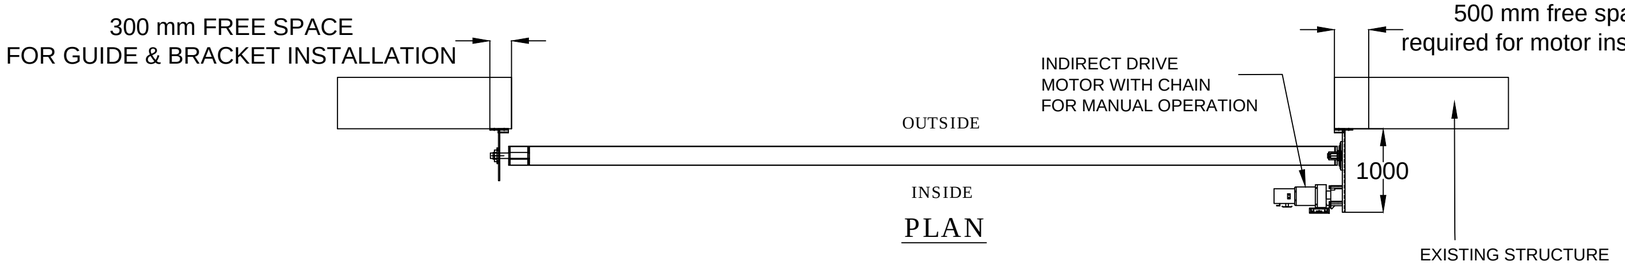

PLAN

Rev 01:- 04/02/2022
1.Added IS material specification for MS material.
2.Added motor capacity details.
3.Mentioned height of grill.
4.Mentioned RAL code.

NOTE:-
1.REQUIRED STRUCTURE FOR ROLLING SHUTTER SHALL BE IN NIHVA SCOPE.
2. ALL REQUIRED CIVIL WORK IN CLIENT SCOPE.
3. 3 PHASE POWER SUPPLY SHOULD BE PROVIDED BY CLIENT.
4. MOTOR : JIELONG , 1.5 TON, 3PH

This drawing & designing is the property of NIHVA TECHNOLOGIES. Not to be sold or copied to any other concern.

TITLE: MOTORIZED ROLLING SHUTTER

NIHVA TECHNOLOGIES PVT. LTD. PUNE
Tel : 020 66304033
Email:- info@nihva.com
Website:- www.nihva.com

	NAME	SIGN	DATE
DRAWN	G.P.		13/09/21
CHECK	A.K.		13/09/21
APPROVAL	V.T.		13/09/21

CLIENT -REWARD CONSTRUCTION
PROJECT -
SITE - INDAPUR
If any queries contact : design@nihva.com
DWG. NO. : NIHVA/21-22/0231
REV. - 01
ALL DIMENSION ARE IN mm
SCALE: NTS
WT:
SHEET: 01 OF 01