

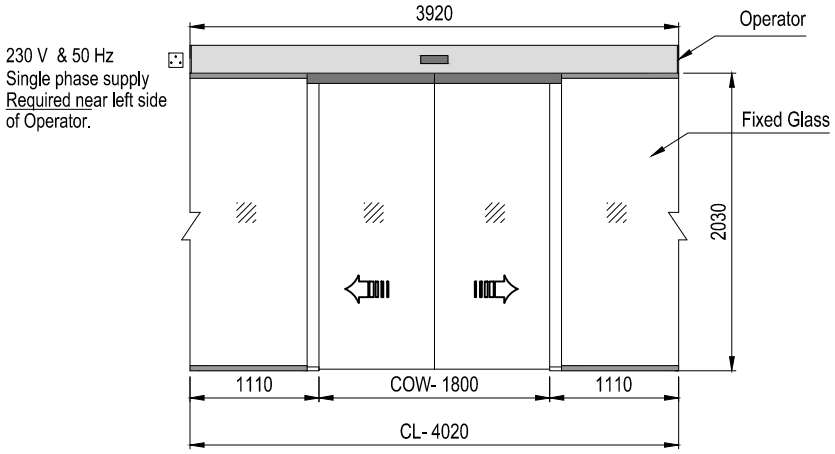


Inside Elevation

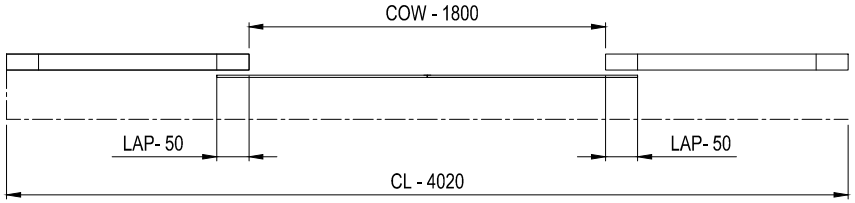


Closed Condition

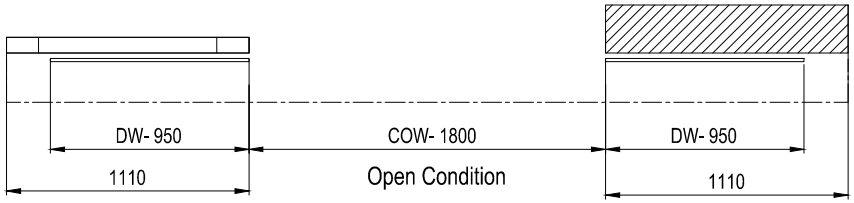

Open Condition

Plan

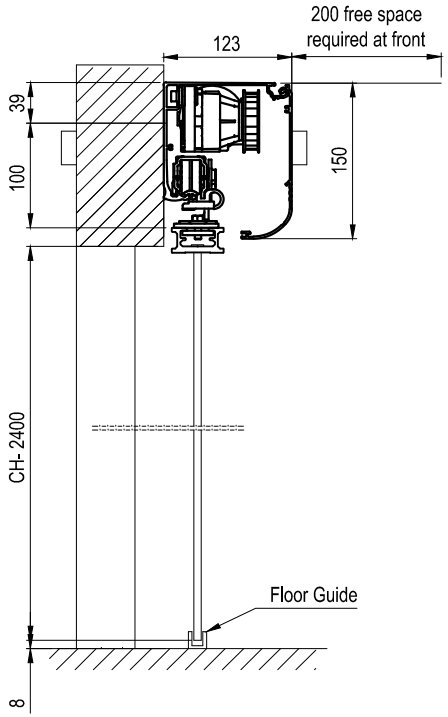

Door Size			
Sr. No.	Clear Width	Clear Height	Quantity
1	1800	2400	1

Glass Type- 10mm Toughened
1. TWO FIXED.
2. TWO MOVING.

This drawing & designing is the property of NIHVA TECHNOLOGIES. Not to be sold or copied to any other concern.

TITLE	AUTOMATIC SLIDING GLASS DOOR			NIHVA TECHNOLOGIES PVT. LTD.
	DRAWN	SIGN	DATE	
DRAWN	P.A		12.01.18	CLIENT - SCON
CHECK	V.T		12.01.18	PROJECT - CREATIVE TOOLS
				SITE -
APPROVAL				DWG. NO. : NIHVA/18-19/0232
If any queries contact : projects@nihva.com				SCALE: NTS | WT: | SHEET: 01 OF 01
ALL DIMENSION ARE IN mm				

NIHVA TECHNOLOGIES PVT. LTD. PUNE
Tel : 020 66304033
Email:- info@nihva.com
Website:- www.nihva.com