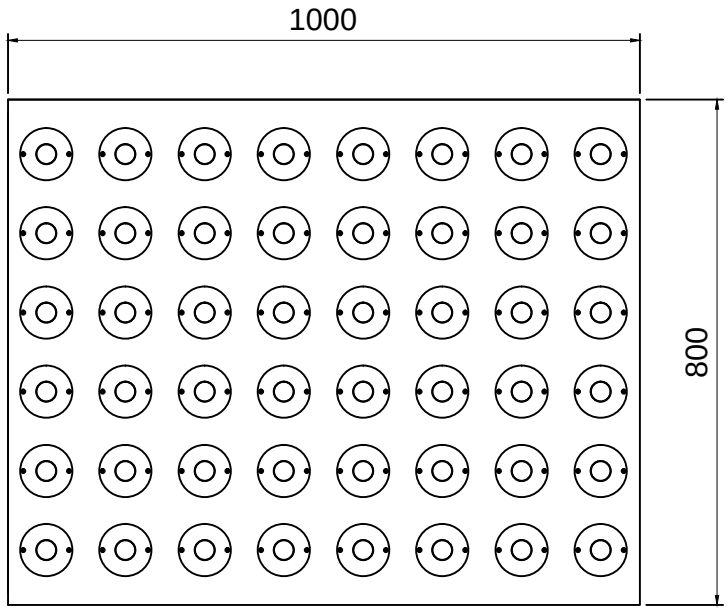

PLAN VIEW

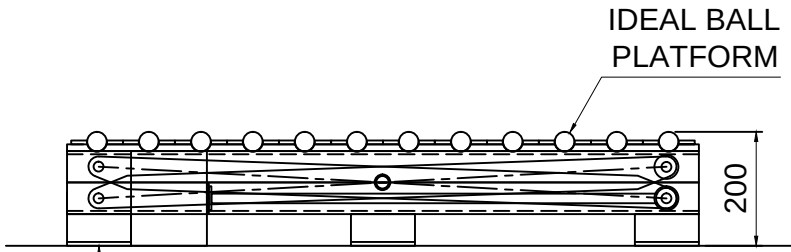

CLOSED POSITION

TO BE GROUTED
AT FFL

FFL

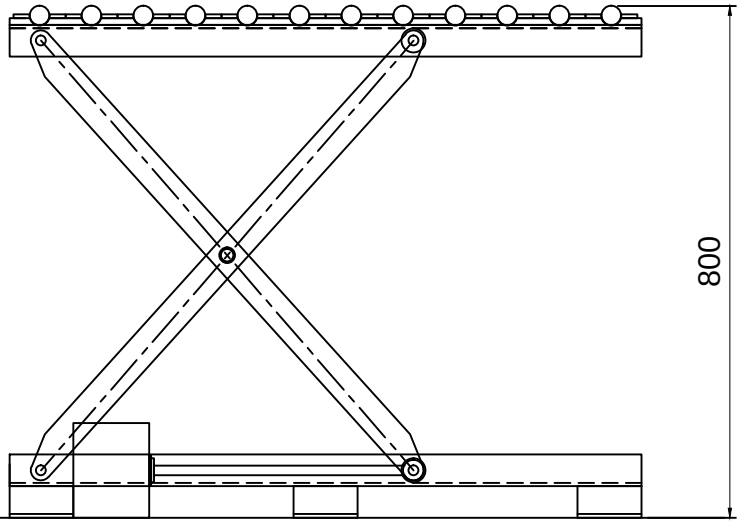

OPEN POSITION

M.O.C : SS304
(EXCLUDING DRIVE)

This drawing & design is the property of NIHVA TECHNOLOGIES. Not to be sold or copied to any other concern.

TITLE	SEMI ELECTRIC SCISSOR LIFT		
	NAME	SIGN	DATE
DRAWN	P.A		03.08.2020
CHECK	G.J		03.08.2020
APPRD.			
If any queries contact : design@nihva.com			
ALL DIMENSION ARE IN mm			

NIHVA TECHNOLOGIES PVT. LTD.
NIHVA TECHNOLOGIES PVT. LTD. PUNE
Tel : 020 66304033
Email:- info@nihva.com
Website:- www.nihva.com

CLIENT - INFINITY AUTOMATED SOLUTION			
PROJECT -			
SITE LOCATION - PUNE			
DWG. NO. : NIHVA/20-21/0040			
SCALE: NTS	WT:	REV- 00	