

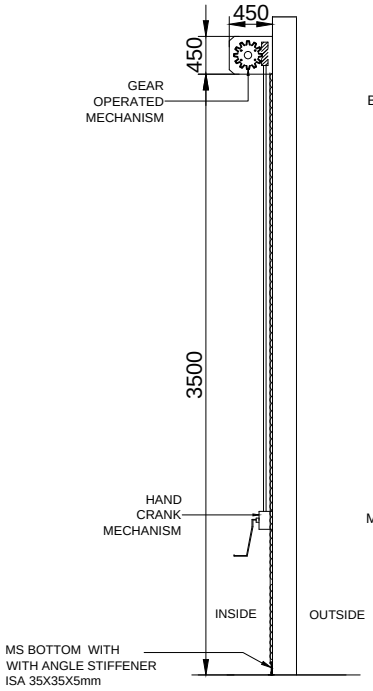



SIDE VIEW

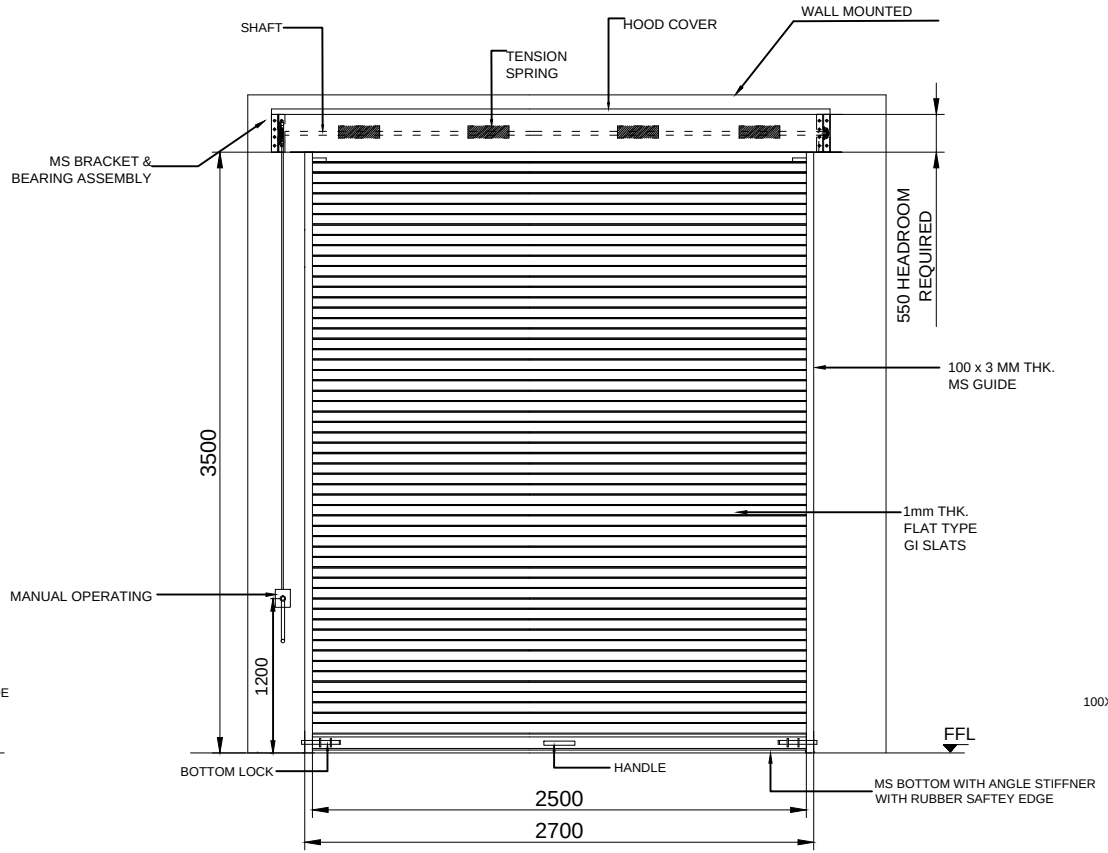


INSIDE ELEVATION

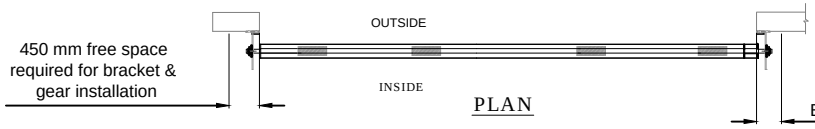

PLAN

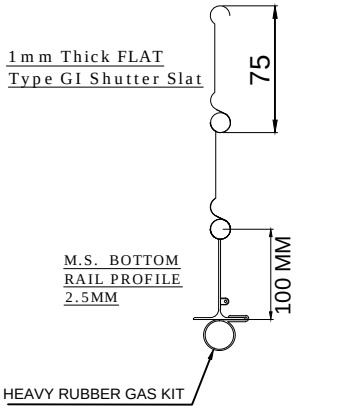

M.S. BOTTOM RAIL PROFILE 2.5MM

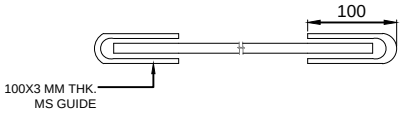

RAL COLOR
RAL 9002 (WHITE GREY)

S.NO	FEATURE	EQUIPMENT DETAILS
01	SLATS MODEL	GALVANISE STEEL(GI) SLATS 1mm THK.
02	GUIDE RAIL	100 X 3mm THK MILD STEEL(MS).
03	BOTTOM RAIL	2.5mm THK MILD STEEL (M.S.).
04	HOOD COVER	0.9mm THK GALVANISE STEEL (GI).
05	RAL COLOR	RAL 9002 (WHITE GREY)
06	NO OF SLATS	60 NOS

SR.NO.	SIZE	QUANTITY
01	2500(W)X3500(H)	10

NOTE-
1. ALL CIVIL WORK WILL BE CLIENT'S SCOPE.
2.FINAL FINISH OF SHUTTER WILL BE IN POWDER COATING OF APPROVED COLOR.
3.DESIGN OF SHUTTER IS AS PER I.S. 6248:1979 STANDARDS.

TOLERANCE - ±10mm

This drawing & design is the property of NIHVA TECHNOLOGIES. Not to be sold or copied to any other concern.

TITLE
GEAR OPERATED ROLLING SHUTTER 2.5mX3.5m(FLAT PROFILE)

NIHVA TECHNOLOGIES PVT. LTD.

NIHVA TECHNOLOGIES PVT. LTD. PUNE
Tel : 020 66304033
Email:- info@nihva.com
Website:- www.nihva.com

	NAME	SIGN	DATE
DRAWN	P.A		16.01.19
CHECK	P.A		16.01.19
APPRD.	R.D		16.01.19

CLIENT -
PROJECT-
SITE LOCATION -
If any queries contact : design@nihva.com
DWG. NO. : NIHVA/18-19/VDR/347
REV- 0
ALL DIMENSION ARE IN mm
SCALE: NTS
WT:
SHEET: 01 OF 01