




ELEVATION 1

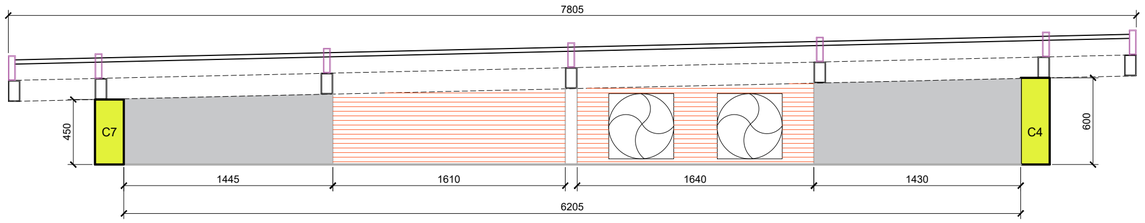


ELEVATION 2

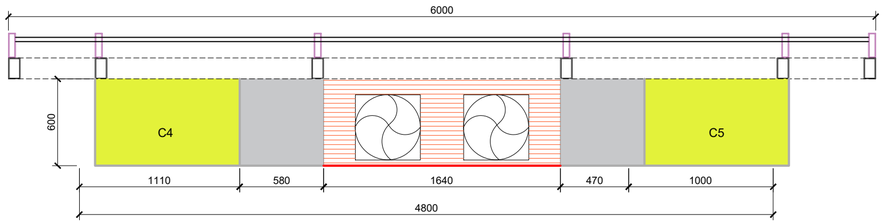


ELEVATION 3

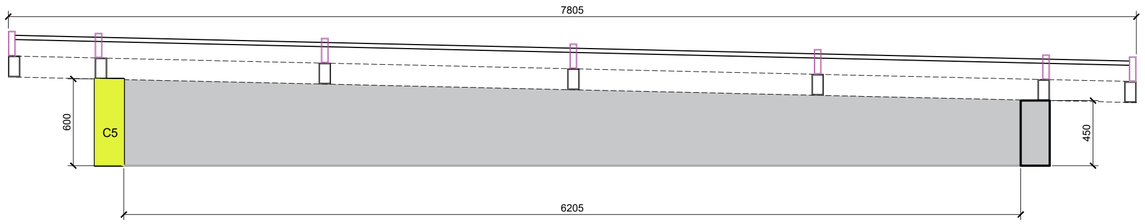

ELEVATION 4

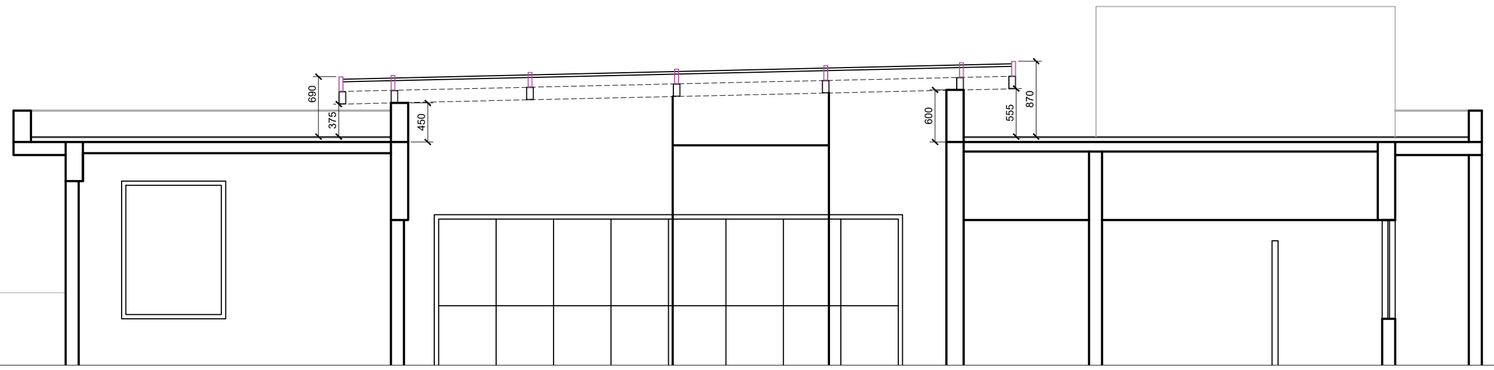

SECTION AA'
Scale 1:50

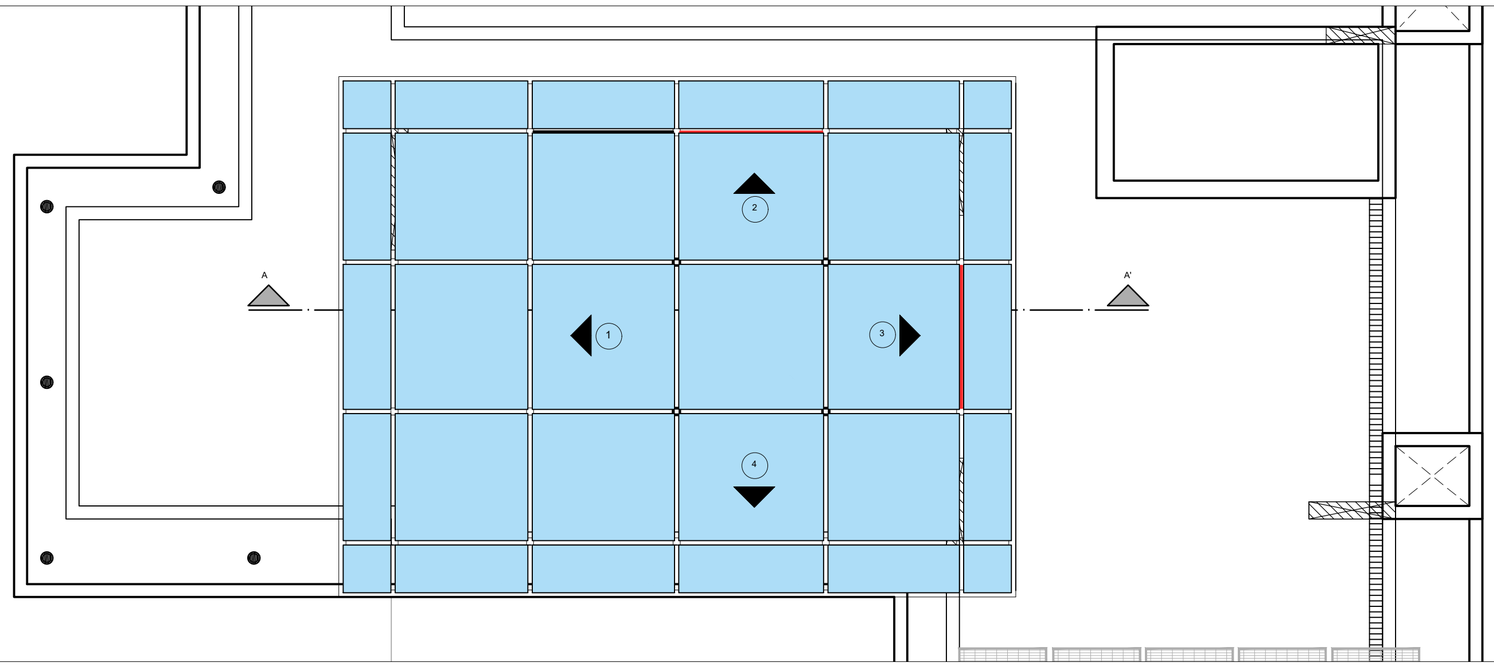

SKYLIGHT PLAN
Scale 1:50

LEGEND:

	LOUVERS
	EXHAUST
	8+8mm laminated glass- high performance
	schuco profile section 50 X 170mm as per drawing received
	MS framing 145X82X6mm as approved by structural engineer

NOTE:
THIS DRAWING IS AN ARCHITECTURAL INTENT ONLY FOR PARDI DIMENSIONS AND EXHAUST, LOUVERS PROVISION REFER STRUCTURAL CONSULTANT DRAWINGS FOR MS FRAMING AND SCHUCO DRAWINGS FOR SKYLIGHT FRAMING

THIS DRAWING IS THE PROPERTY OF GRIT DESIGN AND RESEARCH STUDIO AND IS NOT TO BE USED OR REPRODUCED WITHOUT THEIR PERMISSION.

THE CONTRACTOR MUST VERIFY ALL DIMENSIONS ON THE JOB AND REPORT ANY DISCREPANCIES TO THE ARCHITECTS.

277, PALLOD FARMS

SKYLIGHT ARCHITECTURAL INTENT

GRIT
ENVIRONMENTAL DESIGN + RESEARCH STUDIO
architecture + landscape architecture + environmental psychology

1402 PORTIA || ONE PALLOD FARMS || BANER || PUNE 411045

SCALE
As mentioned

NORTH