


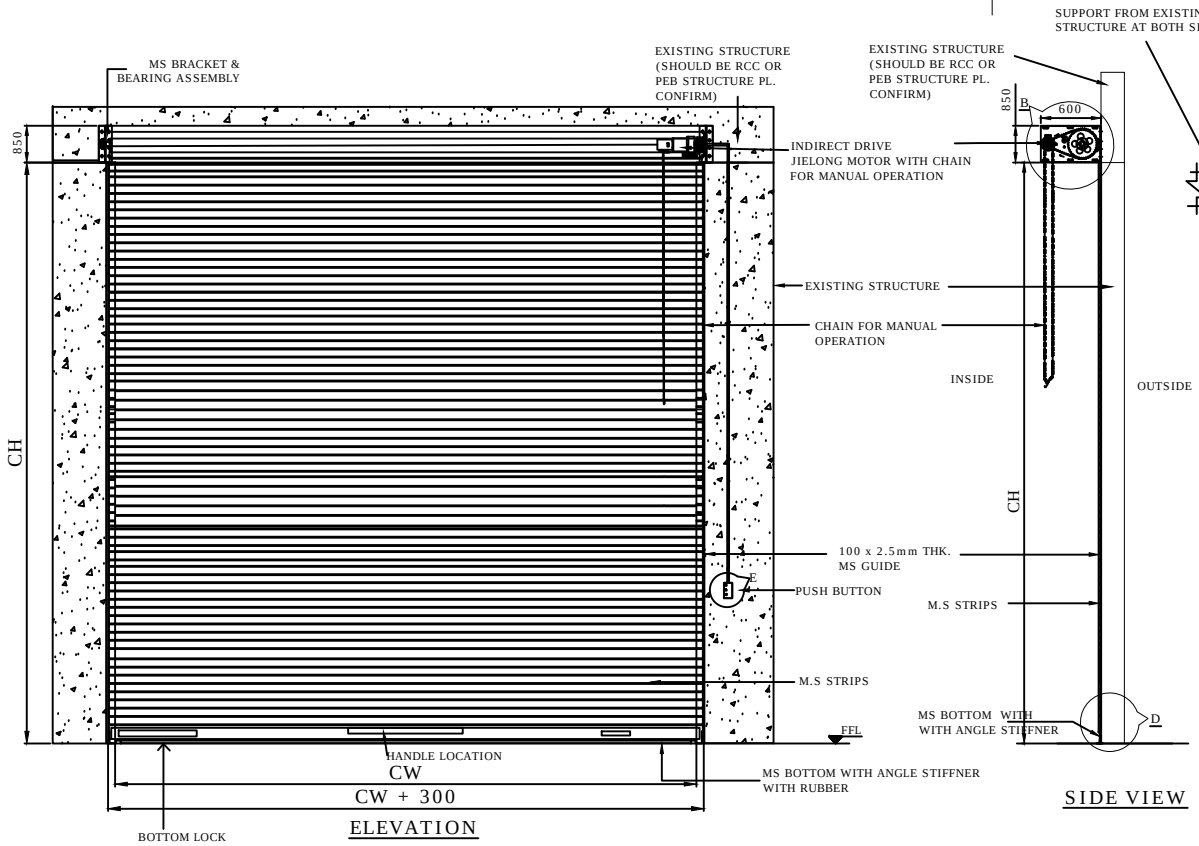


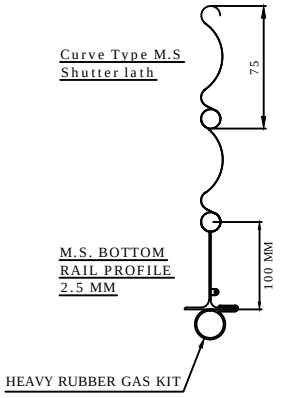

DETAILS : D

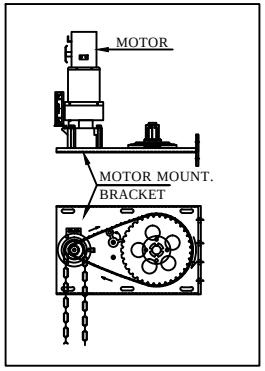

DETAILS : A & B

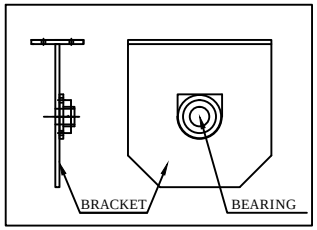

DETAILS : C

(NOTE: REQUIRED TECHANICAL STRUCTURE FOR SHUTTER IN CLIENT SCOPE)

4000	6000	2	RAL -
CLEAR WIDTH (CW)	CLEAR HEIGHT (CH)	QUANTITY	RAL COLOR

This drawing & design is the property of NIHVA TECHNOLOGIES. Not to be sold or copied to any other concern.

TITLE: MOTORIZED ROLLING SHUTTER

NIHVA TECHNOLOGIES PVT. LTD.
NIHVA TECHNOLOGIES PVT. PUNE
Tel : 020 66304033
Email:- info@nihva.com
Website:- www.nihva.com

	NAME	SIGN	DATE
DRAWN	P.A		19.11.2019
CHECK	G.J		19.11.2019
APPRD.			

CLIENT - INGERSOLL RAND (INDIA) LIMITED

PROJECT -

SITE LOCATION - GUJARAT

If any queries contact : design@nihva.com

DWG. NO. : NIHVA/19-20/0156

REV- R00

ALL DIMENSION ARE IN mm

SCALE: NTS | WT: | SHEET: