



NOTE :
1. DOOR HINGES : GEZE MAKE.
2. DOOR CLOSER : GEZE MAKE.
3. DOOR EXTERNAL TRIM : YELE MAKE.
4. DOOR PANIC BAR : YELE MAKE.

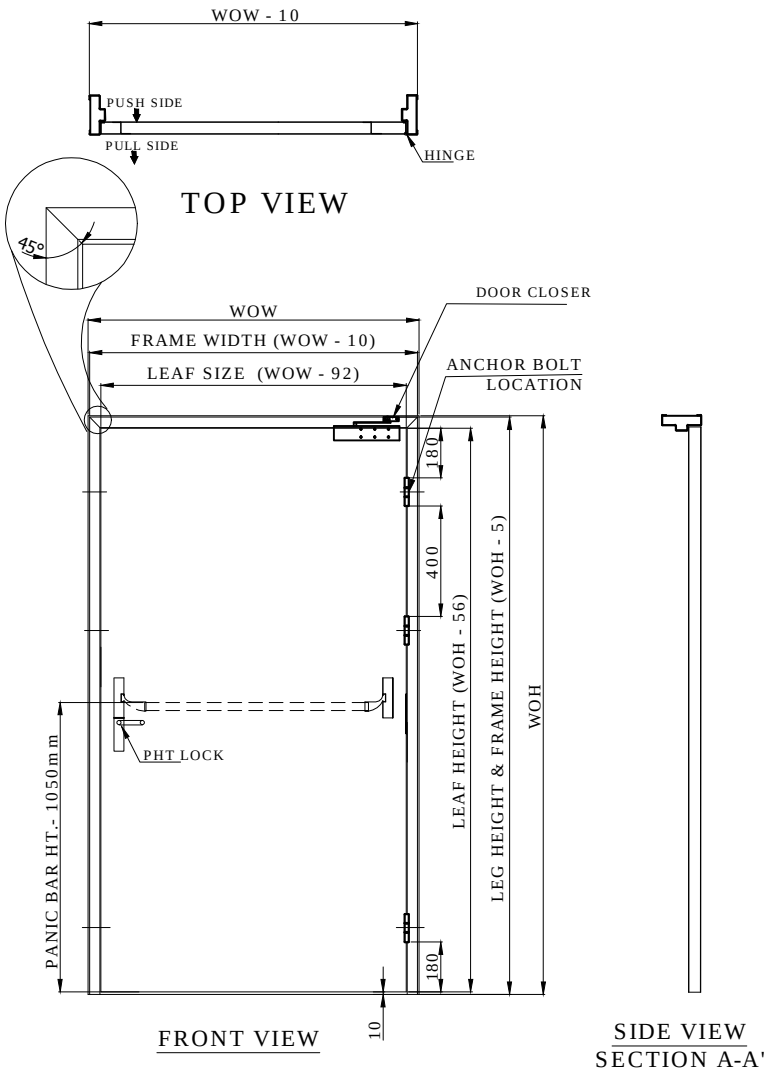

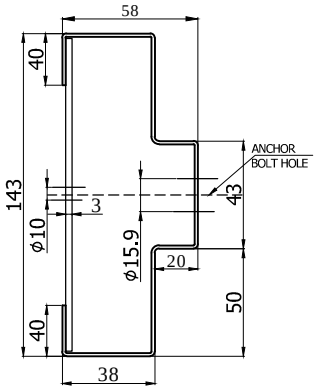

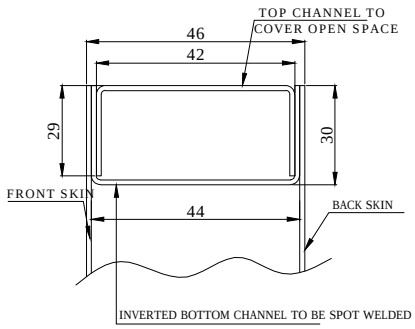

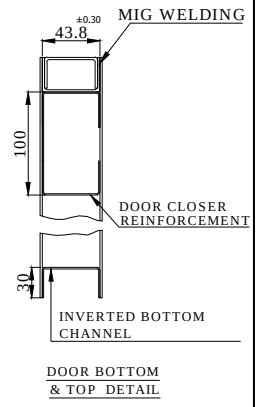

SR. NO	WALL OPENING WIDTH	WALL OPENING HEIGHT	QTY	RAL	LOCATION	HARDWARE
04	1200	2100	12	3020	Block F	Single leaf metal door with Hinges , Door closer , Single point panic bar, with external trim
03	1200	2100	04	3020	Block D	Single leaf metal door with Hinges , Door closer , Single point panic bar, with external trim
02	1200	2100	12	3020	Block C	Single leaf metal door with Hinges , Door closer , Single point panic bar, with external trim
01	1200	2400	01	3020	Block B - First floor	Single leaf metal door with Hinges , Door closer , Single point panic bar with external trim

TOLERANCE - ±05mm

This drawing & design is the property of NIHVA TECHNOLOGIES. Not to be sold or copied to any other concern.

TITLE: SINGLE LEAF STEEL DOOR

	NAME	SIGN	DATE
DRAWN	P.V.A		21.03.2019
CHECK	V.M.T		21.03.2019
APPRD.			

NIHVA TECHNOLOGIES PVT. LTD.
NIHVA TECHNOLOGIES PVT. PUNE
Tel : 020 66304033
Email:- info@nihva.com
Website:- www.nihva.com

CLIENT -
PROJECT -
SITE LOCATION -
If any queries contact : design@nihva.com
DWG. NO. : NIHVA/18-19/VDR/428
REV- R00
ALL DIMENSION ARE IN mm
SCALE: NTS
WT:
SHEET: 01 OF 01