


230 V & 50 Hz
Single phase supply
Required near left side of Operator.

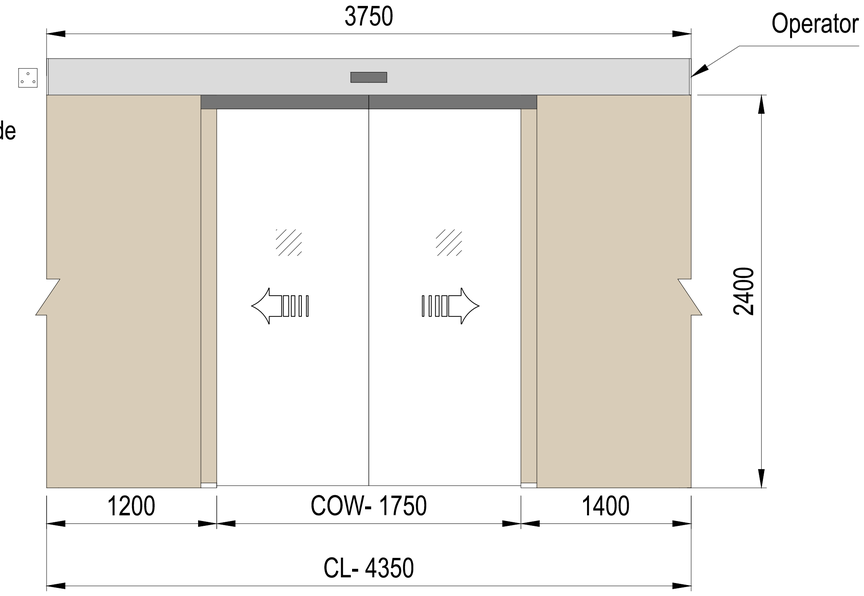


Inside Elevation

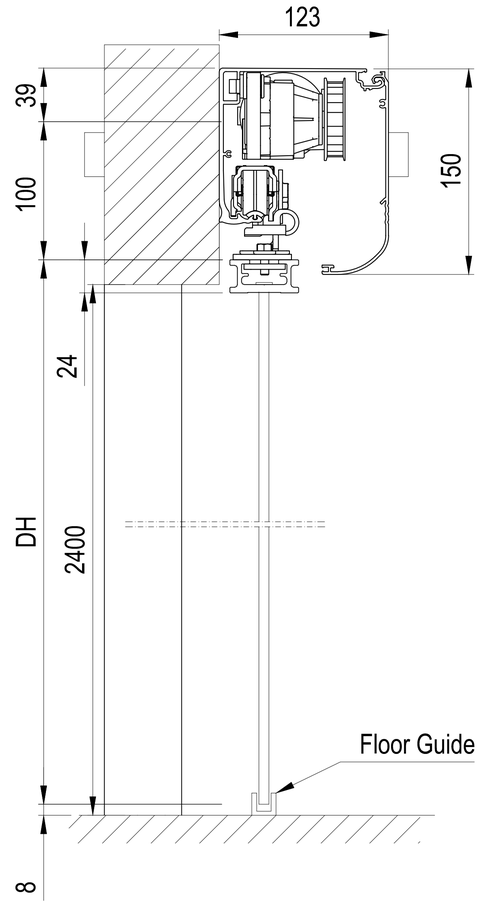

Fixing Plan

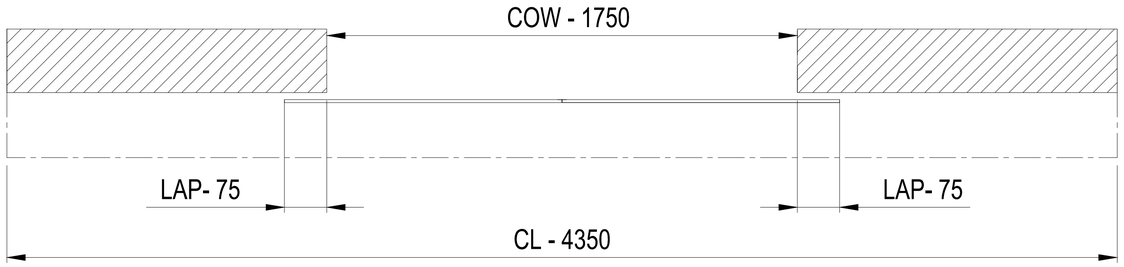

Closed Condition

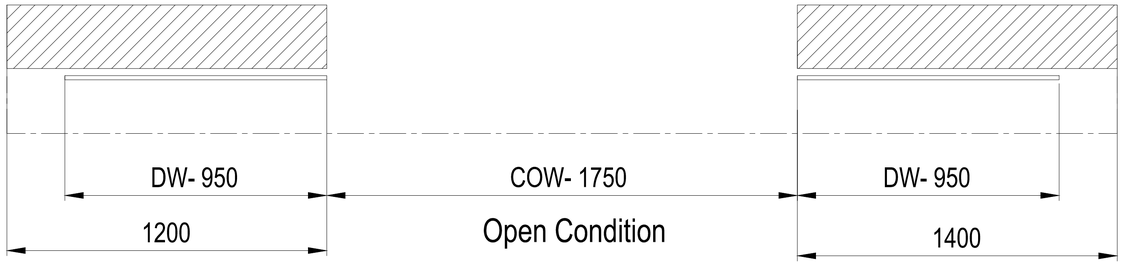

Open Condition

Plan



Fixing Plan

Door Size

Sr. No.	Clear Width	Clear Height	Quantity
1	1750	2400	1

Glass Type- 12mm Toughened

This drawing & designing is the property of NIHVA TECHNOLOGIES. Not to be sold or copied to any other concern.

TITLE: AUTOMATIC SLIDING GLASS DOOR

NIHVA TECHNOLOGIES PVT. LTD. PUNE
Tel : 020 66304033
Email:- info@nihva.com
Website:- www.nihva.com

	SIGN	DATE
DRAWN	OMKAR	15/07/17
CHECK	S.S.	15/07/17
REV.	00	
APPROVAL		

CLIENT - VIJAY LOGISTICS
PROJECT -
SITE - CHAKAN
DWG. NO. : NIHVA/17-18/0132
If any queries contact : projects@nihva.com
SCALE: NTS | WT: | SHEET: 01 OF 01
ALL DIMENSION ARE IN mm