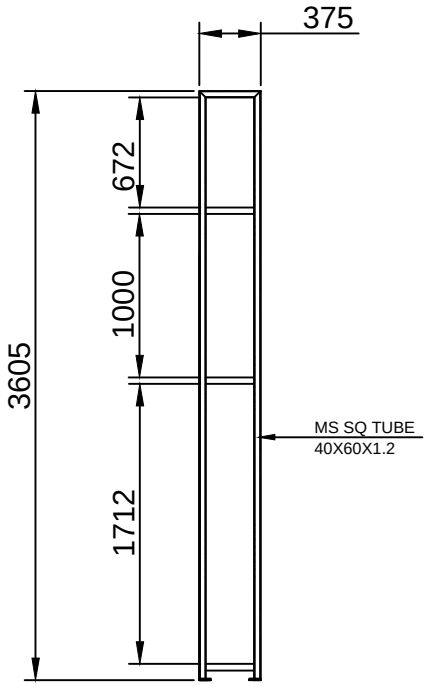


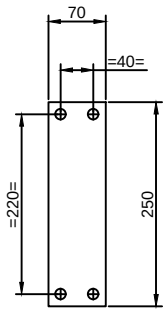


MATERIAL:MS PLATE
THK:10MM
QTY:04 nos

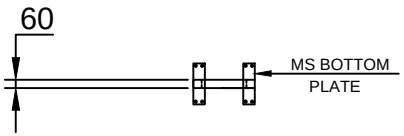


# CRM DOOR 04

QTY:02 NOS

This drawing & design is the property of NIHVA TECHNOLOGIES. Not to be sold or copied to any other concern.

4 LEAF RIGHT SIDE
CRM DOOR 04/GATE 13

NIHVA TECHNOLOGIES PVT. LTD. PUNE
Tel : 020 66304033
Email:- info@nihva.com
Website:- www.nihva.com

| | NAME | DATE |
|---|---|---|
| DRAWN | KISHAN | 16/05/2022 |
| CHECK | M.SUTAR | 16/05/2022 |
| APPRD. | V.TARAK | 16/05/2022 |

If any queries contact : design@nihva.com

ALL DIMENSION ARE IN mm

CLIENT - NIHVA TECHNOLOGIES PVT LTD
LOCATION -
PRODUCT - SLIDING DOOR
DWG NO:-NIHVA/22-23/CLT/
SCALE: NTS | SCALE:-- 1:1 | SHEET:

| Rev No. | Revision | Date | Revised By |
|---|---|---|---|
| | | | |