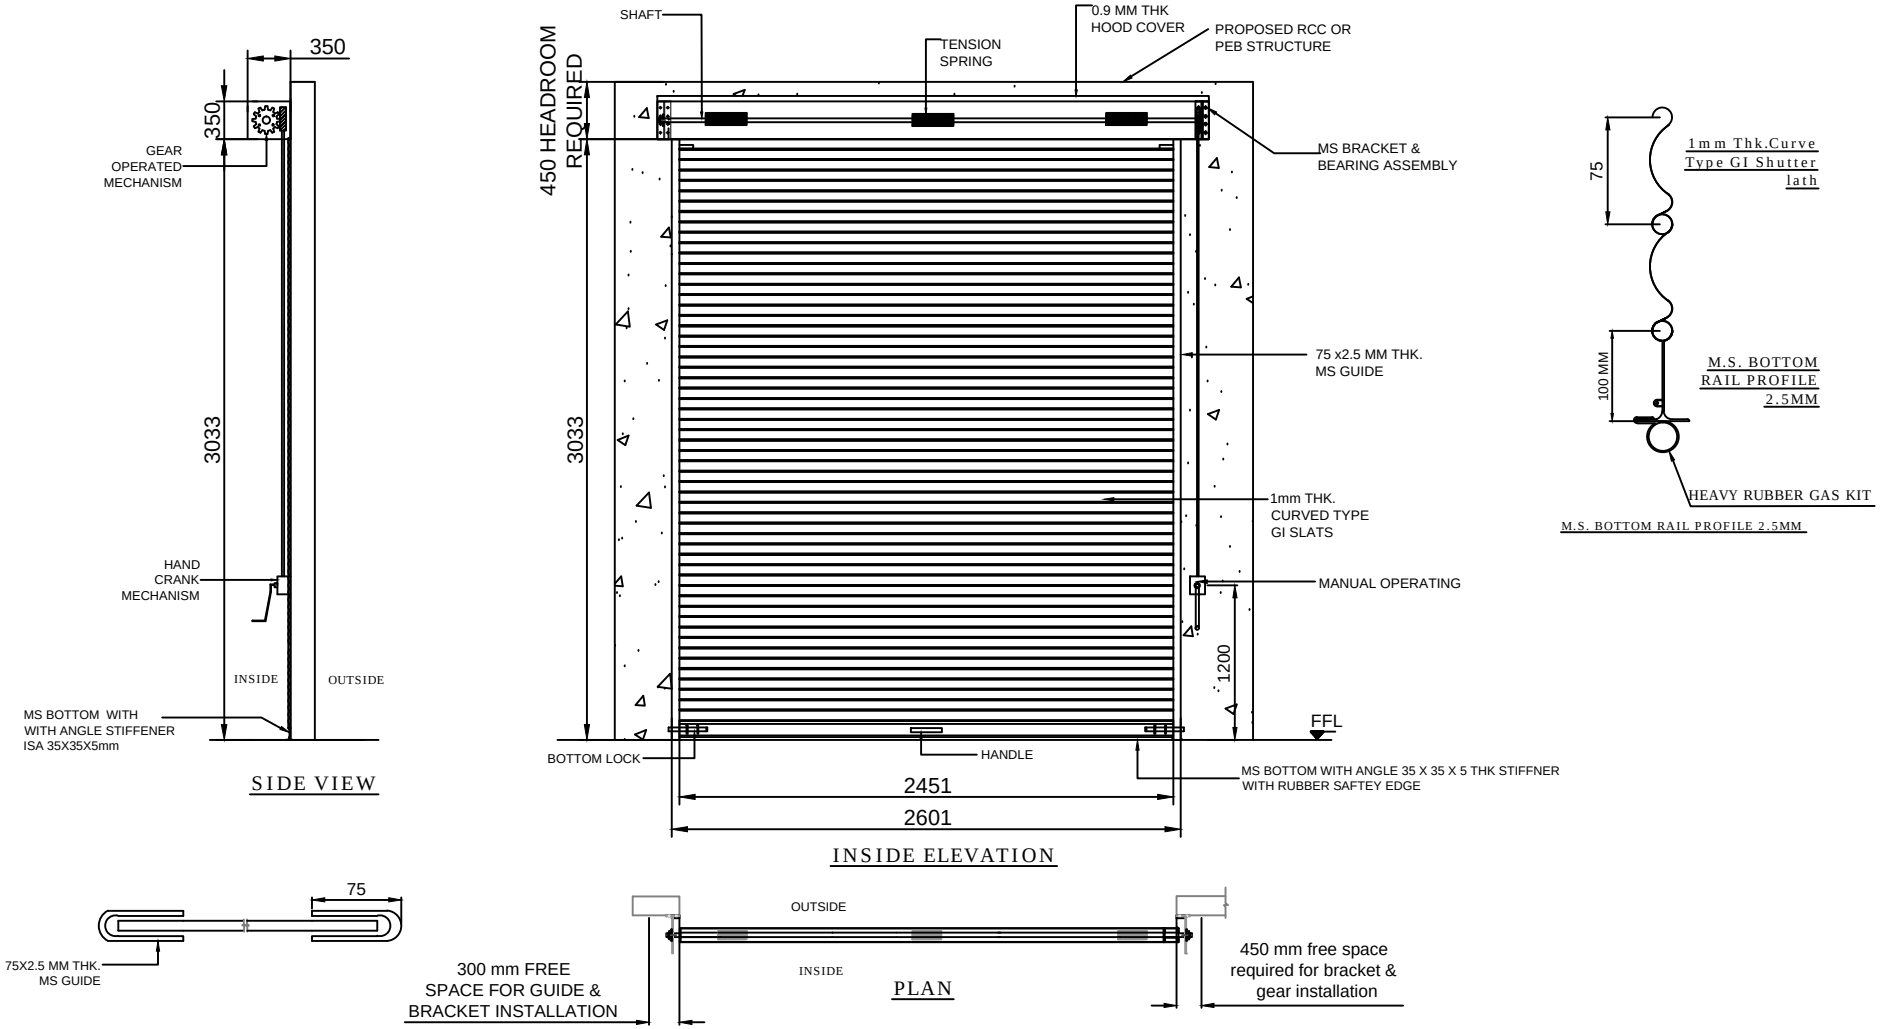


S.N.	LOCATION	SIZE	QUANTITY
1	B50	2451(W)X3033(H)	11 Nos

NOTE-
1. ALL CIVIL WORK WILL BE CLIENT'S SCOPE.
2.STRUCTURE REQUIRED FOR SHUTTER IS IN CLIENT'S SCOPE.
3.FINAL FINISH OF SHUTTER WILL BE IN POWDER COATING OF APPROVED COLOR i.e.RAL 7001.
4.DESIGN OF SHUTTER IS AS PER I.S. 6248:1979 STANDARDS.

TOLERANCE - ±10mm

This drawing & design is the property of NIHVA TECHNOLOGIES. Not to be sold or copied to any other concern.

TITLE: GEAR OPERATED ROLLING SHUTTER 2.451mX3.033m Right side gear box.

	NAME	SIGN	DATE
DRAWN	SURAJ		29.08.2018
CHECK	PRADEEP		29.08.2018
APPRD.	R.D		29.08.2018

NIHVA TECHNOLOGIES PVT. LTD.
Website:- www.nihva.com
NIHVA TECHNOLOGIES PVT. LTD. PUNE
Tel : 020 66304033
Email:- info@nihva.com

CLIENT - INDOSPACE
PROJECT - BUILDING B50
SITE LOCATION - CHAKAN 1
If any queries contact : design@nihva.com
DWG. NO. : NIHVA/18-19/0115
REV- 0
ALL DIMENSION ARE IN mm
SCALE: NTS
WT:
SHEET: 01 OF 01