



PART NO.	PART NAME	DESCRIPTION	QTY
1.	ISMB	150 X 75 X 2305L	6 NOS
2.	R.TUBE	145 X 82 X 5.4THK X 2305L	2 NOS
3.	FLAT	150 X 16 X 2000L	2 NOS
4.	FLAT	75 X 16 X 75L	4 NOS
5.	FLAT	150 X 8 X 184L	6 NOS
6.	FLAT	75 X 6 X 525L	1 NO
7.	FLAT	100 X 16 X 80L	8 NOS
8.	BEND	100 X 3THK X 2220L	2 NOS
9.	SIDE COVER	275 X 3THK X 1500L	2 NOS
10.	LIP STOPER	Ø25 X 50L	4 NOS
11.	CHEQ.SHEET	2000 X 5 THK X 2424L	1 NO
12.	EYE BOLT	M16 X STD WITH NUT	3 NOS

NOTE:~ MTL : MS

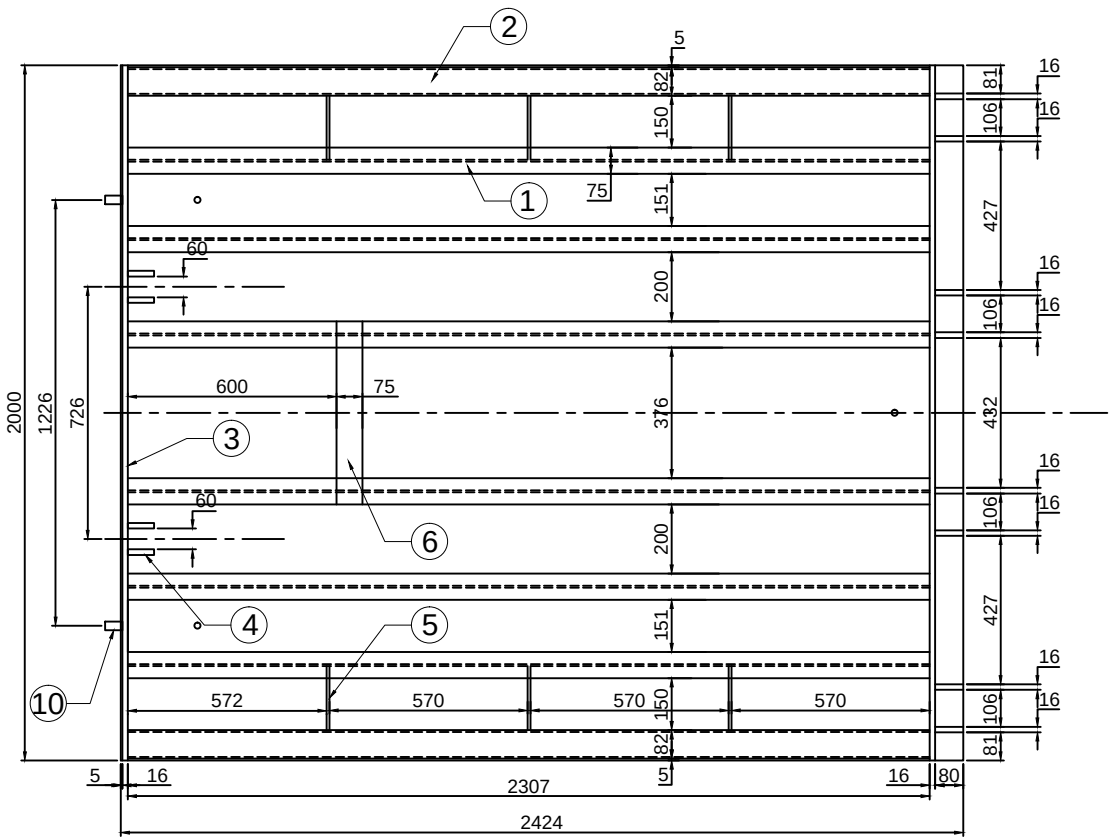

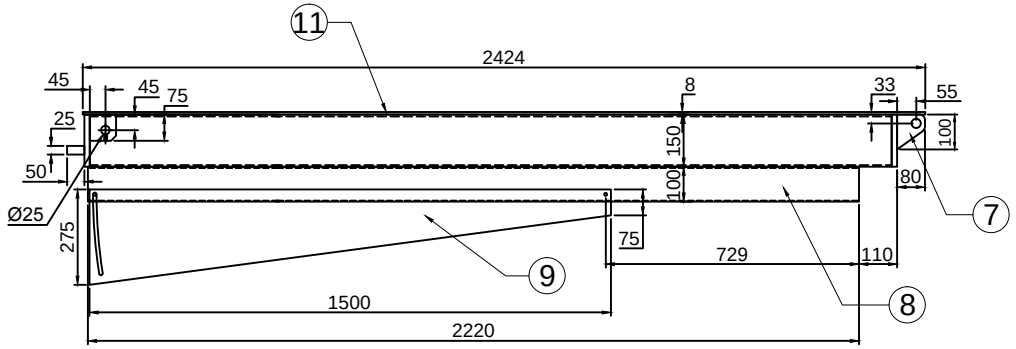

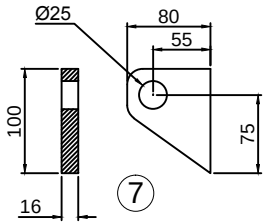

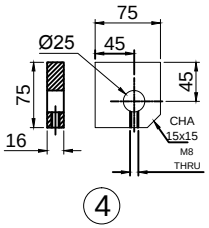

This drawing & design is the property of NIHVA TECHNOLOGIES. Not to be sold or copied to any other concern.

TITLE

DECK ASSLY

NIHVA TECHNOLOGIES PVT. LTD.

NIHVA TECHNOLOGIES PVT. LTD. PUNE
Tel : 020 66304033
Email:- info@nihva.com
Website:- www.nihva.com

	NAME	SIGN	DATE
DRAWN	PRADEEP		23.04.2018
CHECK	PRADEEP		23.04.2018
APPRD.	PRADEEP		23.04.2018

CLIENT -

PROJECT - NSDL2025

SITE LOCATION -

If any queries contact : design@nihva.com

DWG. NO. : NIHVA/18-19/NSDL2025_001

ALL DIMENSION ARE IN mm

SCALE: NTS | WT: | REV- 00