

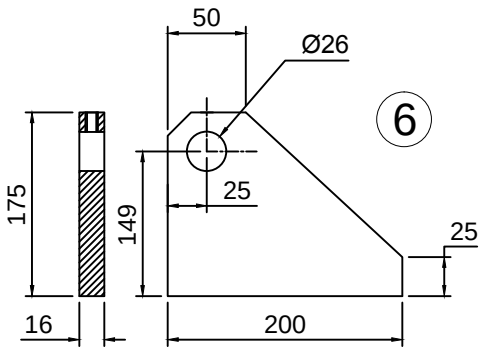


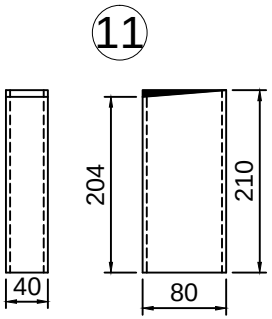

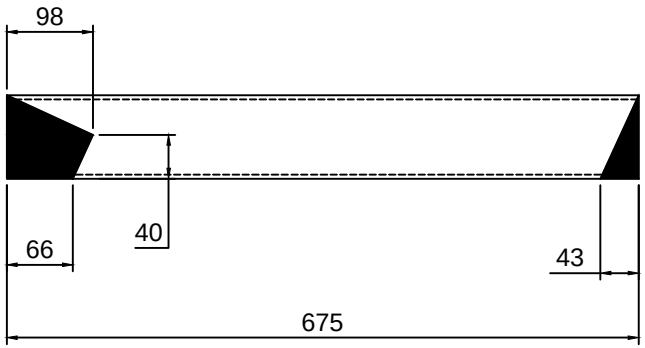

TOP SIDE

This drawing & design is the property of NIHVA TECHNOLOGIES. Not to be sold or copied to any other concern.

TITLE: BASE FRAME DETAILS			NIHVA TECHNOLOGIES PVT. LTD. PUNE Tel : 020 66304033 Email:- info@nihva.com Website:- www.nihva.com
NAME	SIGN	DATE	
DRAWN PRADEEP		05.09.2018	CLIENT -
CHECK PRADEEP		05.09.2018	PROJECT - NSDL2025
APPRD. PRADEEP		05.09.2018	SITE LOCATION -
If any queries contact : design@nihva.com			DWG. NO. : NIHVA/18-19/MFG/NSDL2025/005
ALL DIMENSION ARE IN mm			SCALE: NTS / WT: / REV- 00