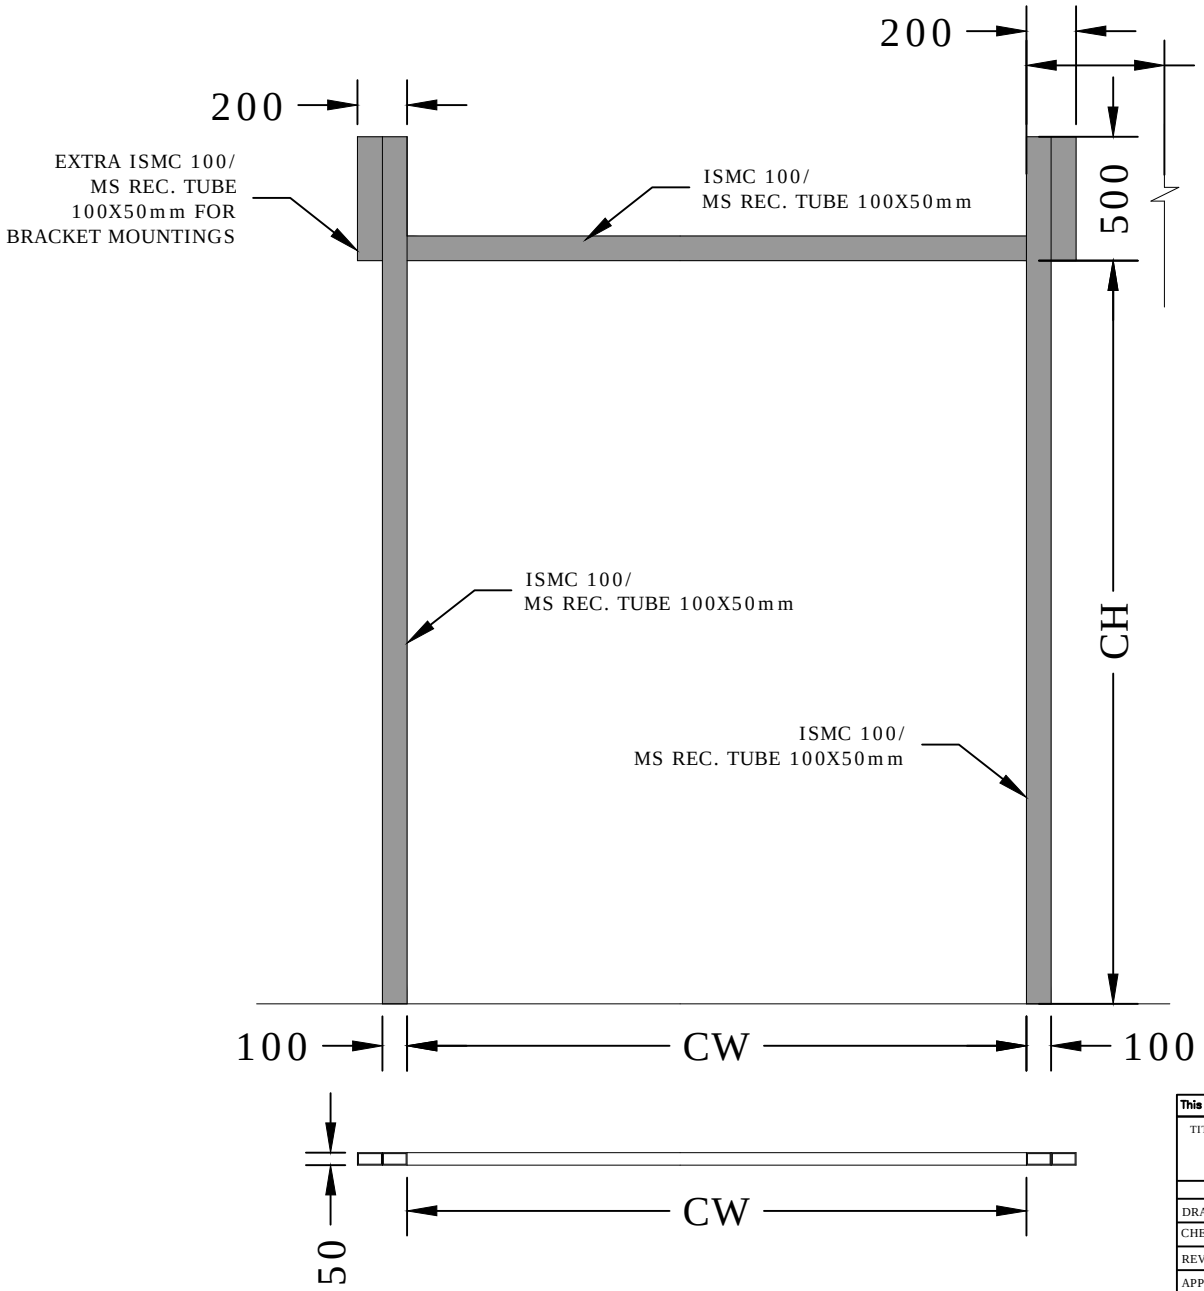


| CLEAR WIDTH (CW) | CLEAR HEIGHT (CH) | QUANTITY |
|---|---|---|
| 3000 mm | 3500 mm | 2 NOS |

This drawing & design is the property of NIHVA TECHNOLOGIES. Not to be sold or copied to any other concern.

TITLE: MS STRUCTURE FOR DOUBLE WALL ROLLING SHUTTER 2

| | SIGN | DATE |
|---|---|---|
| DRAWN | OMKAR | 03/02/18 |
| CHECK | SHEKHAR | 03/02/18 |
| REV. | | |
| APPROVAL | SHEKHAR | 03/02/18 |

If any queries contact : projects@nihva.com

ALL DIMENSION ARE IN mm

NIHVA
NIHVA TECHNOLOGIES PVT. LTD.
NIHVA TECHNOLOGIES PVT. LTD. PUNE
Tel : 020 66304033
Email:- info@nihva.com
Website:- www.nihva.com

CLIENT - LM WIND POWER BLADES (INDIA) PVT. LTD.

PROJECT -

SITE - BANGLORE

DWG. NO. : NIHVA/17-18/0348 | REV- 0

SCALE: NTS | WT: | SHEET: 01 OF 01