

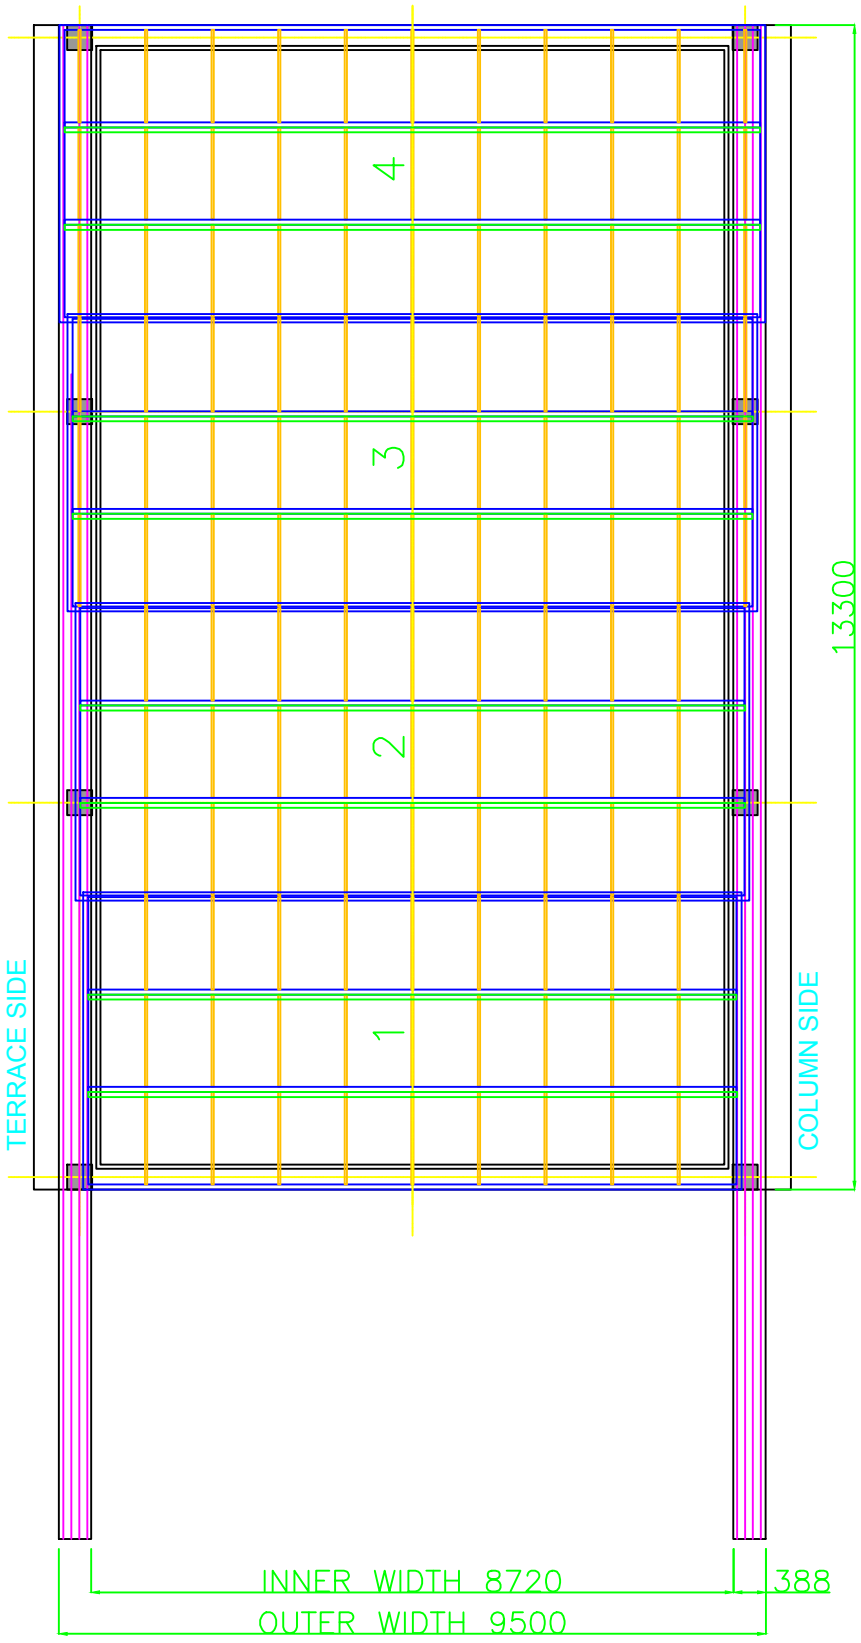


ENCLOSED PLAN

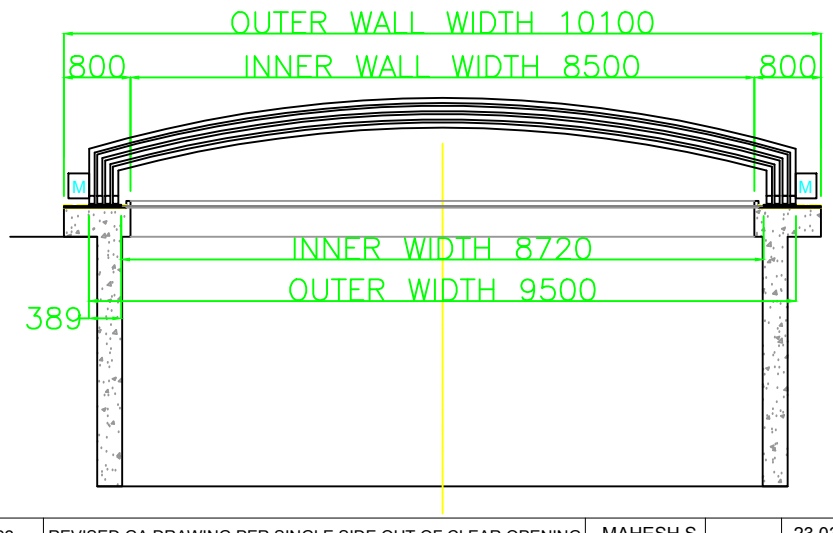

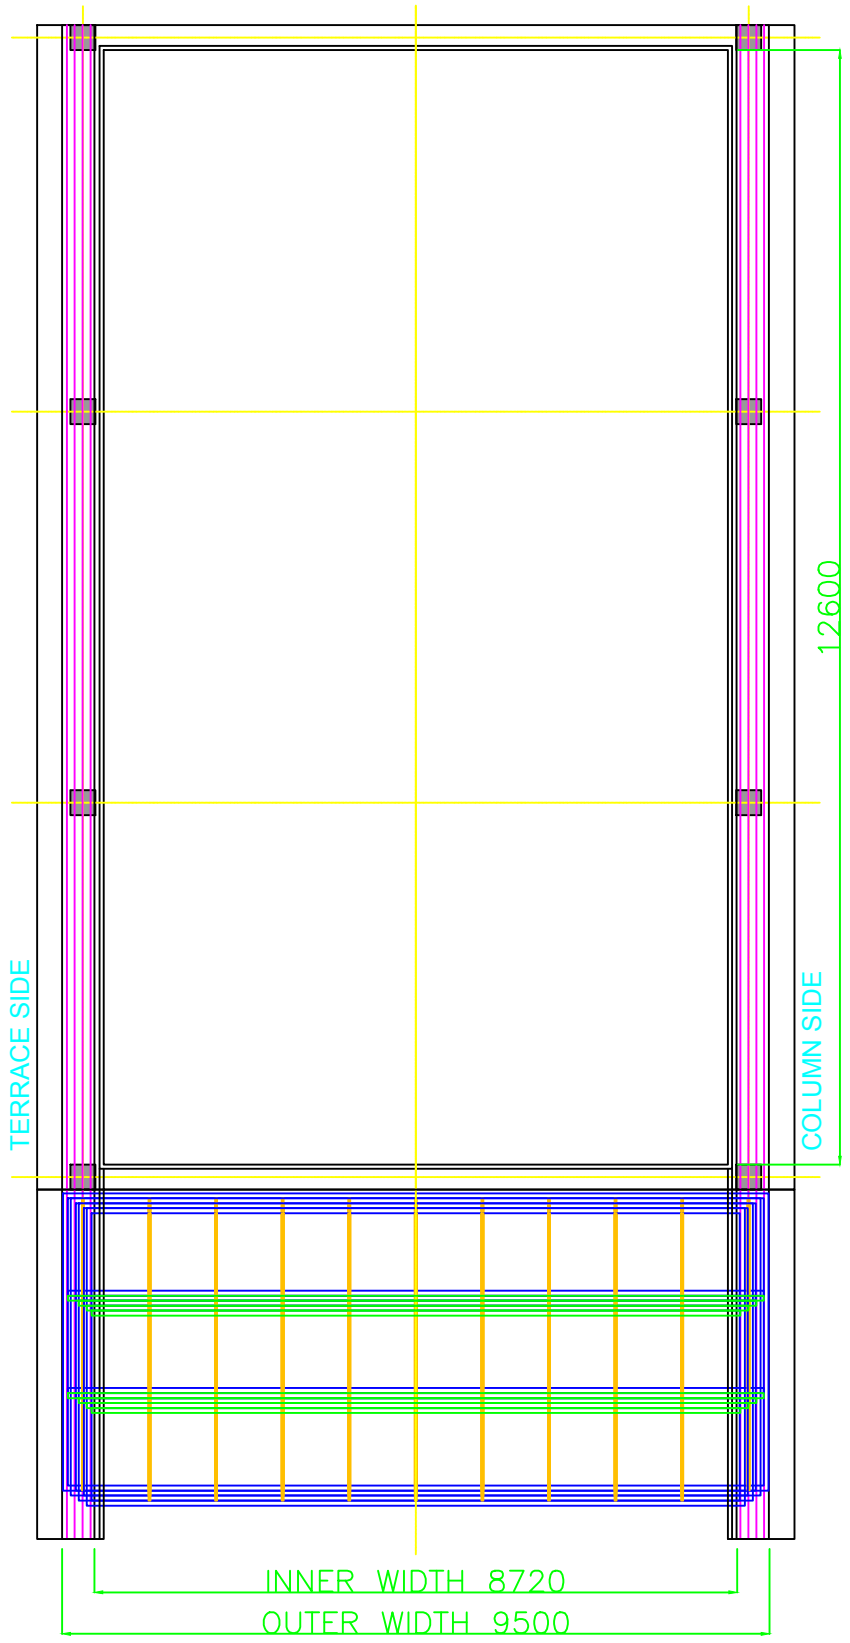

STACKED PLAN

STANDARD PART		
PART LIST	LENGTH	QTY
GNT 001	17.5 M	2
GNT 002	17.5 M	6
GNT 007	3.425 M	8

REV.	DESCRIPTION.	REVISED BY	SIGN	DATE
002	REVISED GA DRAWING PER SINGLE SIDE OUT OF CLEAR OPENING	MAHESH S.		23.03.23
001	REVISED GA DRAWING PER BI-PARTING WITHIN CLEAR OPENING	MAHESH S.		23.03.23
000	RELEASED GA DWG FOR APPROVAL	GAURAV J.		23.03.23

This drawing & design is the property of NIHVA TECHNOLOGIES. Not to be sold or copied to any other concern.

	NAME	SIGN	DATE	
TITLE: ASSLY LAYOUT				
DRAWN	MAHESH S.		23.03.23	CLIENT - MR. PRANAV
CHECK	MAHESH S.		23.03.23	LOCATION - NOIDA_IN
APPRD.	VIJAY T.		23.03.23	PRODUCT - RETRACTABLE ROOF
If any queries contact : projectsautomation@nihva.com				NIHVA\22-23\02XX — REV- 0
ALL DIMENSION ARE IN mm				SCALE: NTS — SHEET: 01 OF 01