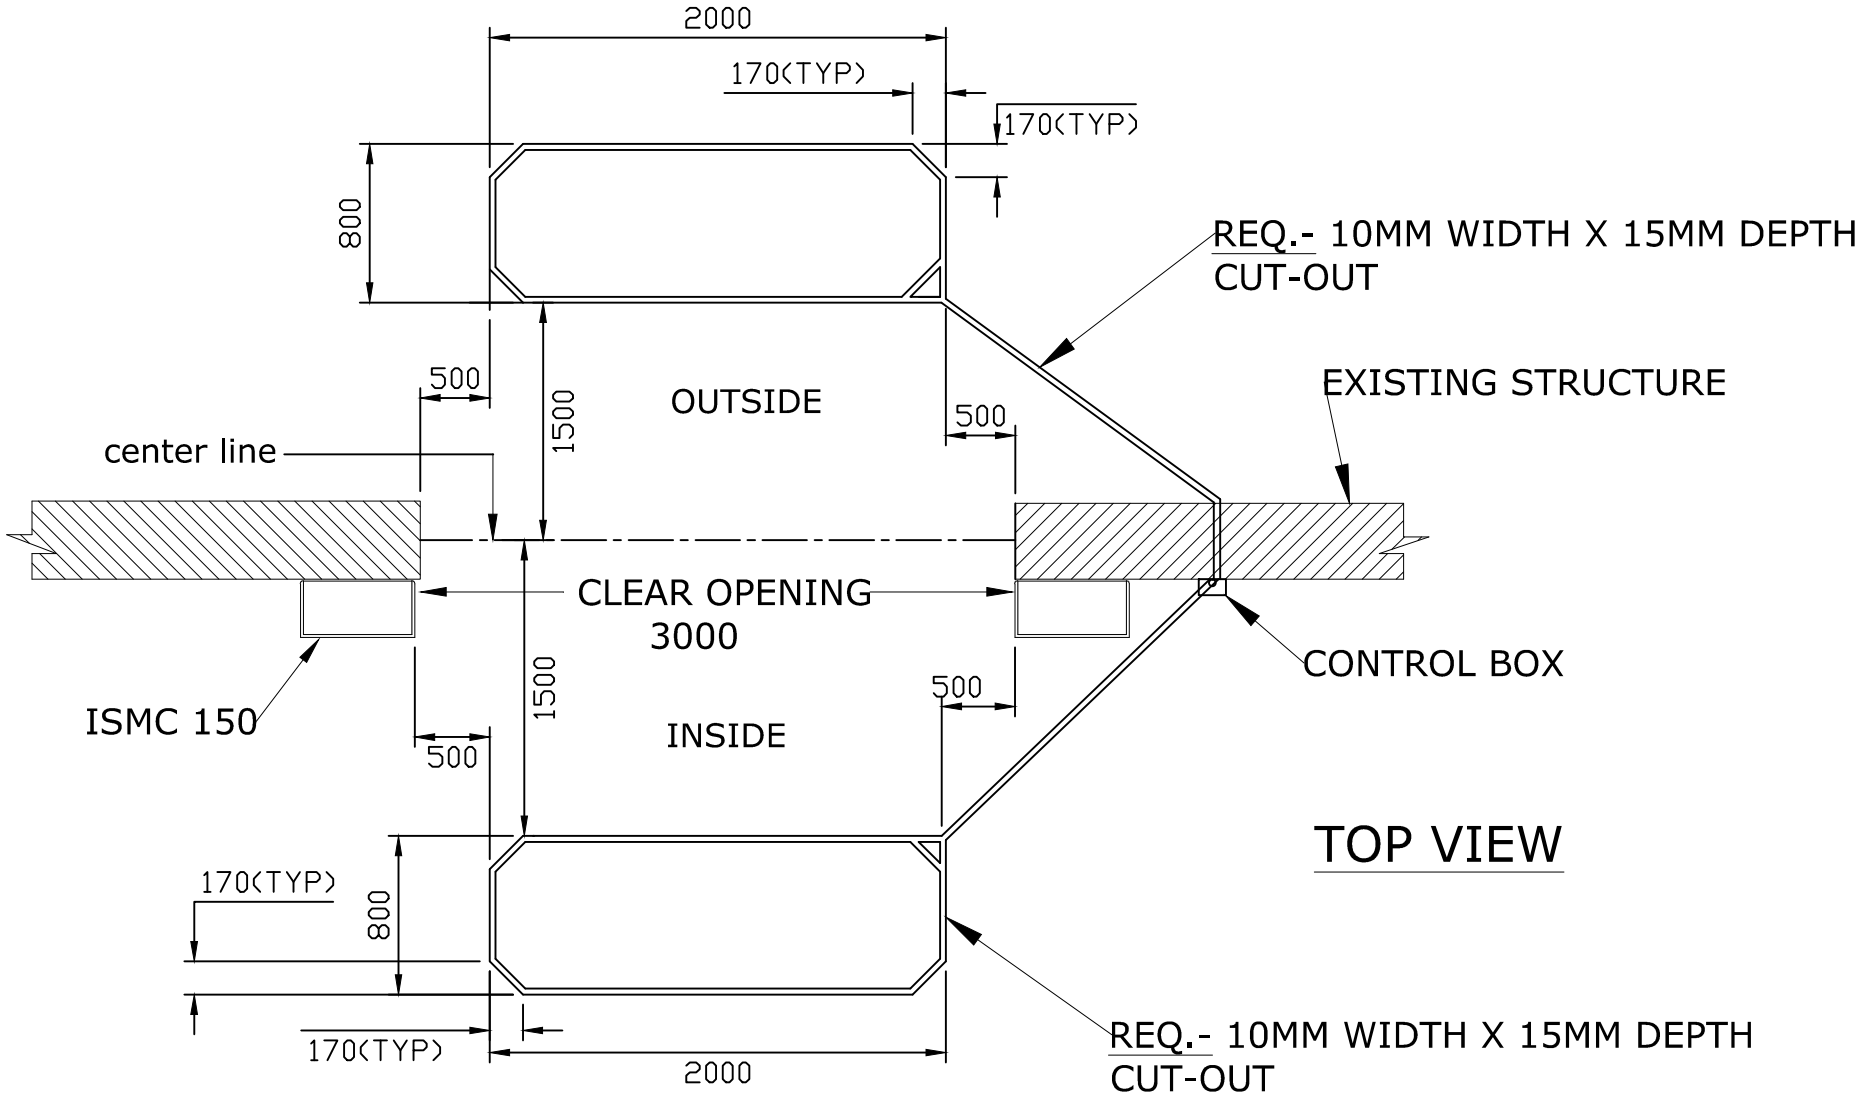


FLOOR CUT-OUT FOR LOOP
DETECTOR FOR
HIGH SPEED DOOR

This drawing & designing is the property of NIHVA TECHNOLOGIES. Not be sold or copy to any other concern.

TITLE

FLOOR CUT-OUT FOR LOOP
DETECTOR FOR
HIGH SPEED DOOR

CLIENT APPROVAL

ALL DIMENSION ARE IN mm

NIHVA TECHNOLOGIES PVT. LTD.

NIHVA TECHNOLOGY
PVT. LTD. PUNE
Tel : 020 66304033
Email:- info@nihva.com
Website:- www.nihva.com

	SIGN	DATE	
DRAWN	OMKAR	17/03/16	CLIENT -MARS INTERNATIONAL
CHECK	ANIL	17/03/16	PROJECT-
ENG			SITE -
APPRD.			DWG. NO. - NVA/15-16/231
MFG			SCALE: 01 | WT: | SHEET: 01
Ref. No.			If any queries contact : projects@nihva.com