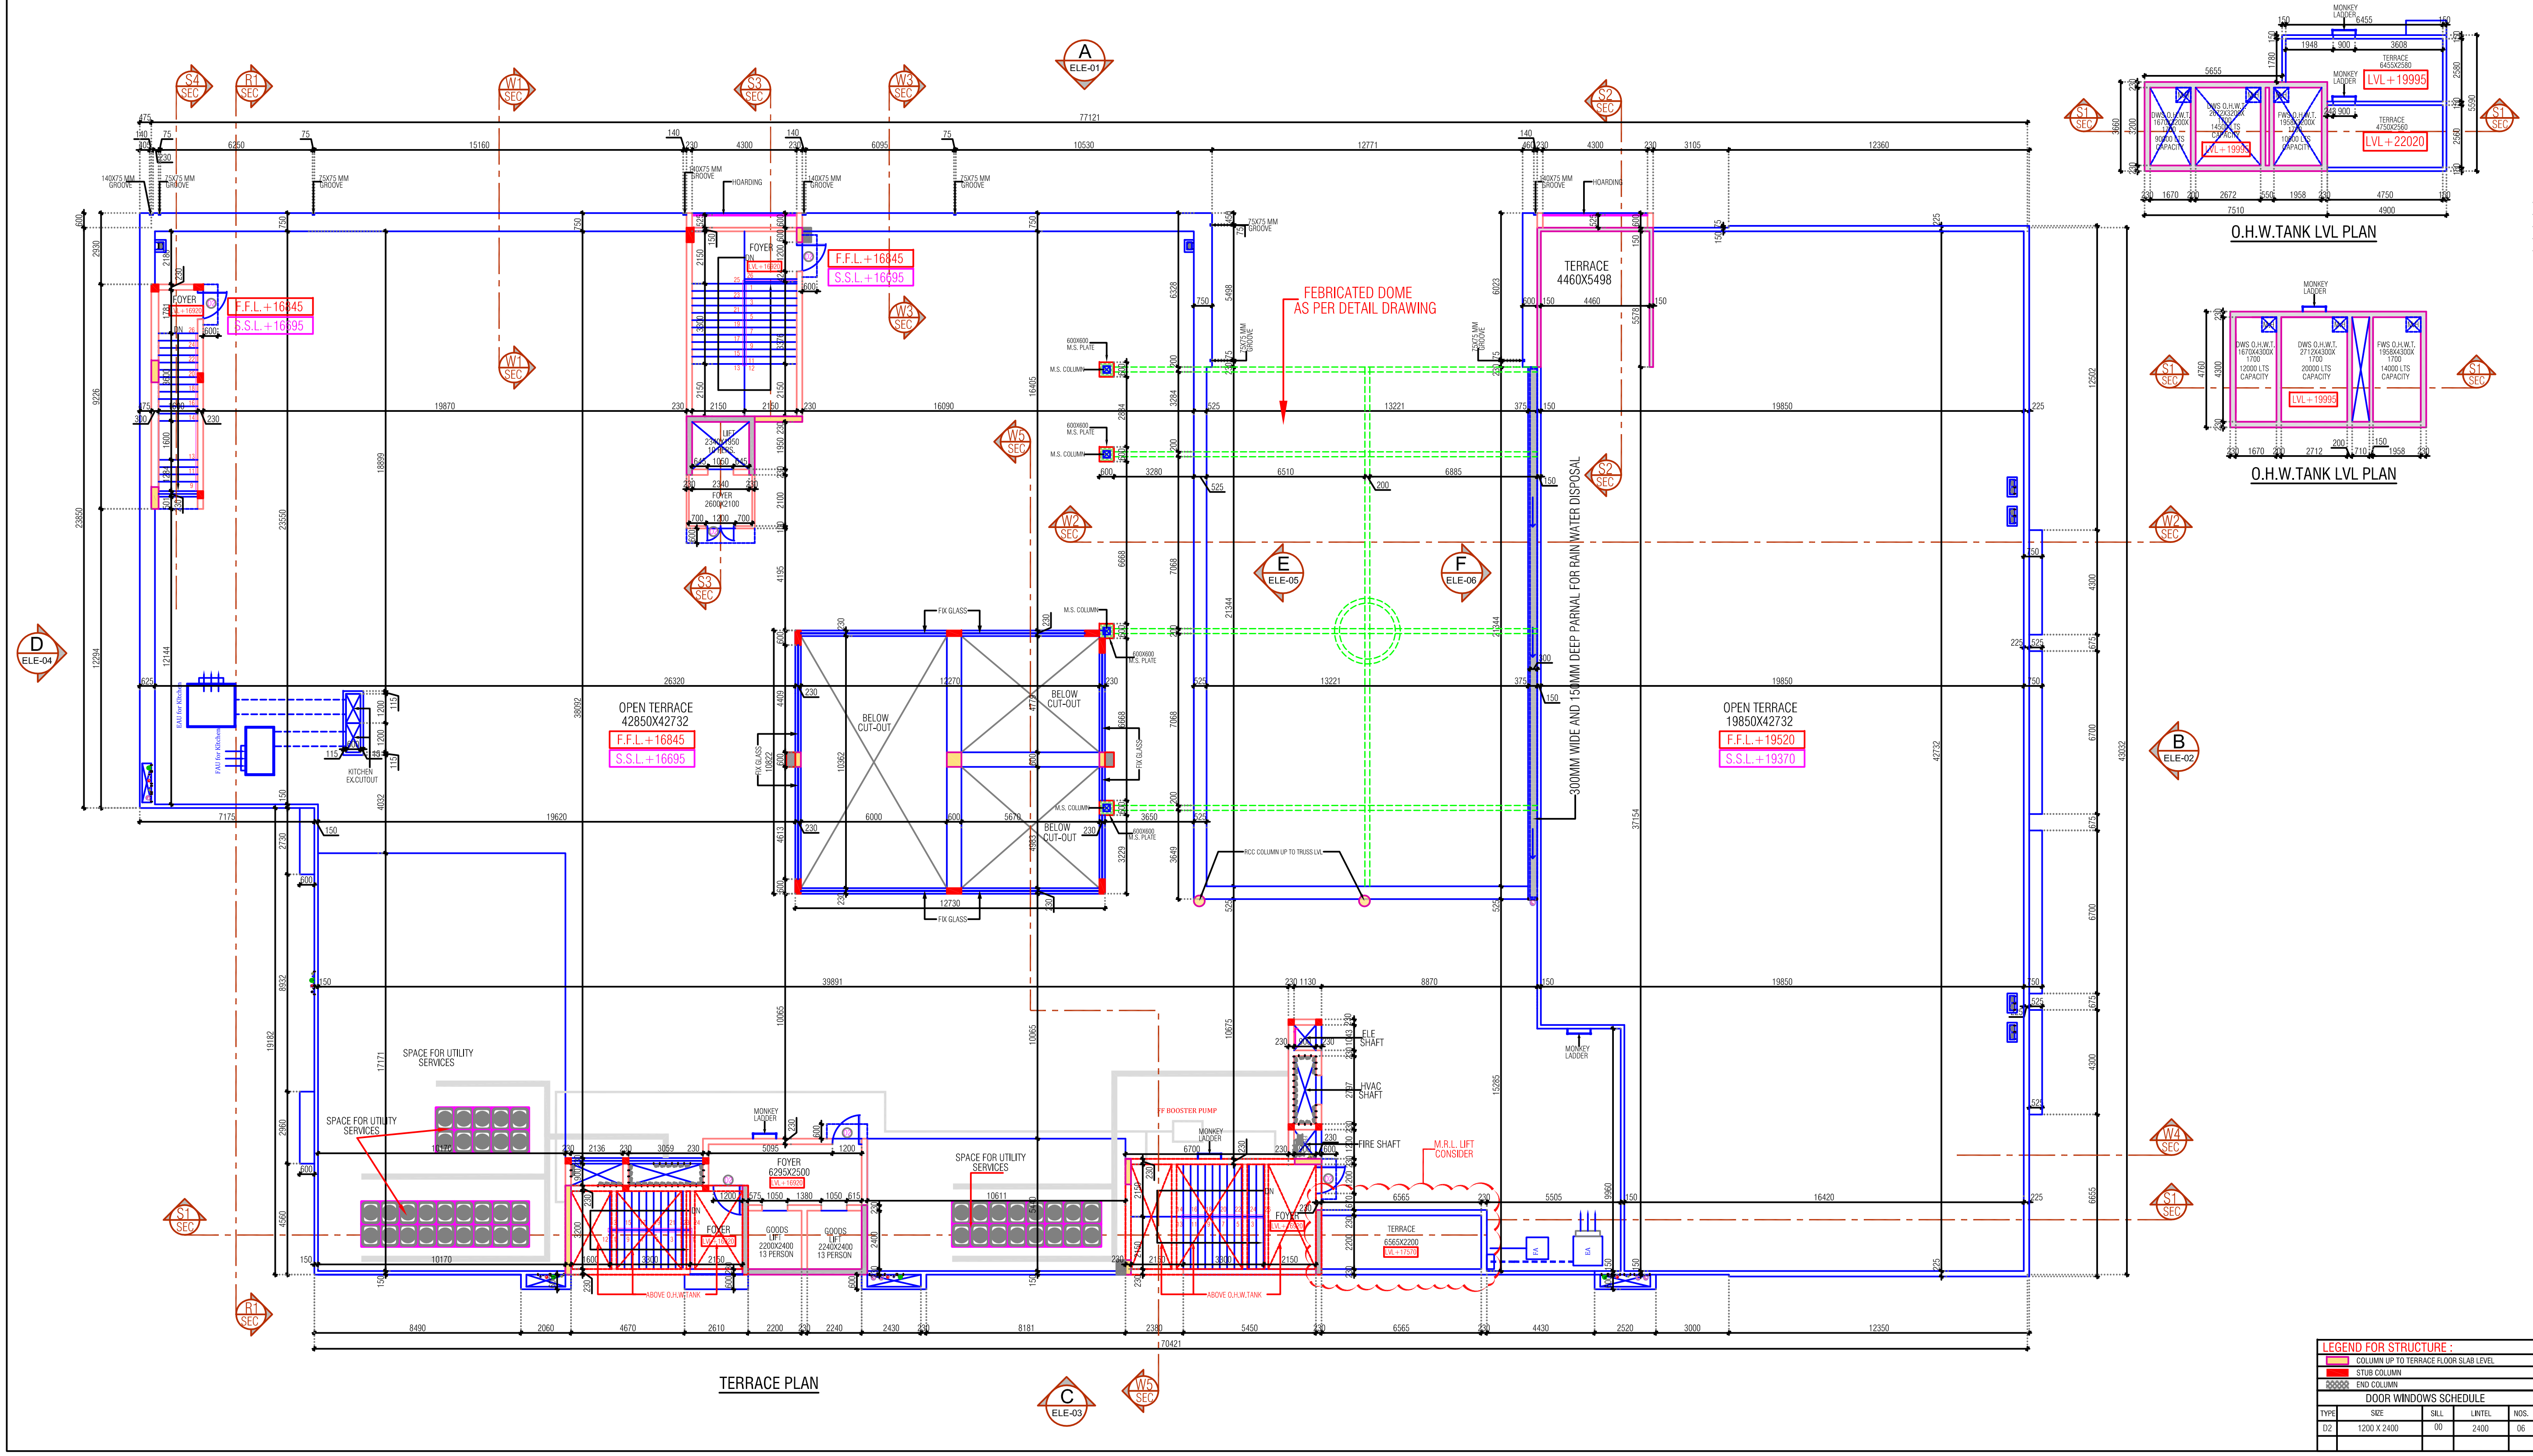

GENERAL NOTES:

1. COLUMN SIZE AS PER STRUCTURE DETAIL.
2. LIFT WELL SHOULD BE PROVIDE AS PER APPROVAL LIFT CONSULTANT & STRUCTURE DETAIL.
3. STAIR CASE AS PER DETAIL
4. RAILLING & PARAPET WALL AS PER DETAIL.
5. FOR DOOR & WINDOW REFER DRAWING
6. TOILET PIPES & SUNK REFAR TO ARCHITECTURE & CONSULTANT DRAWING. IN CASE THERE IS ANY DISCREPANCY BETWEEN ARCHITECTURAL DRAWINGS AND OTHER DRAWINGS, ARCHITECTURAL DRAWINGS SHOULD BE FOLLOWED.
7. ANY AMBIGUITY FOUND SHALL BE IMMEDIATELY BROUGHT TO THE NOTICE OF THE ARCHITECTS BEFORE COMMENCEMENT OF WORK.
8. DRIP MOULD SHOULD BE PROVIDED IN LINTLES OF ALL EXTERNAL OPENINGS.
9. ALL DIMENSIONS ARE TO BE READ AND NOT MEASURED.
10. ALL DIMENSIONS ARE IN MM.
11. REFER DETAIL DRAWINGS WHERE EVER RELEVANT;e.g. FOR THE CONSTRUCTION OF STAIRS,KITCHENS, TOILETS & RAILINGS.
12. LIFT MACHINE ROOM & OVER HEAD WATER TANK AS PER DETAIL.
13. SLEEVE AS/PER PLUMBING DETAIL.
14. SLEEVE AND ELECTRICAL CONDUIT AS/ELECTRICAL DETAIL.
15. ALL DIMENSIONS REQUIRE FINISHED DIMENSIONS PLEASE CONSIDER FINISHING MATERIAL THICKNESS DURING R.C.C. CASTING AND MASONRY PLASTER.
16. CROSS CHECK ALL ARCHITECTURAL PROJECTION, ALL DIMENSIONS,MARGIN WITH AUDA APPROVED PASSING DRAWING BEFORE EXECUTION OF THE WORK.
17. FOR GROUND DEVELOPMENT & INTERIOR DECORATION FOLLOW RESPECTIVE CONSULTANT'S DETAIL DRAWING.
18. GLASS DIVISION & GLAZING THICKNESS MAY BE CHANGE AS PER VENDER \ FACADE CONSULTANT'S DETAIL DRAWING.
19. 61.750M TO BE CONSIDERED AS ±0.00M (INTERNAL ROAD FFL LEVEL)

KEY PLAN :

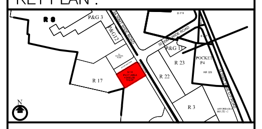

PRINTS ISSUED

Date	Rev.	Client	Site	Stru.	Plum.	Elec.	Office	Total	REMARK
13.12.22	R4	MAIL	MAIL	MAIL	MAIL	MAIL	MAIL	6	G.F.C.
21.01.23	R5	MAIL	MAIL	MAIL	MAIL	MAIL	MAIL	6	G.F.C.

DESCRIPTION OF BUILDING

Rev	Description	Date	Drawn	Checked
R 05	MARK AREA REVISED AS PER CLIENT REQUIREMENT.	21-01-23	SANJAY	NAVNEET

REVISIONS / ISSUE

THIS DRAWING MUST NOT BE REPRODUCED IN WHOLE OR IN PART WITHOUT THE PRIOR APPROVAL OF CONSULTANTS

CLIENT :

DISCIPLINE :

ARCHITECTURAL

DRAWING TITLE :

TERRACE & O.H.W.TANK
ARCHITECTURAL PLAN

Project code	Discipline code	Drawing serial no.			Drawing revision no.		
N-EMACC02	A	1	6	0	R	0	5

Project Ref No.				N
Original Scale 1:200	Drawn	Checked	Authorised	
	Date: 26.04.22	Date:28.04.22	Date: 28.04.22	CUSTOM

LEGEND FOR STRUCTURE :

🟨	COLUMN UP TO TERRACE FLOOR SLAB LEVEL
🟥	STUB COLUMN
▨	END COLUMN

DOOR WINDOWS SCHEDULE

TYPE	SIZE	SILL	LINTEL	NOS.
D2	1200 X 2400	00	2400	06