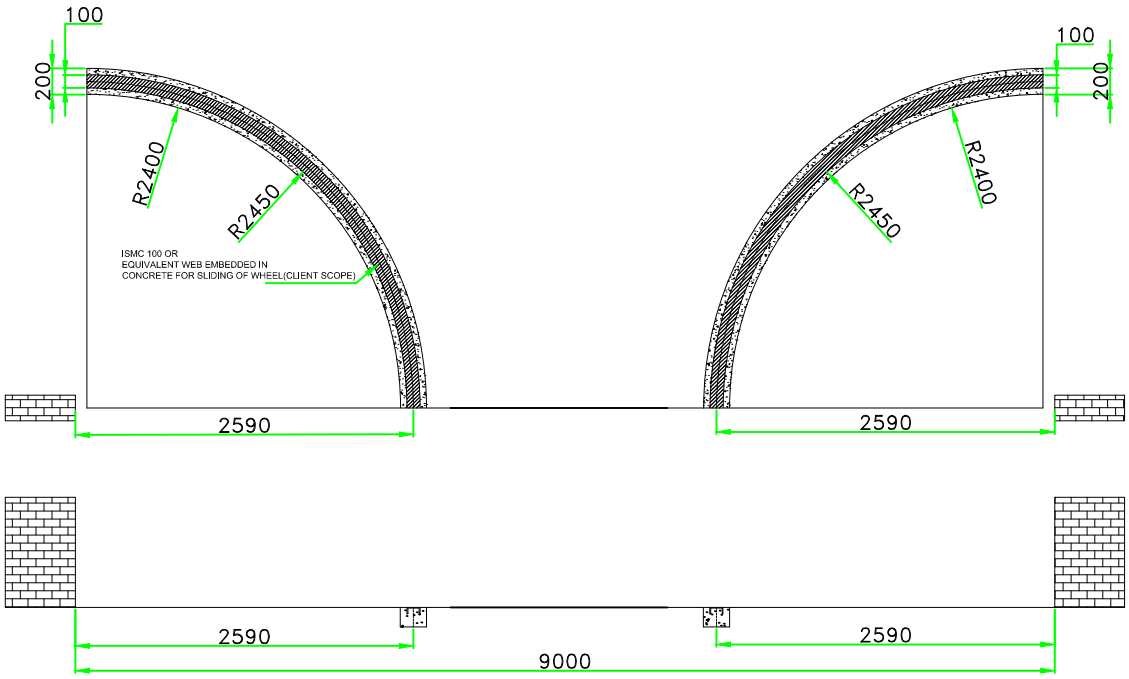


R01	CLEAR WIDTH CHANGED TO 9000	S.M.S.	30.12.20
REV.	DESCRIPTION	DRAWN	DATE

This drawing & designing is the property of NIHVA TECHNOLOGIES. Not be sold or copy to any other concern.

TITLE				
SWING GATE FOUNDATION DRAWING				NIHVA TECHNOLOGY PVT. LTD. PUNE
	NAME	SIGN	DATE	Tel : 020 66304033
DRAWN	SURAJ		13.12.2018	Website:- www.nihva.com Email:- info@nihva.com
CHECK	P.A		13.12.2018	CLIENT - INDAMER TECHNICS PVT. LTD.
APPROVAL	R.D		13.12.2018	PROJECT -
If any queries contact : design@nihva.com				SITE - NAGPUR
ALL DIMENSION ARE IN mm				DWG. NO. : NIHVA/18-19/0204/R01 REV. : R01
				SCALE: NTS WT: SHEET: