




SIDE VIEW

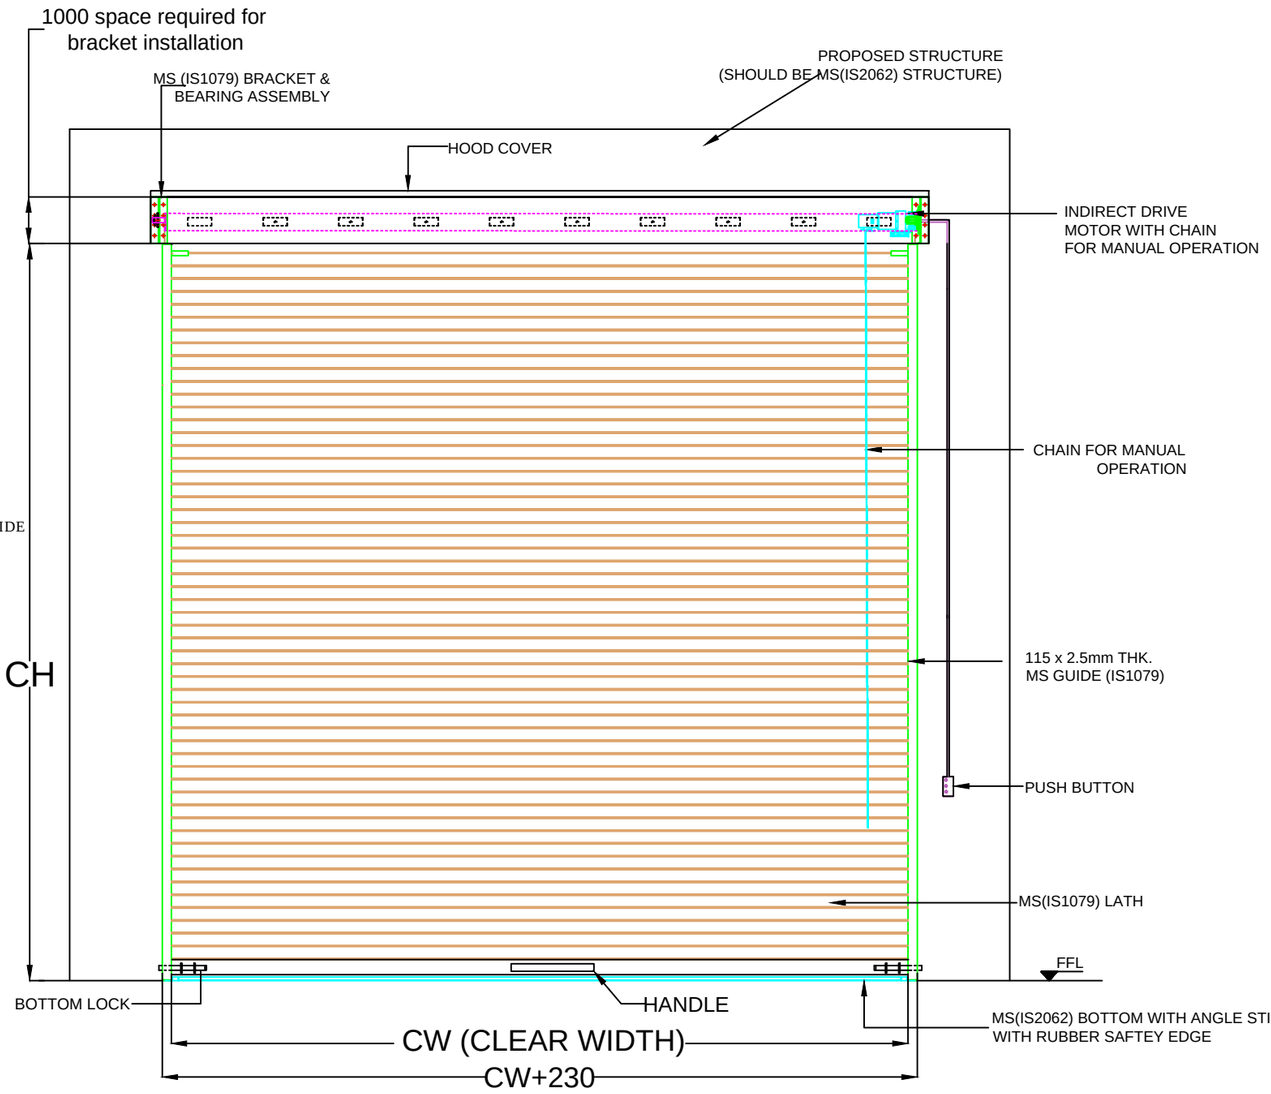


ELEVATION

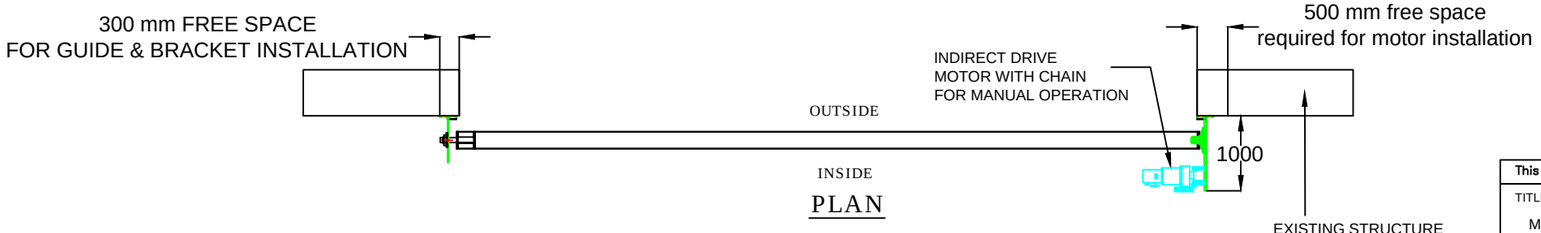

PLAN

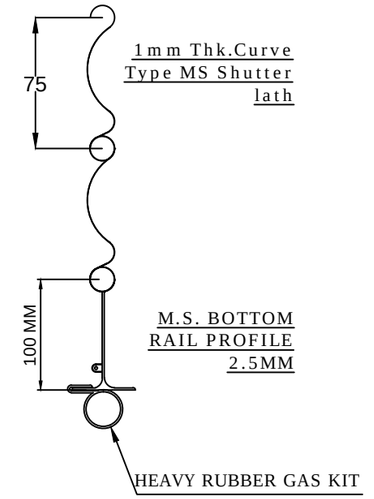

M.S. BOTTOM RAIL PROFILE 2.5MM

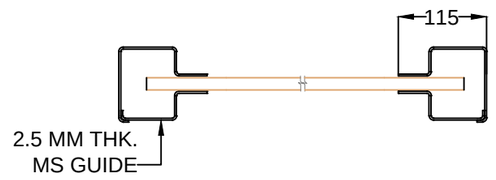

COLOR:- 1.RAL7035(LIGHT GRAY) ☐
2.RAL9016(TRAFFIC WHITE) ☐
3.RAL5005(SIGNAL BLUE) ☐
4.RAL7004(SIGNAL GRAY) ☐
5.RAL5015(SKY BLUE) ☑

CLEAR WIDTH (CW)	CLEAR HEIGHT (CH)	GRILL SIZE (CW) X (CH)	QUANTITY
7000	7000	-	04

NOTE:-
1. REQUIRED STRUCTURE FOR ROLLING SHUTTER SHALL BE IN NIHVA SCOPE.
2. ALL REQUIRED CIVIL WORK IN CLIENT SCOPE.
3. 3 PHASE POWER SUPPLY SHOULD BE PROVIDED BY CLIENT.
4. MOTOR : JIELONG , 1.5 TON, 3PH

Rev 01:- 04/02/2022
1. Added IS material specification for MS material.
2. Added motor capacity details.
3. Mentioned height of grill.
4. Mentioned RAL code.

Rev 02:- 10/02/ 2022
1. Grill removed.

This drawing & designing is the property of NIHVA TECHNOLOGIES. Not to be sold or copied to any other concern.

TITLE: MOTORIZED ROLLING SHUTTER

NIHVA TECHNOLOGIES PVT. LTD.
NIHVA TECHNOLOGIES PVT. LTD. PUNE
Tel : 020 66304033
Email:- info@nihva.com
Website:- www.nihva.com

	NAME	SIGN	DATE
DRAWN	G.P.		13/09/21
CHECK	A.K.		13/09/21
APPROVAL	V.T.		13/09/21

CLIENT -REWARD CONSTRUCTION
PROJECT -
SITE - INDAPUR
If any queries contact : design@nihva.com
DWG. NO. : NIHVA/21-22/0231 REV. - 02
ALL DIMENSION ARE IN mm
SCALE: NTS WT: SHEET: 01 OF 01