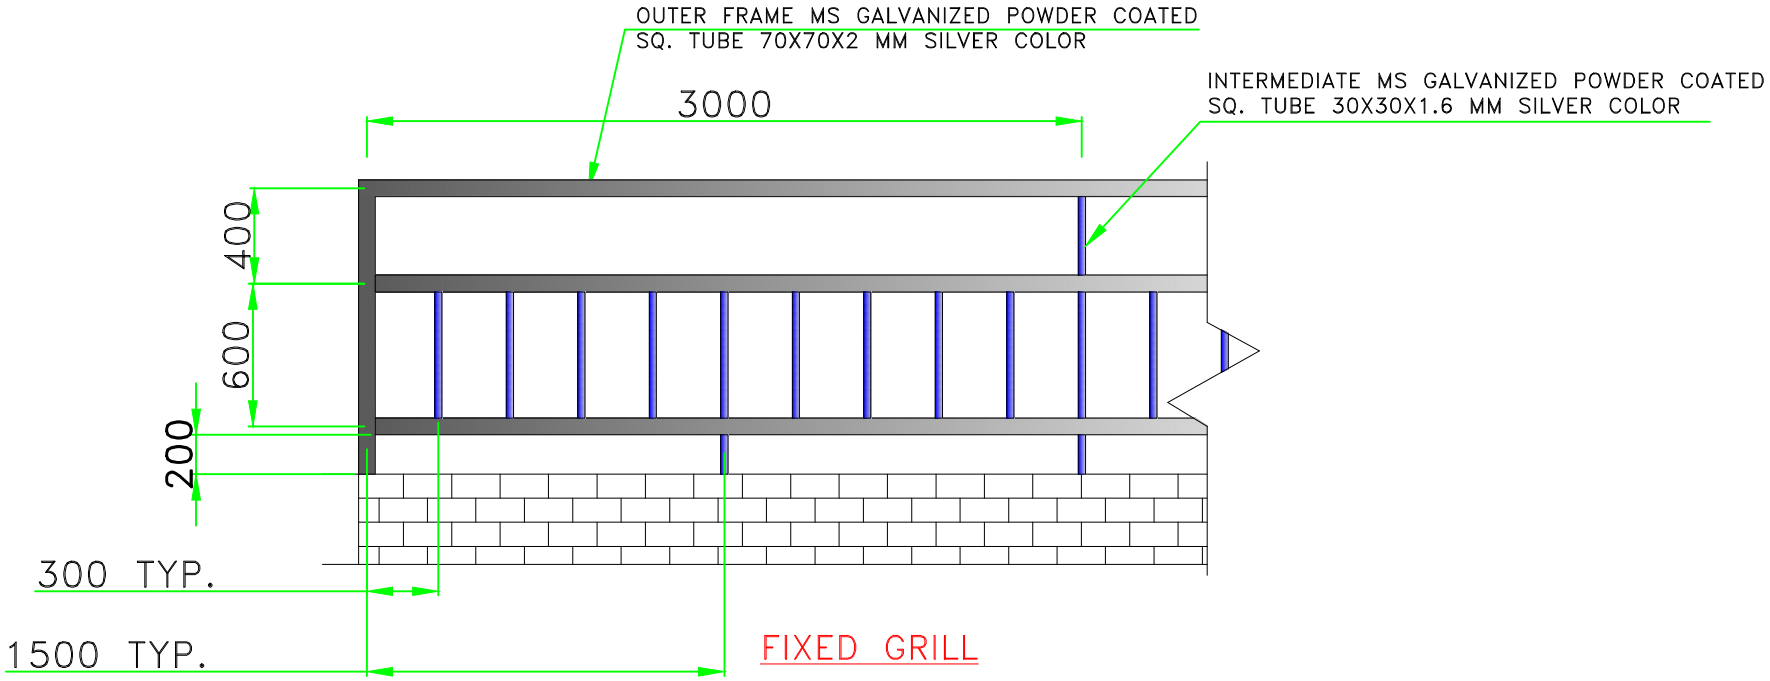


OUTER FRAME = 70 X 70 X 2 mm
INNER FRAME = 30 X 30 X 1.6 mm
ONE FRAME LENGTH = 3 METER
TOTAL LENGTH OF FENCEING

LOCATION	FG 2	FG 3	FG 4
LENGTH	19650	19600	7500
WEIGHT SS	375KG.	375KG.	150KG.
WEIGHT MS	500KG.	500KG.	180KG.

APPROXIMATE WEIGHT

This drawing & designing is the property of NIHVA TECHNOLOGIES. Not be sold or copy to any other concern.

TITLE

FENCING

CLIENT APPROVAL

ALL DIMENSION ARE IN mm

	SIGN	DATE
DRAWN	ABHIJIT	10/11/14
CHECK	ANIL	10/11/14
REV.	04	
APPRD.		
MFG		
Ref. No.		

NIHVA TECHNOLOGIES PVT. LTD.

NIHVA TECHNOLOGY PVT. LTD. PUNE
Tel : 020 66304033
Email:- info@nihva.com
Website:- www.nihva.com

CLIENT - JSW

PROJECT -

SITE - KHED

DWG. NO. - NVA/JSW/D1/ 3 of 3

SCALE: 01 | WT: | SHEET: 01

If any queries contact : projects@nihva.com