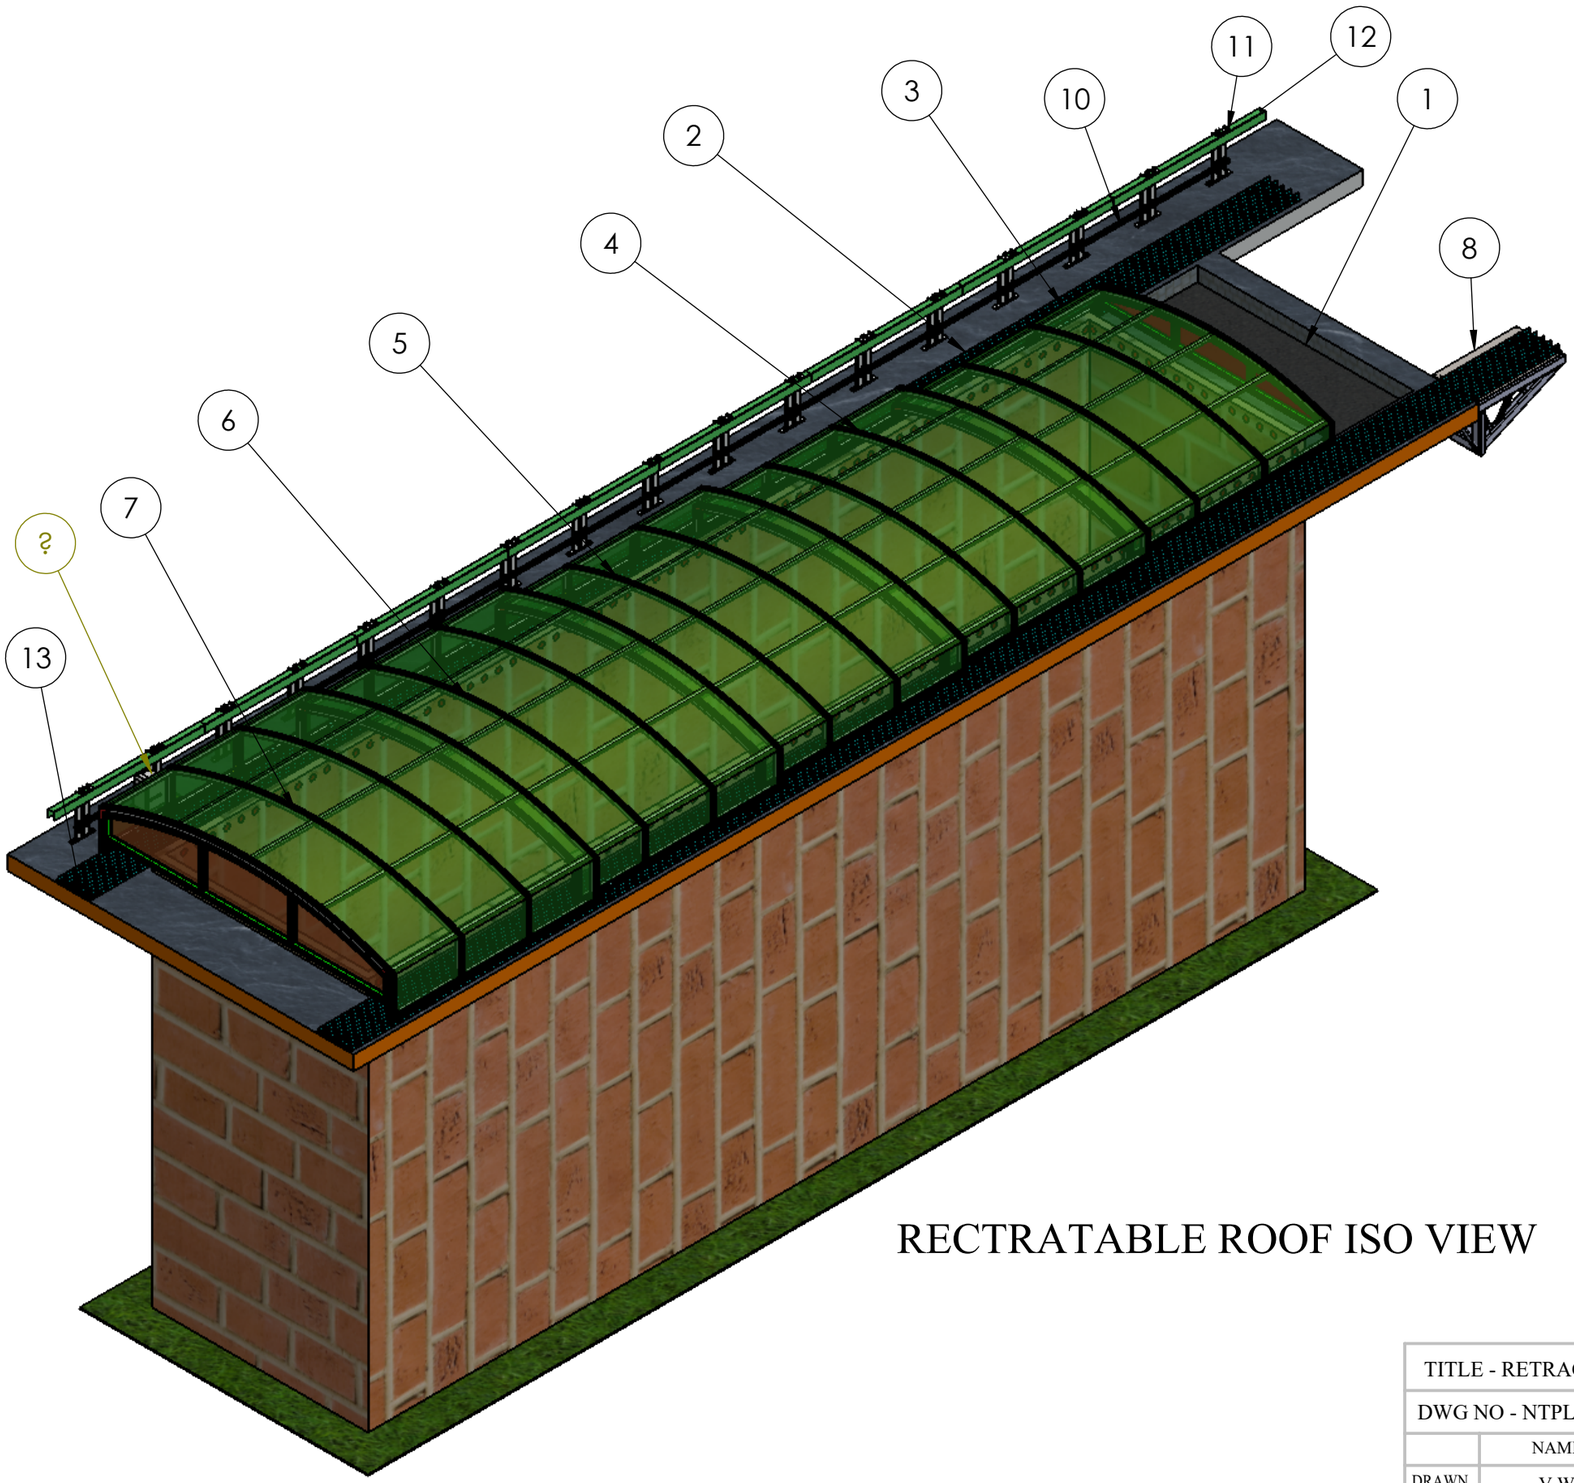


RECTRATABLE ROOF ISO VIEW

ITEM NO.	PART NUMBER	DESCRIPTION	QTY.
1	VIJAY CIVIL BASE		1
2	GUIDE RAILS-T75-1B	STD (16.8 M LENGTH)	10
3	VIJAY_PANEL NO 1 ASM		1
4	PANEL NO 2 ASM		1
5	PANEL NO 3 ASM		1
6	PANEL NO 4 ASM		1
7	PANEL NO 5 ASM		1
8	MB REC TUBE STRUCTURE		1
9	MOTOR MTG BRACKET NICE 1.8T	MS	1
10	VIJAY RACK	STD (M4 RACK, 30x8x1000 mm, ZINC COATED WITH SPACERS AND SCREWS.)	16
11	VIJAY_Rack support_575	STD (LOOSE PART)	17
12	VIJAY BUSBAR FLASHER	STD (LOOSE PART)	8
13	VIJAY Anchor Bolt M10x75	STD	160
14	NICE RB 1.8T		1

TITLE - RETRACTABLE ROOF

DWG NO - NTPL-000-PM-001-00-00-00

NIHVA Technologies Pvt. Ltd.

NIHVA TECHNOLOGIES PVT.LTD.PUNE

Website - www.nihva.com

	NAME	SIGNATURE	DATE
DRAWN	V.W		07-04-2025
CHK'D	S.W.		07-04-2025
APPV'D	V.T.		07-04-2025

PROJECT NO - NTPL-000-PM

PRODUCT - RETRACTABLE ROOF

SITE LOCATION - GUJARAT

if any queries contact - supportautomation@nihva.com

REVISION -


QTY - 1

ALL DIMENSION ARE IN mm


A3


SCALE


SHEET 1 OF 28

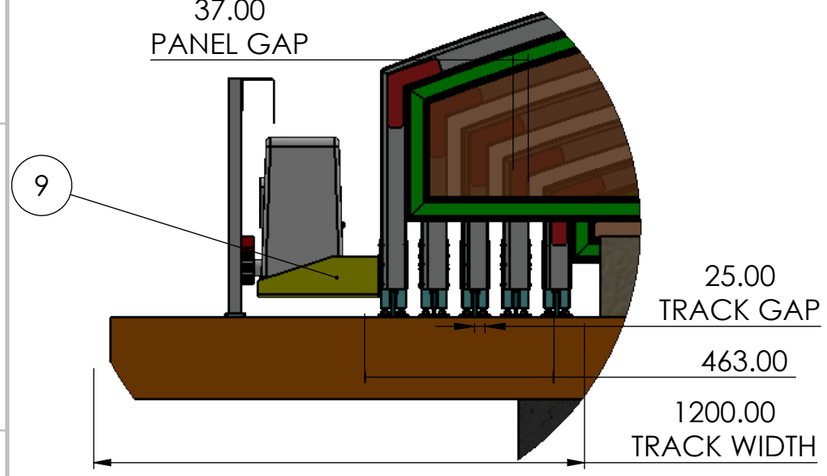

DETAIL B
SCALE 1 : 15

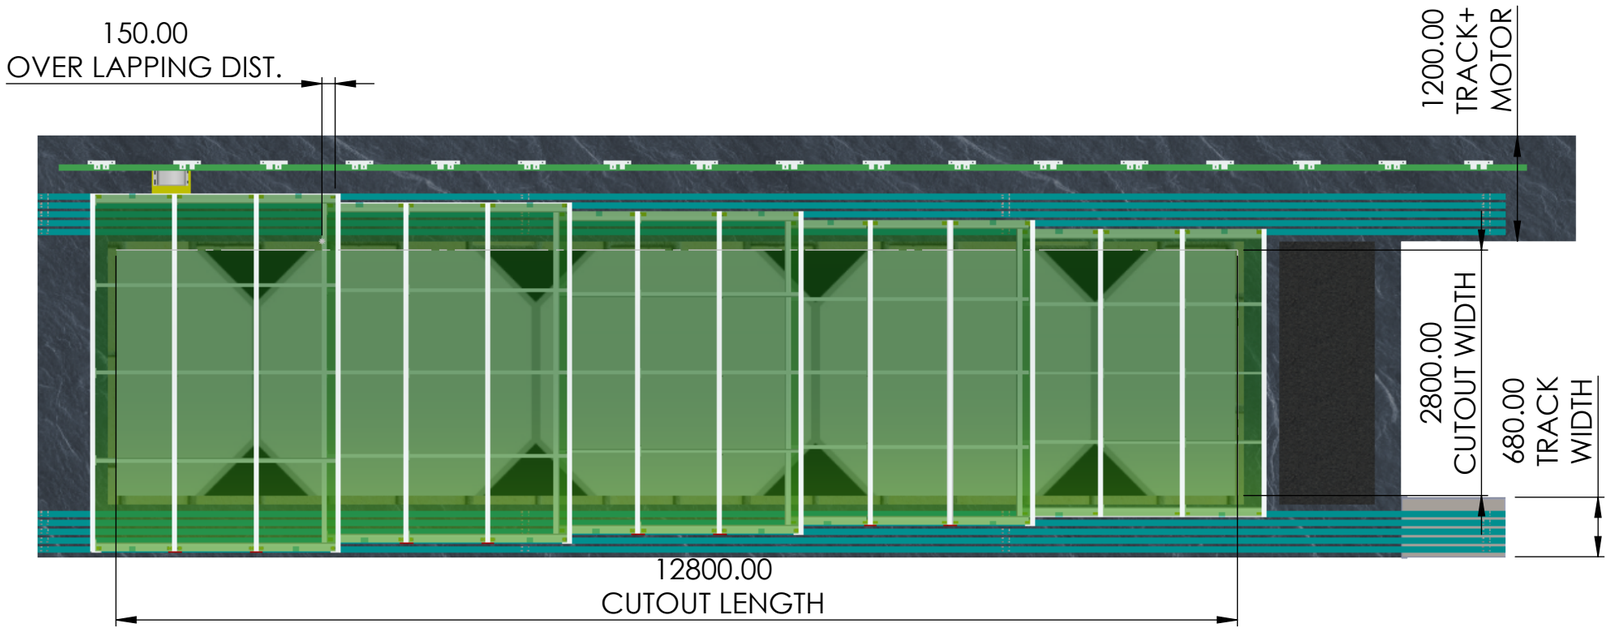

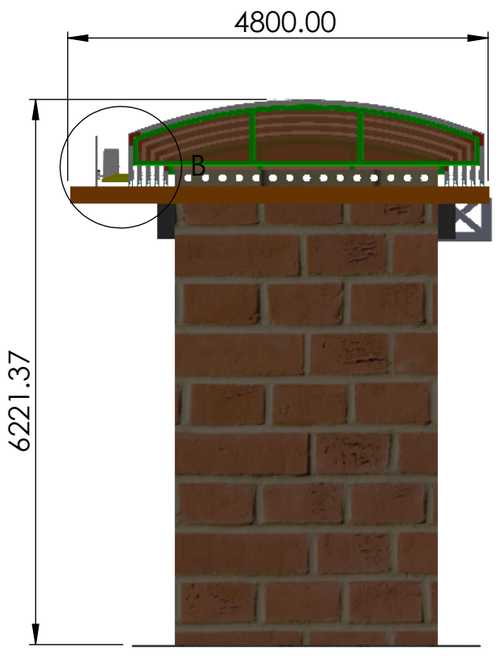


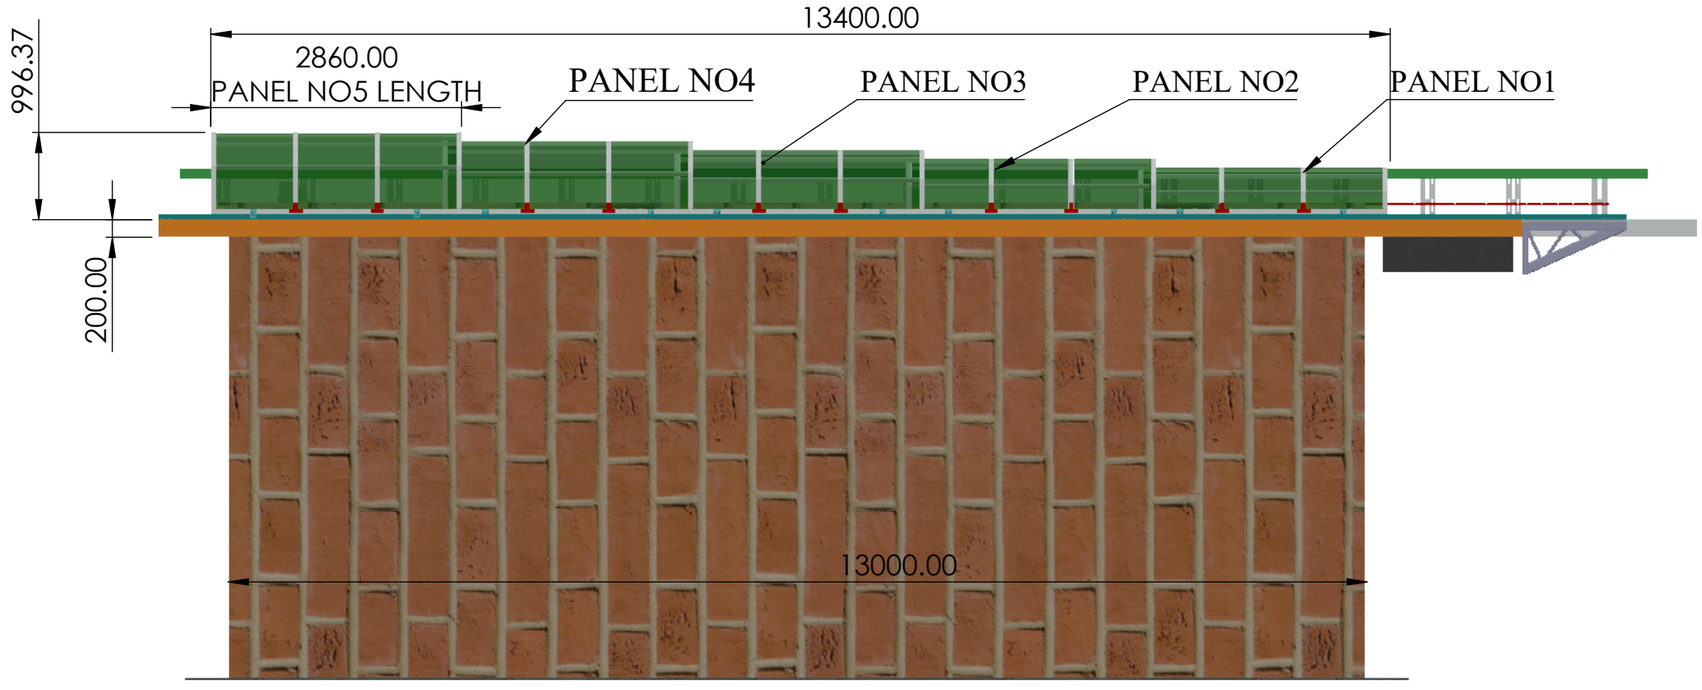


RETRACTABLE ROOF

TITLE - RETRACTABLE ROOF				NIHVA TECHNOLOGIES PVT.LTD.PUNE
DWG NO - NTPL-000-PM-001-01-00-00				Website - www.nihva.com
	NAME	SIGNATURE	DATE	PROJECT NO - NTPL-000-PM
DRAWN	V.W		07-04-2025	PRODUCT - RETRACTABLE ROOF
CHK'D	S.W.		07-04-2025	SITE LOCATION - GUJARAT
APPV'D	V.T.		07-04-2025	
if any queries contact - supportautomation@nihva.com				REVISION - QTY - 1
ALL DIMENSION ARE IN mm			A3	SCALE SHEET 2 OF 28


ITEM NO.	PART NUMBER	DESCRIPTION	QTY.
1	GUIDE RAILS-T75-1B	STD (16800 MM LENGTH)	10

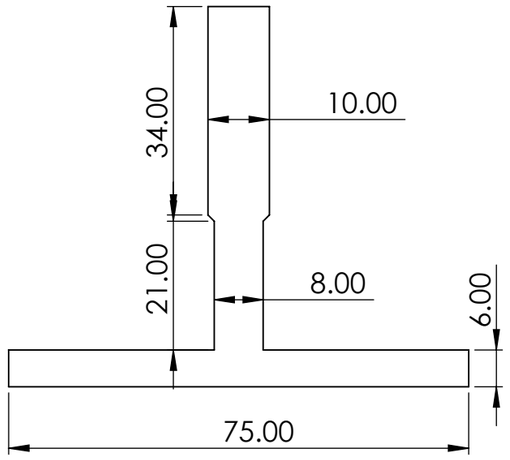


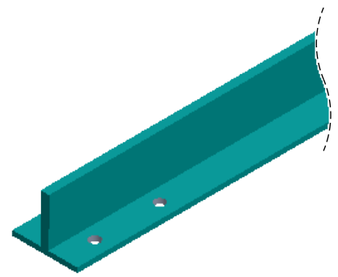


TITLE - RETRACTABLE ROOF				NIHVA TECHNOLOGIES PVT.LTD.PUNE
DWG NO - NTPL-000-PM-001-02-00-02				Website - www.nihva.com
	NAME	SIGNATURE	DATE	PROJECT NO - NTPL-000-PM
DRAWN	V.W		07-04-2025	PRODUCT - RETRACTABLE ROOF
CHK'D	S.W.		07-04-2025	SITE LOCATION - GUJARAT
APPV'D	V.T.		07-04-2025	
if any queries contact - supportautomation@nihva.com				REVISION - QTY - 1
ALL DIMENSION ARE IN mm		A3		SCALE SHEET 3 OF 28

ITEM NO.	PART NUMBER	DESCRIPTION	QTY.
1	PANEL NO 1		1
2	PANEL NO1 ENCLOSER		1
3	VIJAY_BEARING BLOCK ASM WITH SHOULDER BOLT	SLIDING BLOCK	20
4	AL Support tube SQ TUBE 40X40X1.5 MM L-853.33 MM	AL INTERMEDIAT SUPPORT TUBE	75
5	VIJAY_Rivet_iso_15977_4_x_16_0	RIVET M4X16	60
6	T PLATE	JOINING PLATE	8
7	L ANGLE PLATE	JOINING PLATE	12
8	L PALTE	JOINING PLATE	8
9	VIJAY_L ANGLE WELDING PLATE	ALUMINIUM JOINING PLATE	4
10	PANEL NO1 POLYCARBONET SHEET		3
11	PANEL NO1 ENCLOSER POLYCARBONET SHEET		1

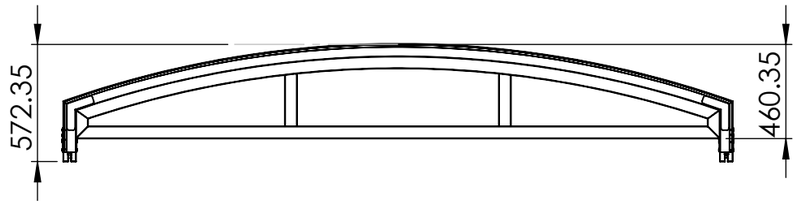


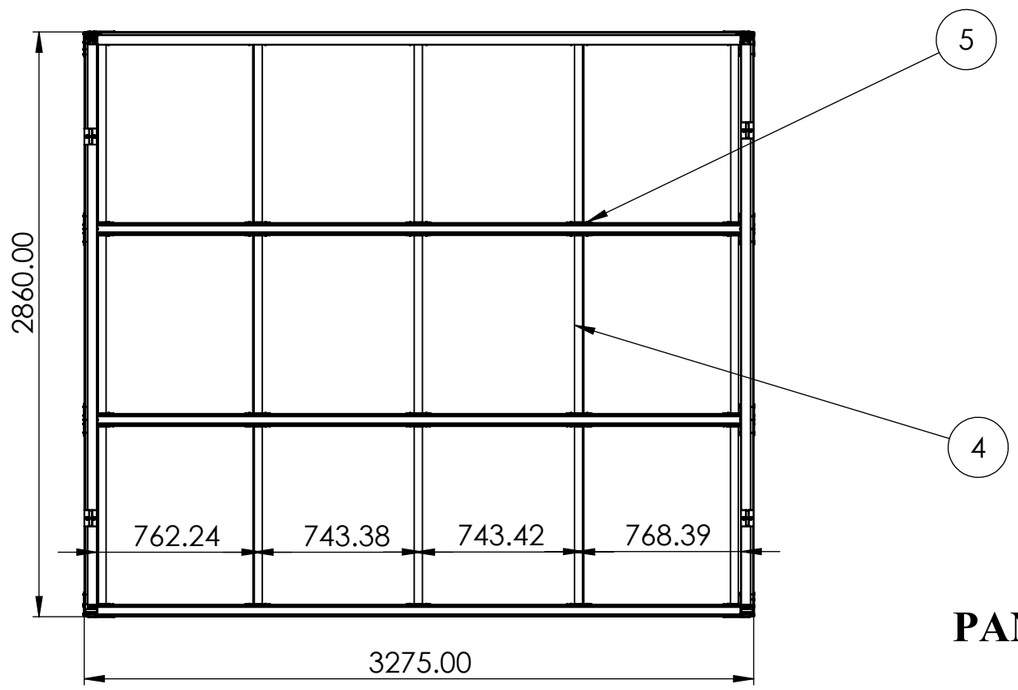


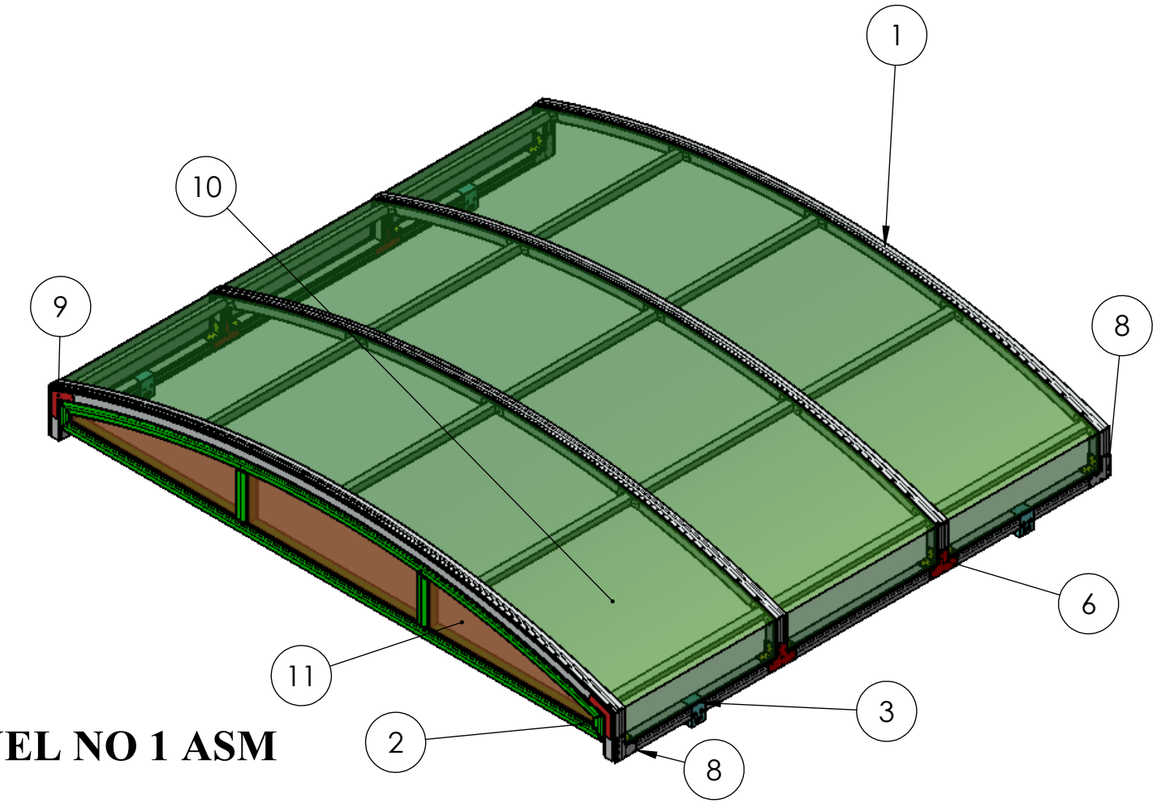


PANEL NO 1 ASM


TITLE - RETRACTABLE ROOF				NIHVA TECHNOLOGIES PVT.LTD.PUNE
DWG NO - NTPL-000-PM-001-03-00-03				Website - www.nihva.com
	NAME	SIGNATURE	DATE	PROJECT NO - NTPL-000-PM
DRAWN	V.W		07-04-2025	PRODUCT - RETRACTABLE ROOF
CHK'D	S.W.		07-04-2025	SITE LOCATION - GUJARAT
APPV'D	V.T.		07-04-2025	
if any queries contact - supportautomation@nihva.com				REVISION - / QTY - 1
ALL DIMENSION ARE IN mm			A3	SCALE / SHEET 4 OF 28

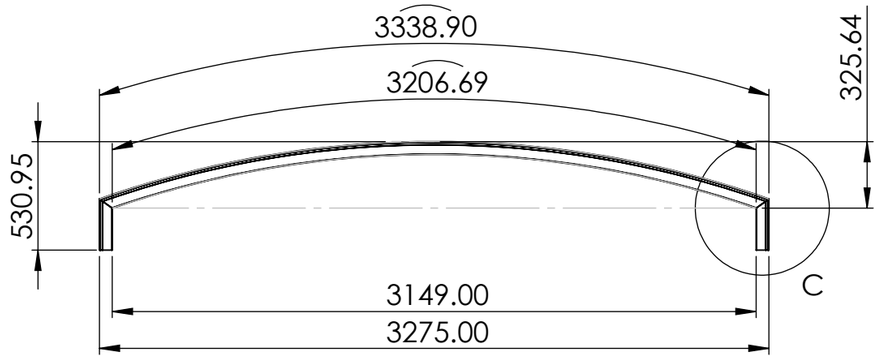

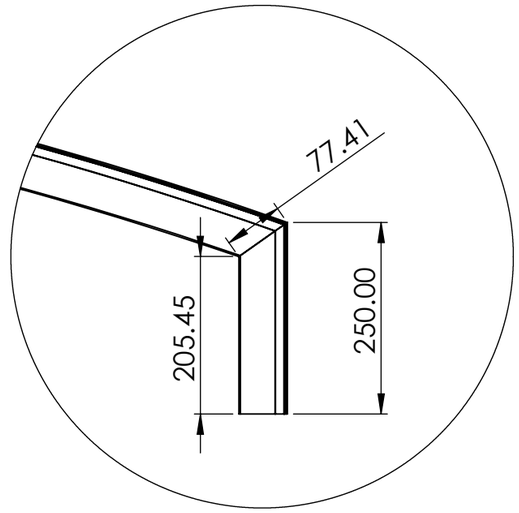

DETAIL C
SCALE 1 : 8

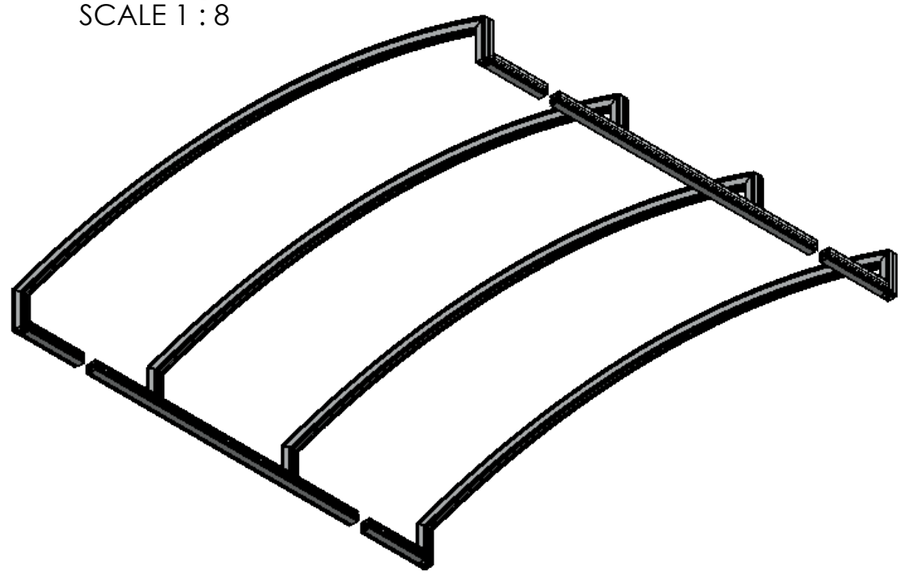


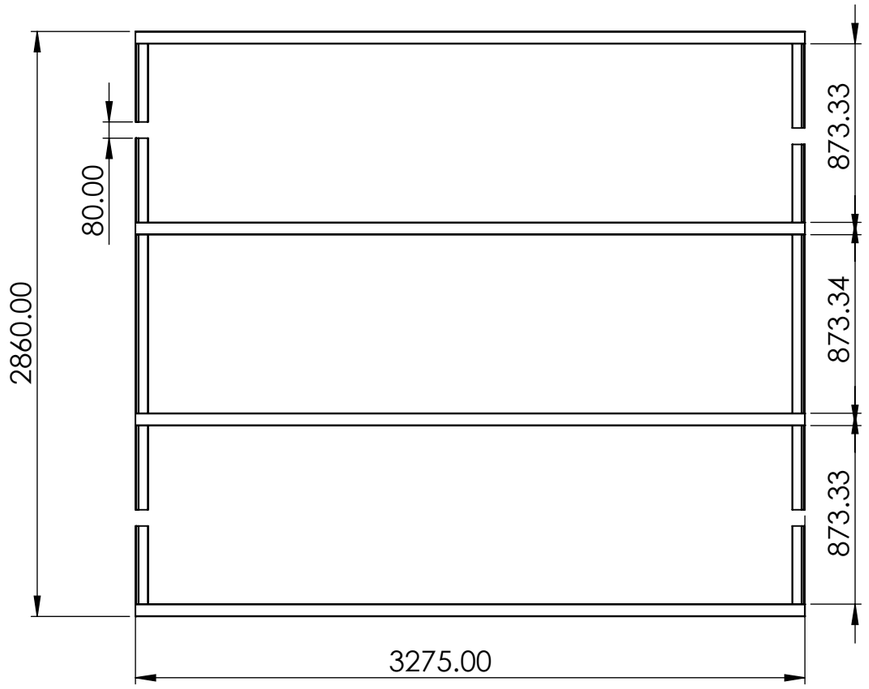


PANEL NO 1


TITLE - RETRACTABLE ROOF				NIHVA TECHNOLOGIES PVT.LTD.PUNE
DWG NO - NTPL-000-PM-001-03-01-00				Website - www.nihva.com
	NAME	SIGNATURE	DATE	PROJECT NO - NTPL-000-PM
DRAWN	V.W		07-04-2025	PRODUCT - RETRACTABLE ROOF
CHK'D	S.W.		07-04-2025	SITE LOCATION - GUJARAT
APPV'D	V.T.		07-04-2025	
if any queries contact - supportautomation@nihva.com				REVISION - QTY - 1
ALL DIMENSION ARE IN mm		A3		SCALE SHEET 5 OF 28

ITEM NO.	PART NUMBER	DESCRIPTION	QTY.
1	PANEL NO1 ENCLOSER	ALUMINIUM ALLOY 6063 T-4	1

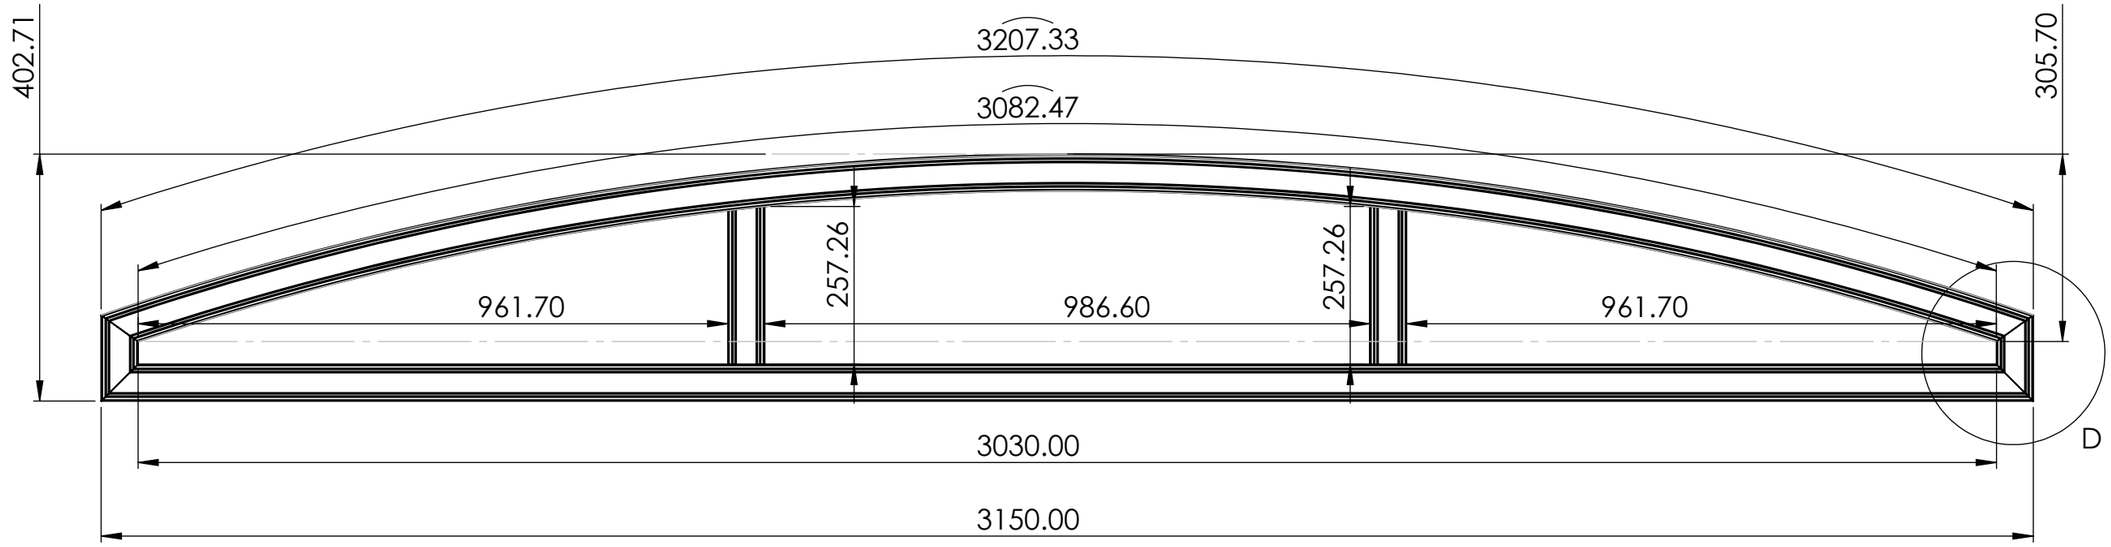

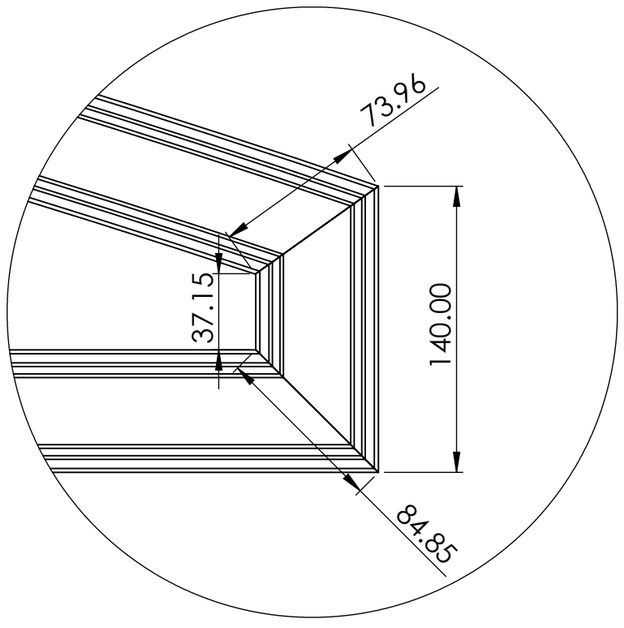



DETAIL D
SCALE 1 : 3

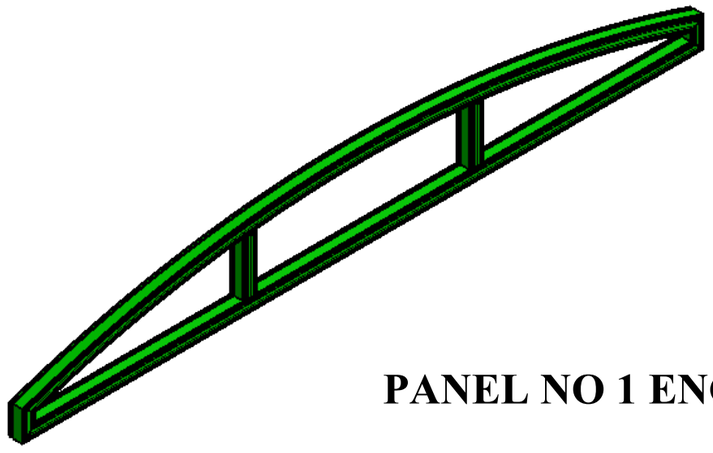


PANEL NO 1 ENCLOER

TITLE - RETRACTABLE ROOF				NIHVA TECHNOLOGIES PVT.LTD.PUNE Website - www.nihva.com
DWG NO - NTPL-000-PM-001-03-02-00				
	NAME	SIGNATURE	DATE	PROJECT NO - NTPL-000-PM
DRAWN	V.W		07-04-2025	PRODUCT - RETRACTABLE ROOF
CHK'D	S.W.		07-04-2025	SITE LOCATION - GUJARAT
APPV'D	V.T.		07-04-2025	
if any queries contact - supportautomation@nihva.com				REVISION - QTY - 1
ALL DIMENSION ARE IN mm		A3		SCALE SHEET 6 OF 28

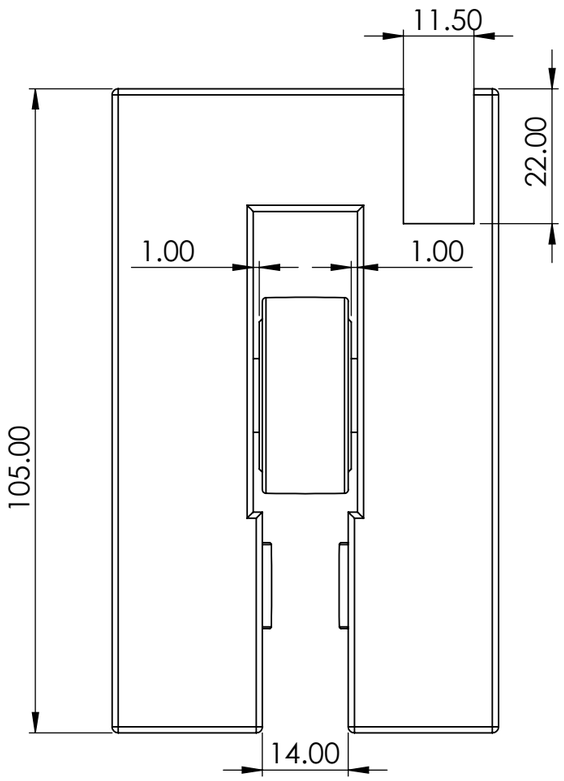


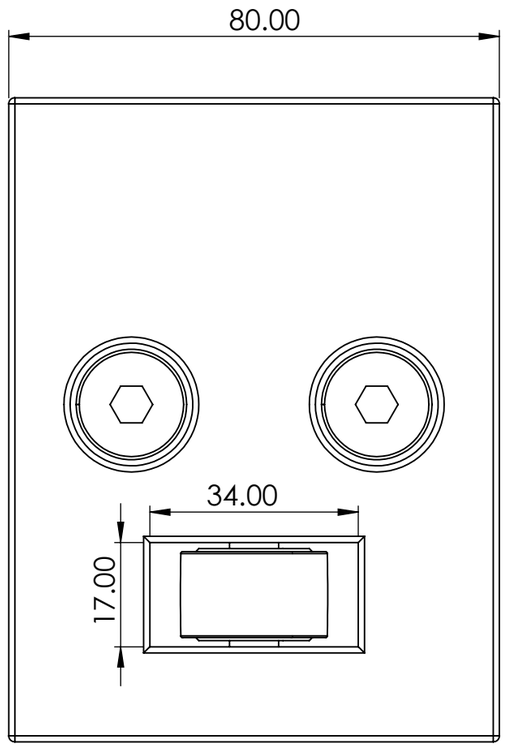

ITEM NO.	PART NUMBER	DESCRIPTION	QTY.
1	BEARING BLOCK (T75-1B)	80X105X63 MM (VMC PART)	20
2	SKF_NATR 12	BRG(STD)	40
3	SKF_NATR 8	BRG(STD)	40
4	MANUSH BHAI VIJAY SHOULDER BOLT NATR 12		40
5	ISO 7379 - 8 x 30 --- N		40

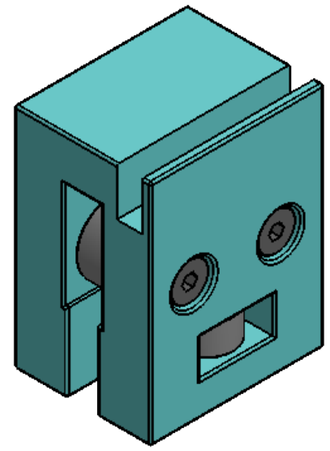



BEARING BLOCK ASM

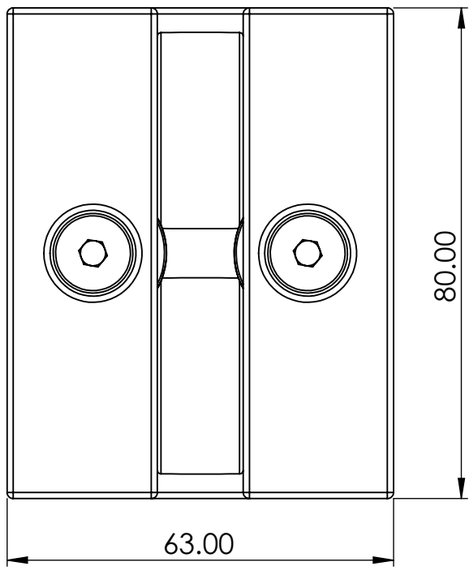



NOTE
FOR ALL PANEL THIS BEARING BLOCK ASSEMBY IS USED
VMC MACHINING

TITLE - RETRACTABLE ROOF				NIHVA TECHNOLOGIES PVT.LTD.PUNE
DWG NO - NTPL-000-PM-001-03-03-00				Website - www.nihva.com
	NAME	SIGNATURE	DATE	PROJECT NO - NTPL-000-PM
DRAWN	V.W		07-04-2025	PRODUCT - RETRACTABLE ROOF
CHK'D	S.W.		07-04-2025	SITE LOCATION - GUJARAT
APPV'D	V.T.		07-04-2025	
if any queries contact - supportautomation@nihva.com				REVISION - QTY - 1
ALL DIMENSION ARE IN mm		A3		SCALE SHEET 7 OF 28

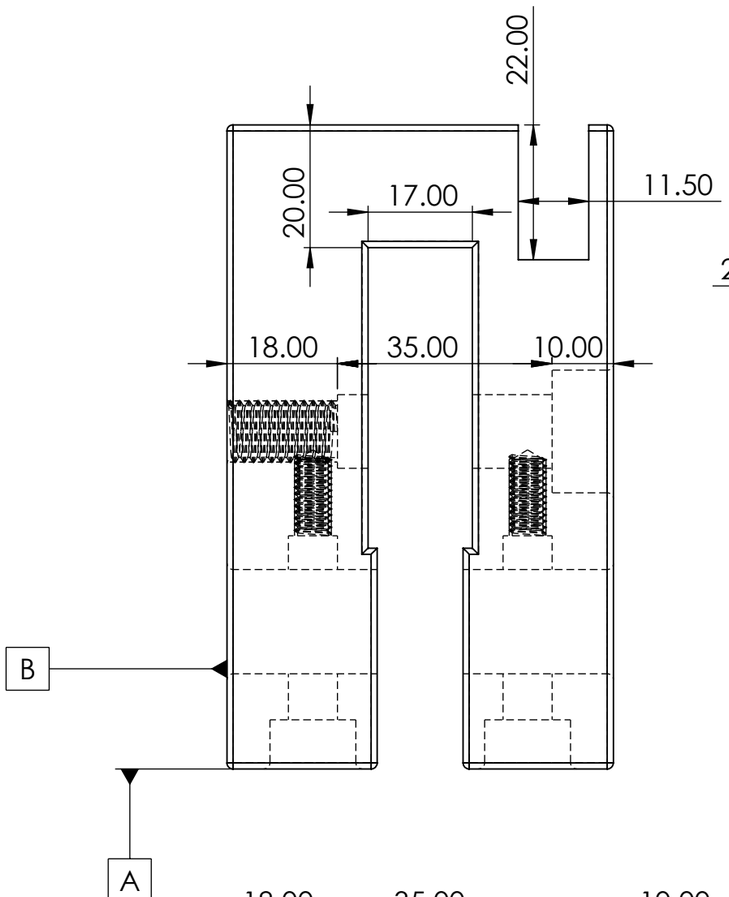

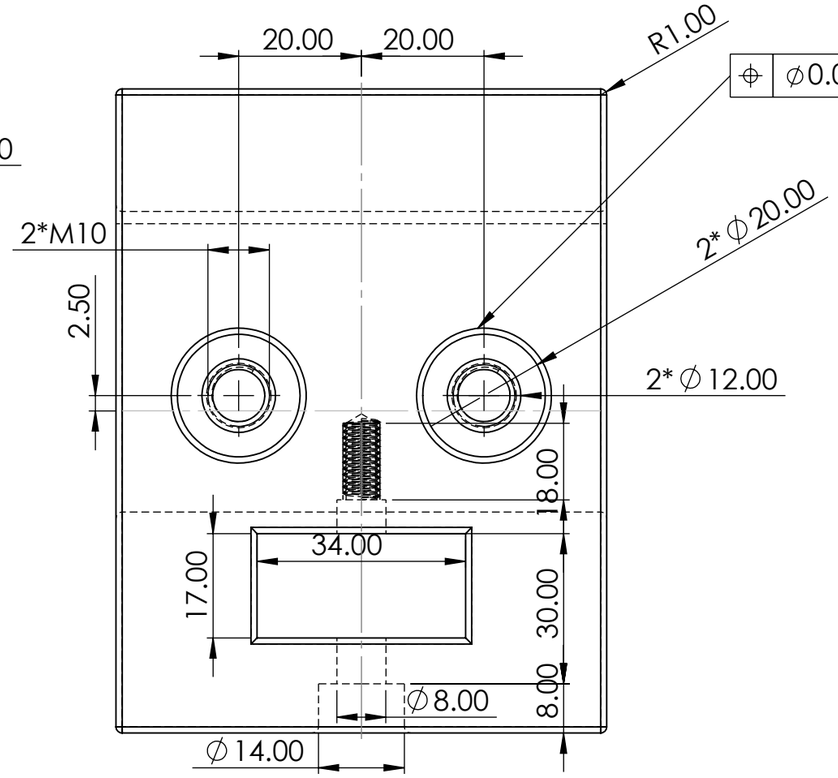

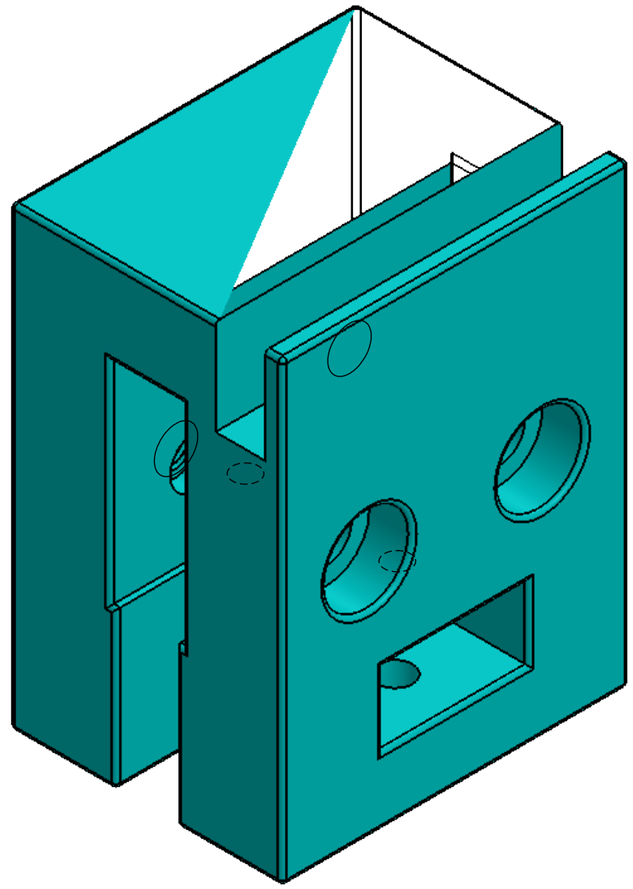

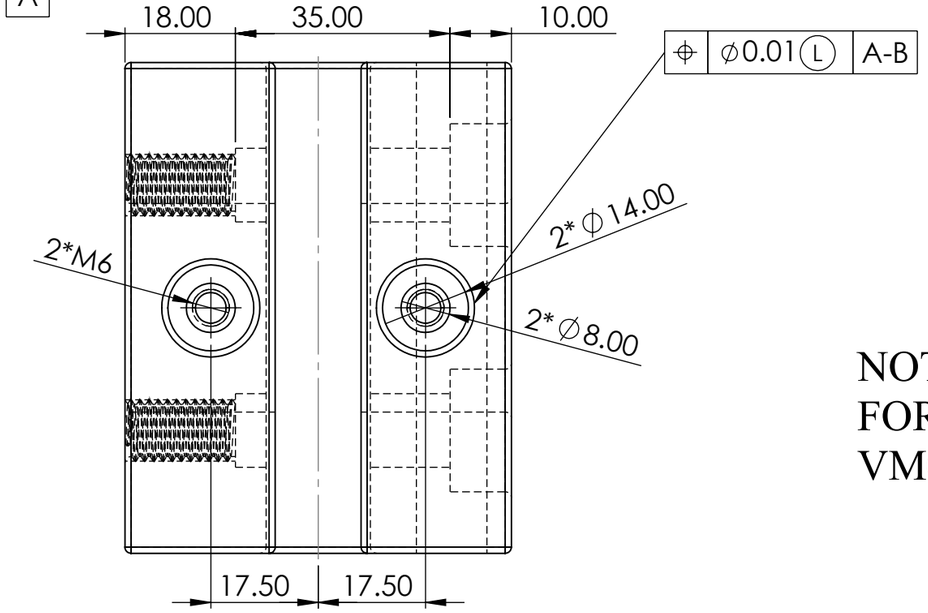



BEARING BLOCK

NOTE
FOR ALL PANEL THIS BEARING BLOCK IS USED
VMC MANCHINING

TITLE - RETRACTABLE ROOF				NIHVA Technologies Pvt. Ltd.	NIHVA TECHNOLOGIES PVT.LTD.PUNE Website - www.nihva.com
DWG NO - NTPL-000-PM-001-03-03-00					
	NAME	SIGNATURE	DATE	PROJECT NO - NTPL-000-PM	
DRAWN	V.W		07-04-2025	PRODUCT - RETRACTABLE ROOF	
CHK'D	S.W.		07-04-2025	SITE LOCATION - GUJARAT	
APPV'D	V.T.		07-04-2025		
if any queries contact - supportautomation@nihva.com				REVISION -	QTY - 1
ALL DIMENSION ARE IN mm		A3		SCALE	SHEET 8 OF 28

ITEM NO.	PART NUMBER	DESCRIPTION	QTY.
1	AL Support tube SQ TUBE 40X40X2MM L-873.33 MM	AL INTERMEDIAT SUPPORT TUBE	75

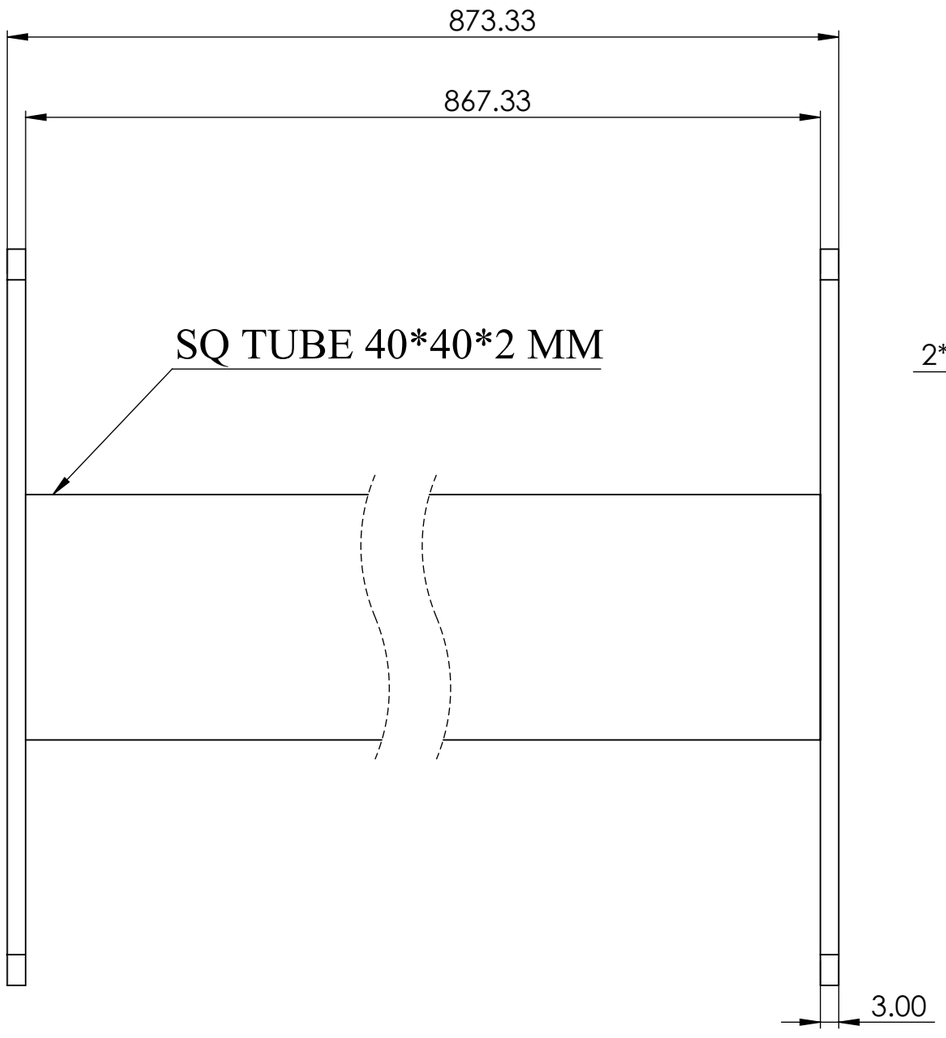


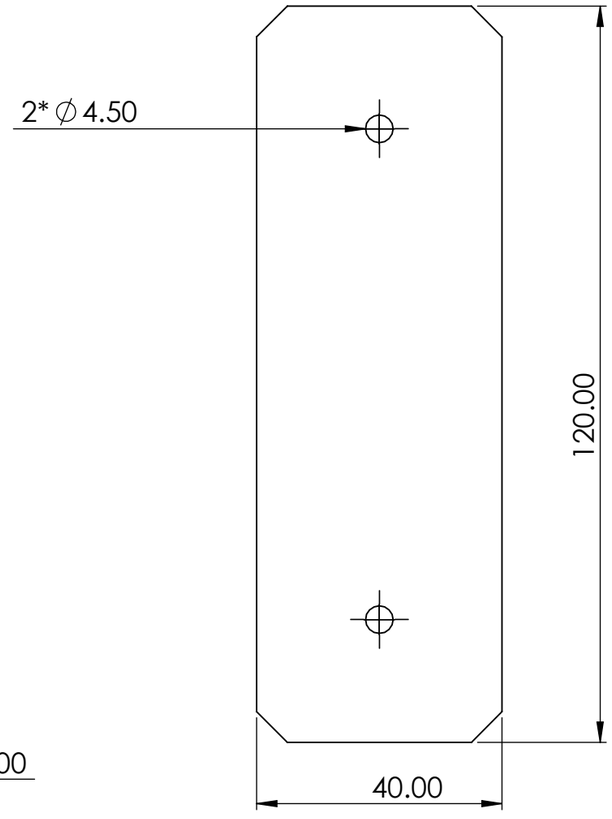


NOTE
FOR ALL PANEL THIS INTERMEDIATE TUBE IS USED

TITLE - RETRACTABLE ROOF				NIHVA TECHNOLOGIES PVT.LTD.PUNE
DWG NO - NTPL-000-PM-001-03-04-00				Website - www.nihva.com
	NAME	SIGNATURE	DATE	PROJECT NO - NTPL-000-PM
DRAWN	V.W		07-04-2025	PRODUCT - RETRACTABLE ROOF
CHK'D	S.W.		07-04-2025	SITE LOCATION - GUJARAT
APPV'D	V.T.		07-04-2025	
if any queries contact - supportautomation@nihva.com				REVISION - / QTY - 1
ALL DIMENSION ARE IN mm			A3	SCALE / SHEET 9 OF 28

ITEM NO.	PART NUMBER	DESCRIPTION	QTY.
1	T PLATE	SS304 -117.5X156X3 MM THK	40
2	MANUSH BHAI VIJAY rivet_iso_15977_4_x_16_0	RIVET M4X16	400

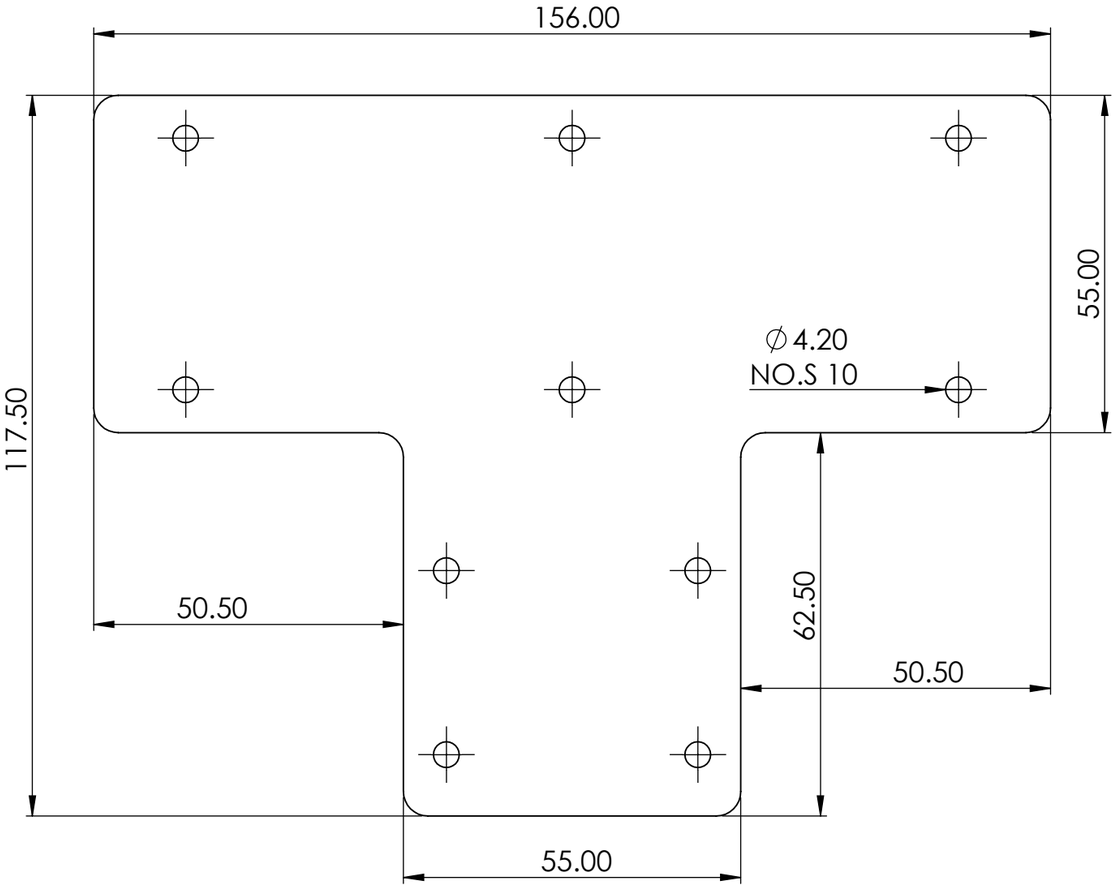


DEVELOPMENT VIEW

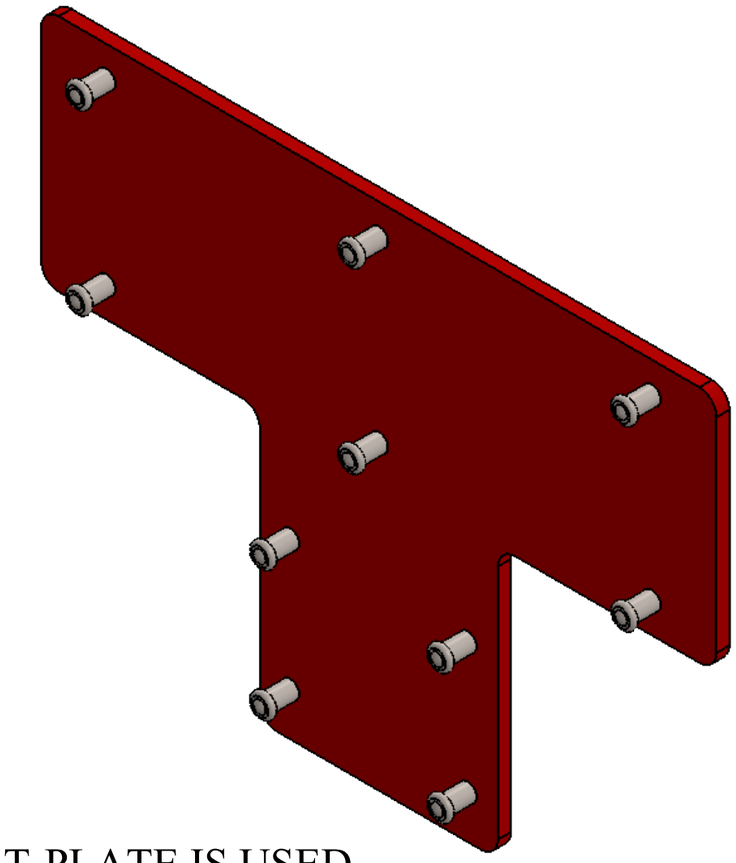



NOTE
FOR ALL PANEL THIS T-PLATE IS USED
LASER CUTTING

TITLE - RETRACTABLE ROOF				NIHVA TECHNOLOGIES PVT.LTD.PUNE
DWG NO - NTPL-000-PM-001-03-06-00				Website - www.nihva.com
	NAME	SIGNATURE	DATE	PROJECT NO - NTPL-000-PM
DRAWN	V.W		07-04-2025	PRODUCT - RETRACTABLE ROOF
CHK'D	S.W.		07-04-2025	SITE LOCATION - GUJARAT
APPV'D	V.T.		07-04-2025	
if any queries contact - supportautomation@nihva.com				REVISION - / QTY - 1
ALL DIMENSION ARE IN mm		A3		SCALE / SHEET 10 OF 28

ITEM NO.	PART NUMBER	DESCRIPTION	QTY.
1	L ANGLE PLATE	SS304 - 60X60X3 MM	60
2	MANUSH BHAI_VIJAY rivet_iso_15977_4_x_ 16_0	RIVET M4X16	480

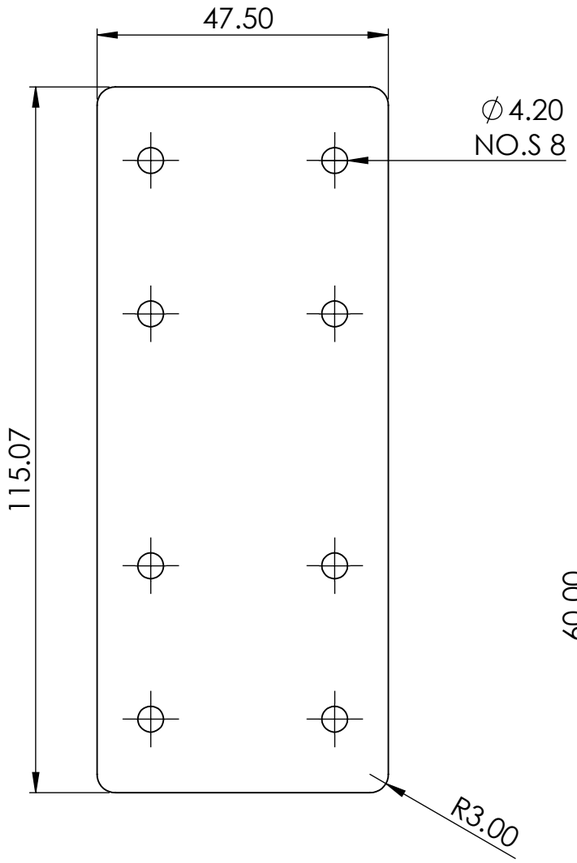

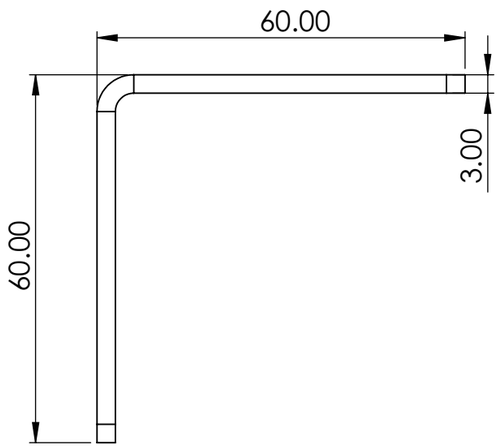

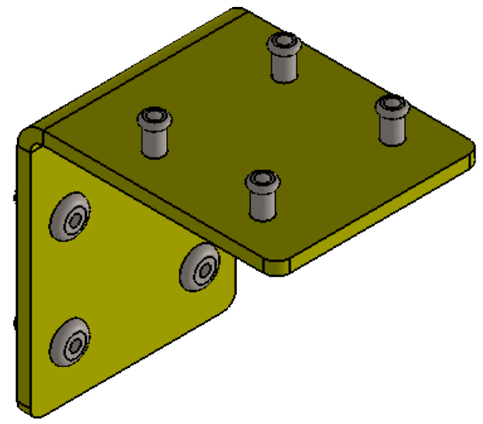


DEVELOPMENT VIEW


FOR ALL PANEL THIS L-ANGLE PLATE IS USED
LASER CUTTING

TITLE - RETRACTABLE ROOF				NIHVA TECHNOLOGIES PVT.LTD.PUNE
DWG NO - NTPL-000-PM-001-03-07-00				Website - www.nihva.com
	NAME	SIGNATURE	DATE	PROJECT NO - NTPL-000-PM
DRAWN	V.W		07-04-2025	PRODUCT - RETRACTABLE ROOF
CHK'D	S.W.		07-04-2025	SITE LOCATION - GUJARAT
APPV'D	V.T.		07-04-2025	
if any queries contact - supportautomation@nihva.com				REVISION - QTY - 1
ALL DIMENSION ARE IN mm		A3		SCALE SHEET 11 OF 28

ITEM NO.	PART NUMBER	DESCRIPTION	QTY.
1	L PLATE	SS304- 91X106X3 MM THK	40
2	MANUSH BHAI_VIJAY rivet_iso_15977_4_x_16_0	RIVET M4X16	400

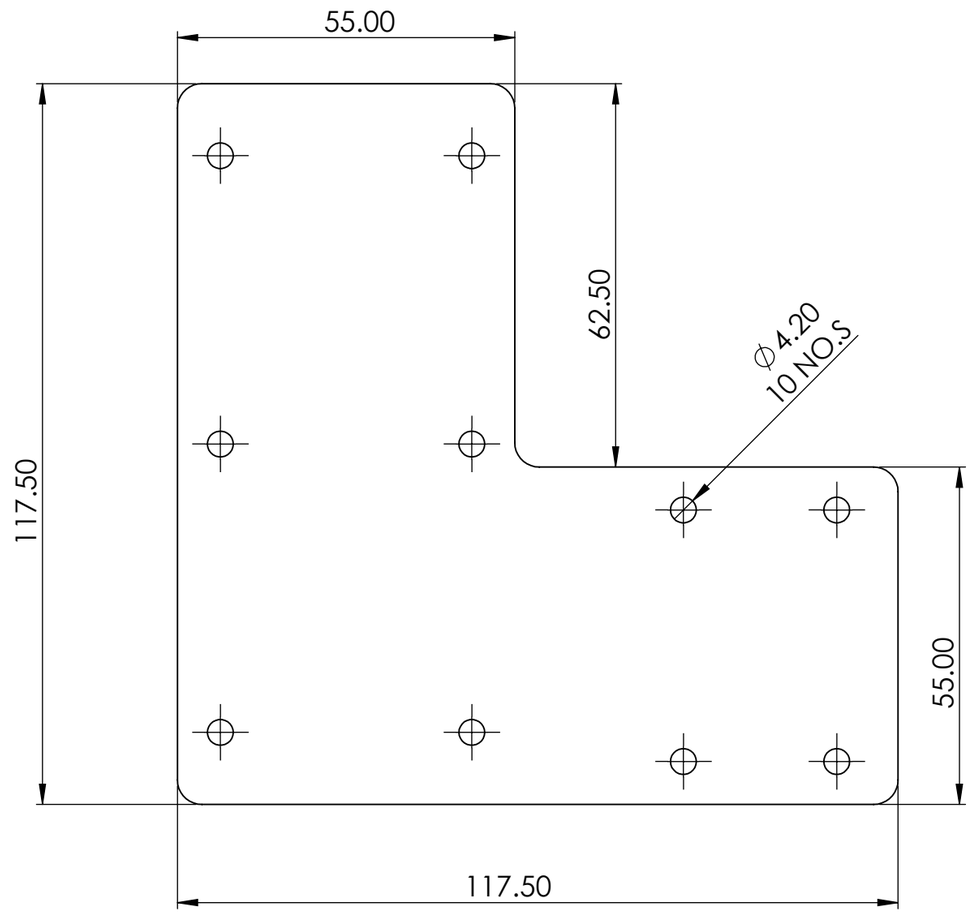


DEVELOPMENT VIEW

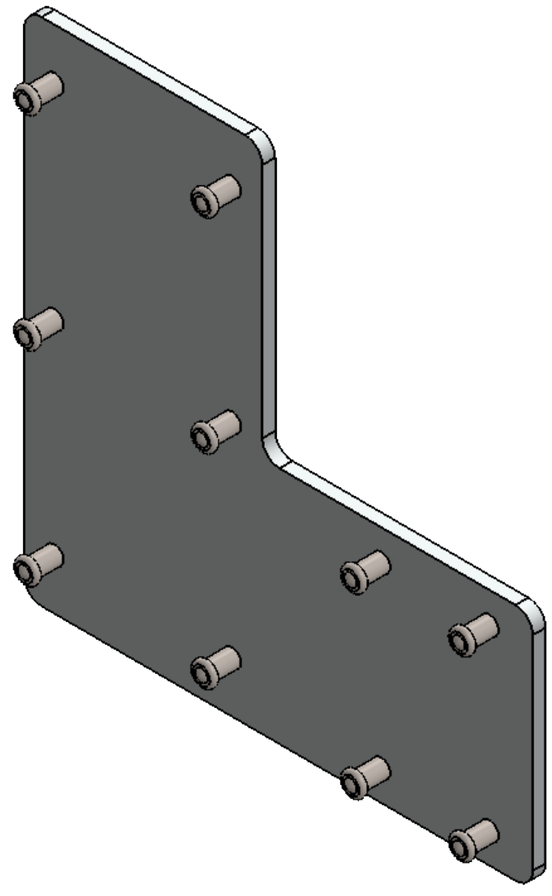



NOTE
FOR ALL PANEL THIS L-PLATE IS USED
LASER CUTTING

TITLE - RETRACTABLE ROOF				NIHVA TECHNOLOGIES PVT.LTD.PUNE
DWG NO - NTPL-000-PM-001-03-08-00				Website - www.nihva.com
	NAME	SIGNATURE	DATE	PROJECT NO - NTPL-000-PM
DRAWN	V.W		07-04-2025	PRODUCT - RETRACTABLE ROOF
CHK'D	S.W.		07-04-2025	SITE LOCATION - GUJARAT
APPV'D	V.T.		07-04-2025	
if any queries contact - supportautomation@nihva.com				REVISION - QTY - 1
ALL DIMENSION ARE IN mm		A3		SCALE SHEET 12 OF 28

ITEM NO.	PART NUMBER	DESCRIPTION	QTY.
1	VIJAY_L ANGLE WELDING PLATE	ALUMINIUM JOINING PLATE	20

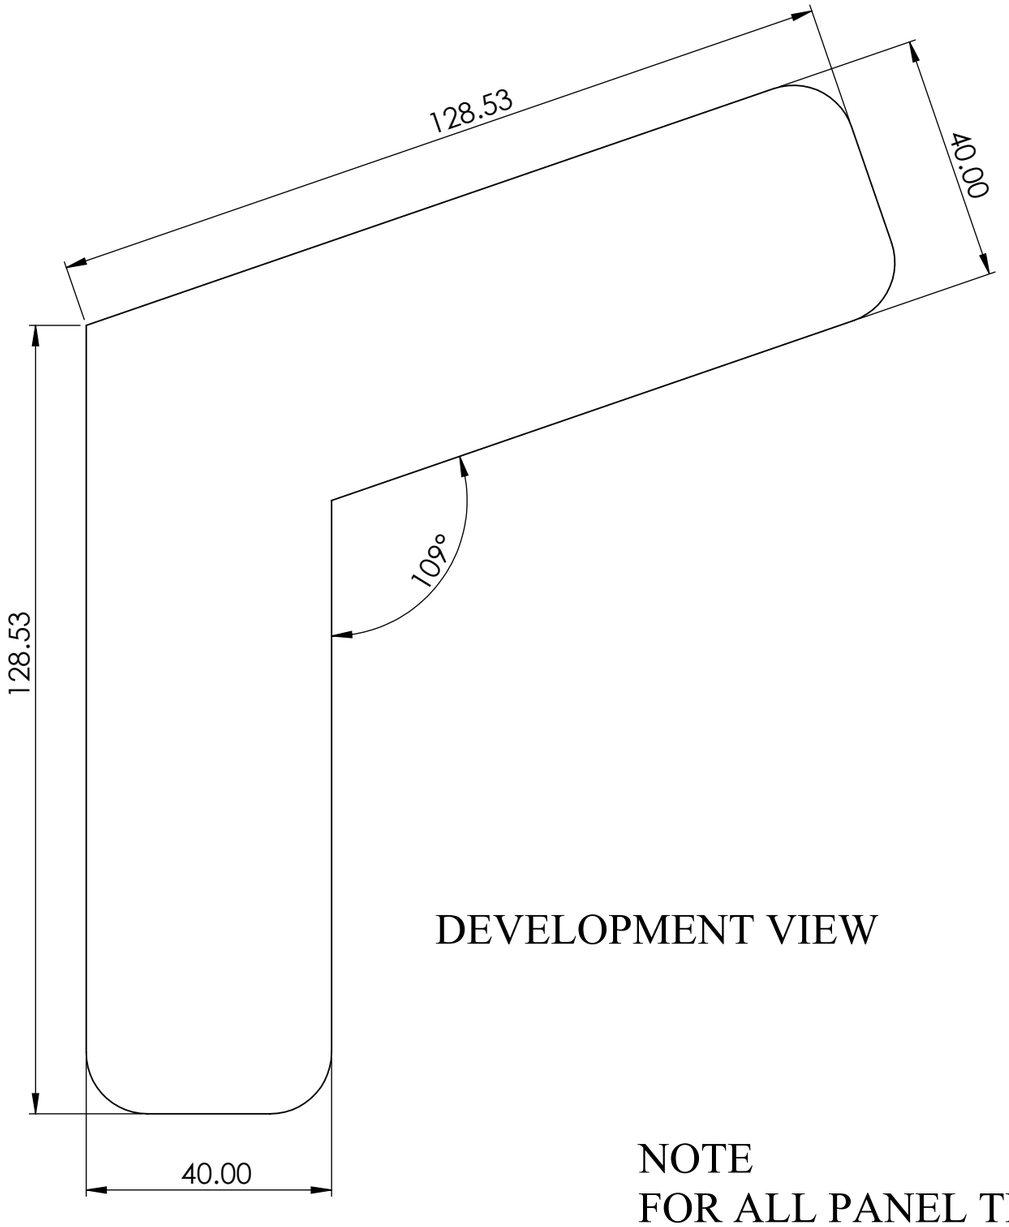

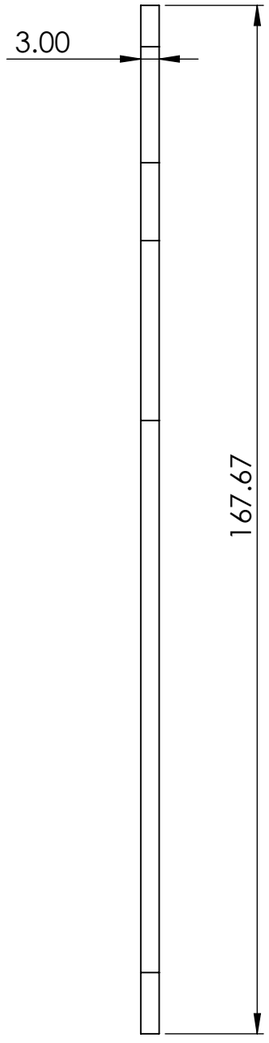


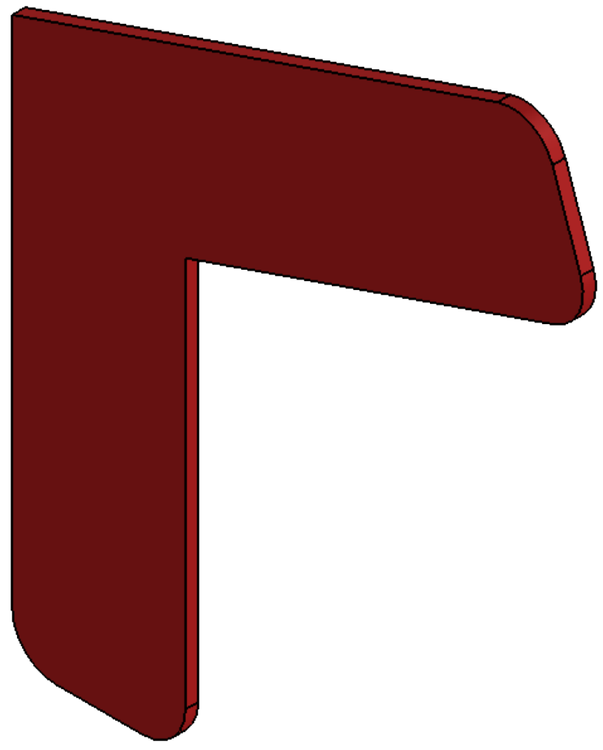


DEVELOPMENT VIEW


NOTE
FOR ALL PANEL THIS L-ANGULAR WELDING PLATE IS USED
LASER CUTTING

TITLE - RETRACTABLE ROOF				NIHVA TECHNOLOGIES PVT.LTD.PUNE
DWG NO - NTPL-000-PM-001-03-09-00				Website - www.nihva.com
	NAME	SIGNATURE	DATE	PROJECT NO - NTPL-000-PM
DRAWN	V.W		07-04-2025	PRODUCT - RETRACTABLE ROOF
CHK'D	S.W.		07-04-2025	SITE LOCATION - GUJARAT
APPV'D	V.T.		07-04-2025	
if any queries contact - supportautomation@nihva.com				REVISION - QTY - 1
ALL DIMENSION ARE IN mm			A3	SCALE SHEET 13 OF 28

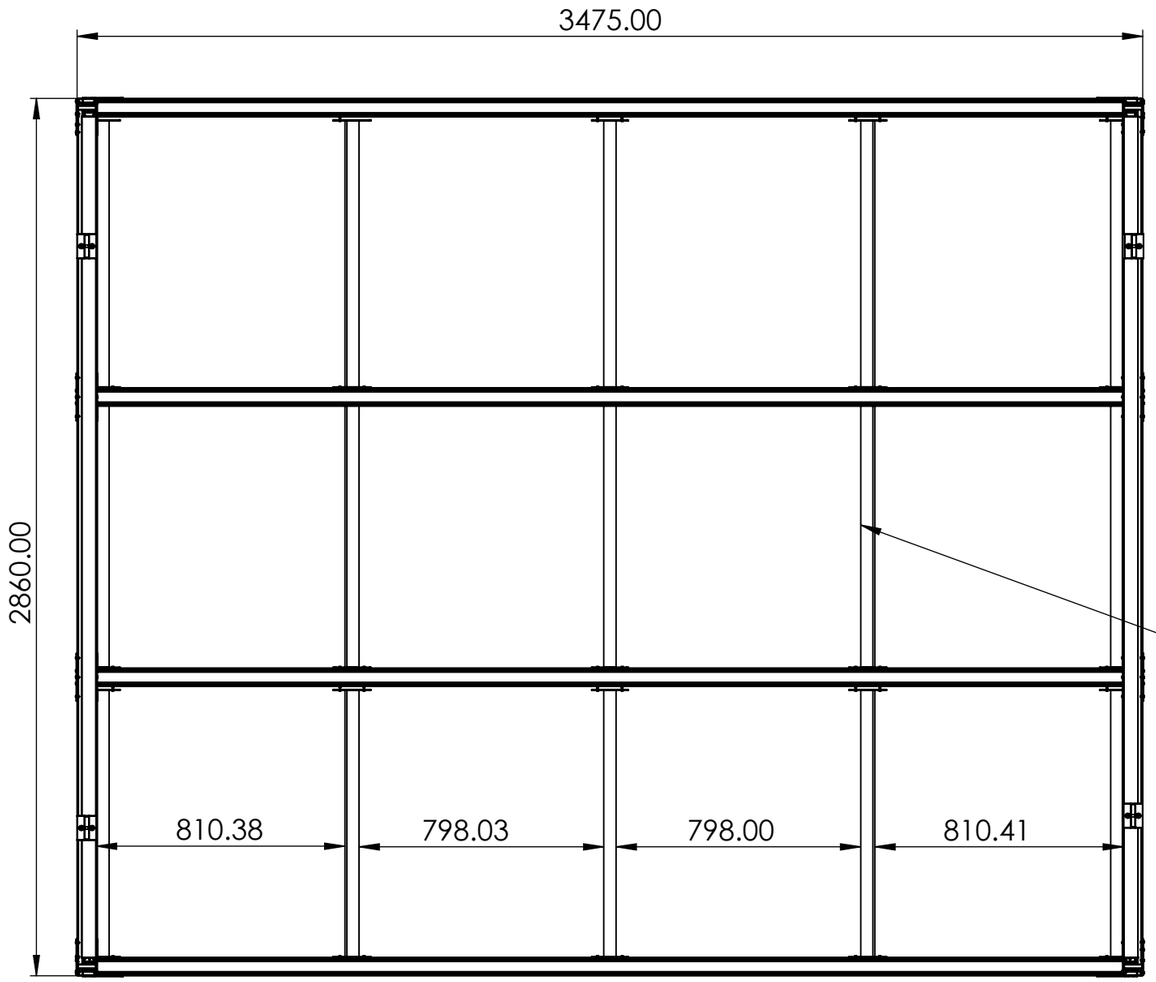

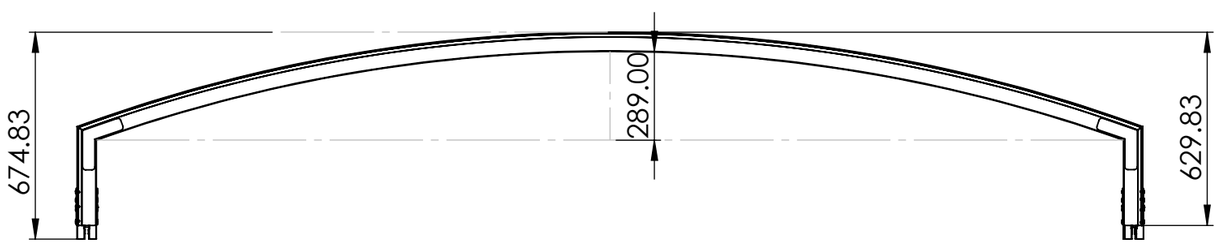


ITEM NO.	PART NUMBER	DESCRIPTION	QTY.
1	PANEL NO 2		1
2	VIJAY_BEARING BLOCK ASM WITH SHOULDER BOLT	SLIDING BLOCK	4
9	T PLATE	JOINING PLATE	8
4	L ANGLE PLATE	JOINING PLATE	12
5	L PALTE	JOINING PLATE	8
6	MANUSH BHAI _01 VIJAY L ANGLE WELDING PLATE	JOINING PLATE	3
7	MANUSH BHAI VIJAY L ANGLE PLATE	JOINING PLATE	1
8	AL Support tube SQ TUBE 40X40X2MM L-873.33 MM	AL INTERMEDIAT SUPPORT TUBE	15
9	VIJAY_Rivet_iso_15977_4_x_16 _0	RIVET M4X16	60
10	PANEL NO 2 POLYCARBONET SHEET		3

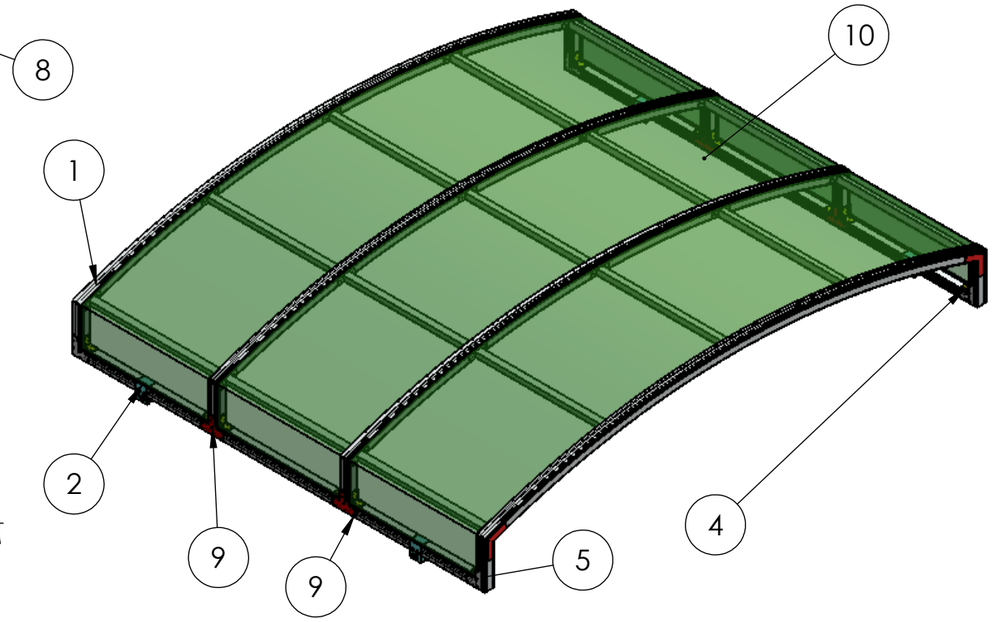


PANEL NO 2 ASM


TITLE - RETRACTABLE ROOF				NIHVA TECHNOLOGIES PVT.LTD.PUNE
DWG NO - NTPL-000-PM-001-04-00-00				Website - www.nihva.com
	NAME	SIGNATURE	DATE	PROJECT NO - NTPL-000-PM
DRAWN	V.W		07-04-2025	PRODUCT - RETRACTABLE ROOF
CHK'D	S.W.		07-04-2025	SITE LOCATION - GUJARAT
APPV'D	V.T.		07-04-2025	
if any queries contact - supportautomation@nihva.com				REVISION - QTY - 1
ALL DIMENSION ARE IN mm		A3		SCALE SHEET 14 OF 28



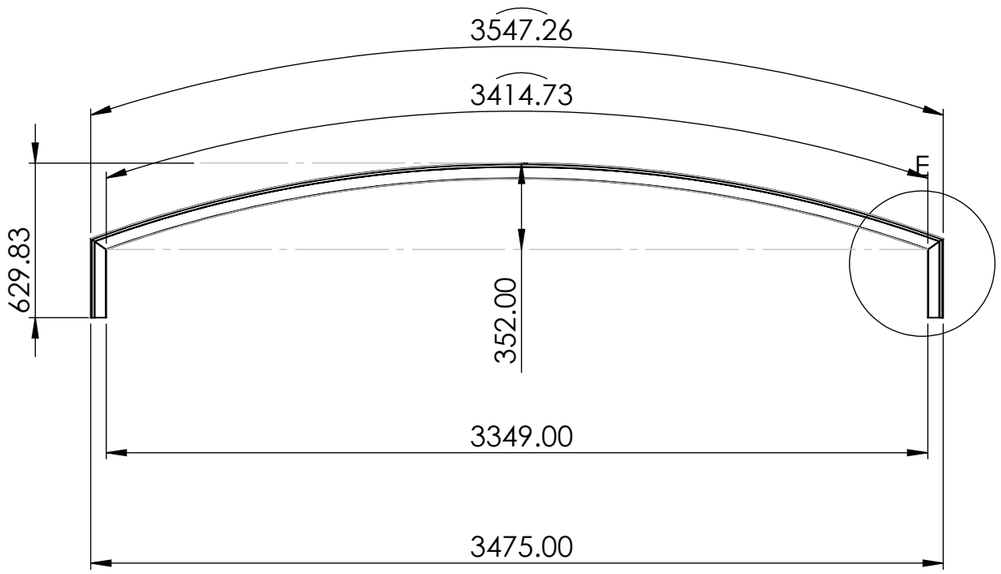

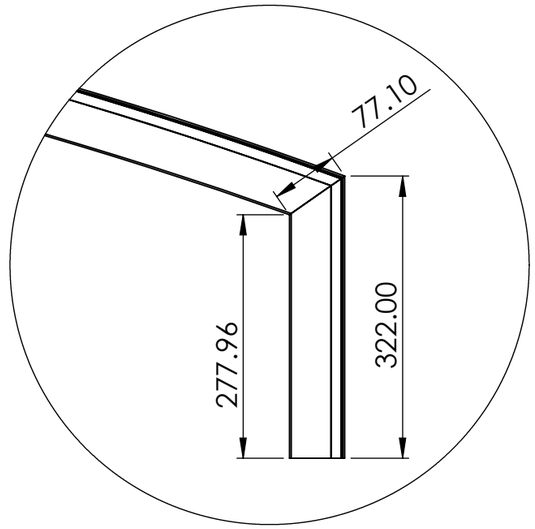


DETAIL E
SCALE 1 : 7

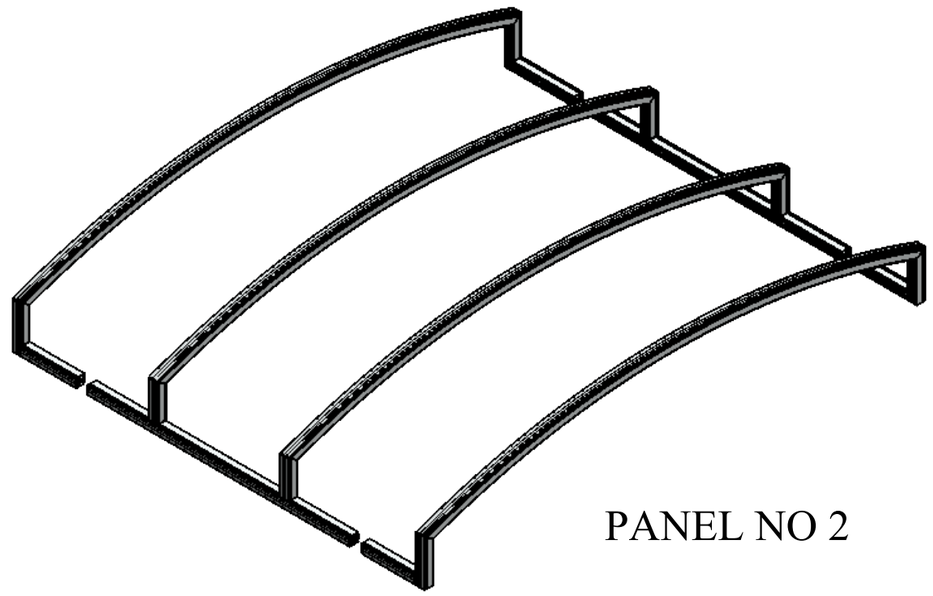



PANEL NO 2

TITLE - RETRACTABLE ROOF				NIHVA TECHNOLOGIES PVT.LTD.PUNE Website - www.nihva.com
DWG NO - NTPL-000-PM-001-04-01-00				
	NAME	SIGNATURE	DATE	PROJECT NO - NTPL-000-PM
DRAWN	V.W		07-04-2025	PRODUCT - RETRACTABLE ROOF
CHK'D	S.W.		07-04-2025	SITE LOCATION - GUJARAT
APPV'D	V.T.		07-04-2025	
if any queries contact - supportautomation@nihva.com				REVISION - / QTY - 1
ALL DIMENSION ARE IN mm		A3		SCALE / SHEET 15 OF 28

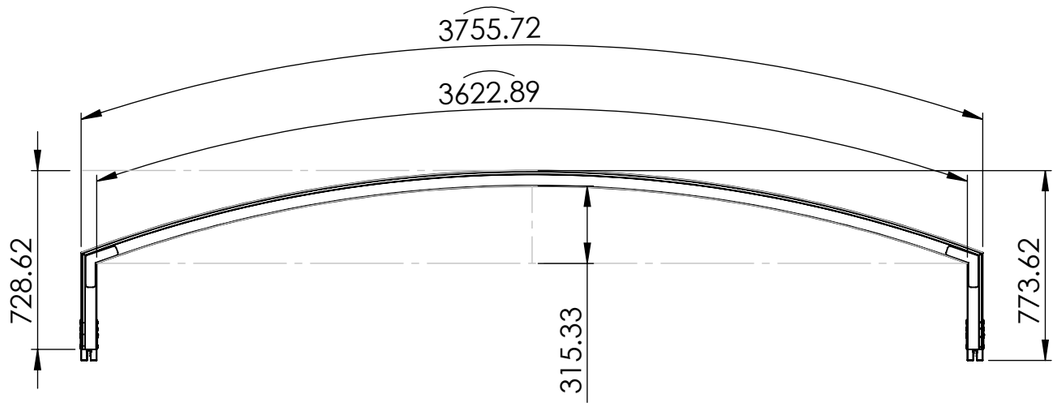


ITEM NO.	PART NUMBER	DESCRIPTION	QTY.
1	PANEL NO 3		1
2	VIJAY_BEARING BLOCK ASM WITH SHOULDER BOLT	SLIDING BLOCK	4
3	T PLATE	JOINING PLATE	8
4	L ANGLE PLATE	JOINING PLATE	12
5	L PALTE	JOINING PLATE	8
6	VIJAY_L ANGLE WELDING PLATE	ALUMINIUM JOINING PLATE	4
7	AL Support tube SQ TUBE 40X40X2MM L-873.33 MM	AL INTERMEDIAT SUPPORT TUBE	15
8	VIJAY_Rivet_iso_15977_4_x_16_0	RIVET M4X16	60
9	PANEL NO 3 POLYCARBONET SHEET		3

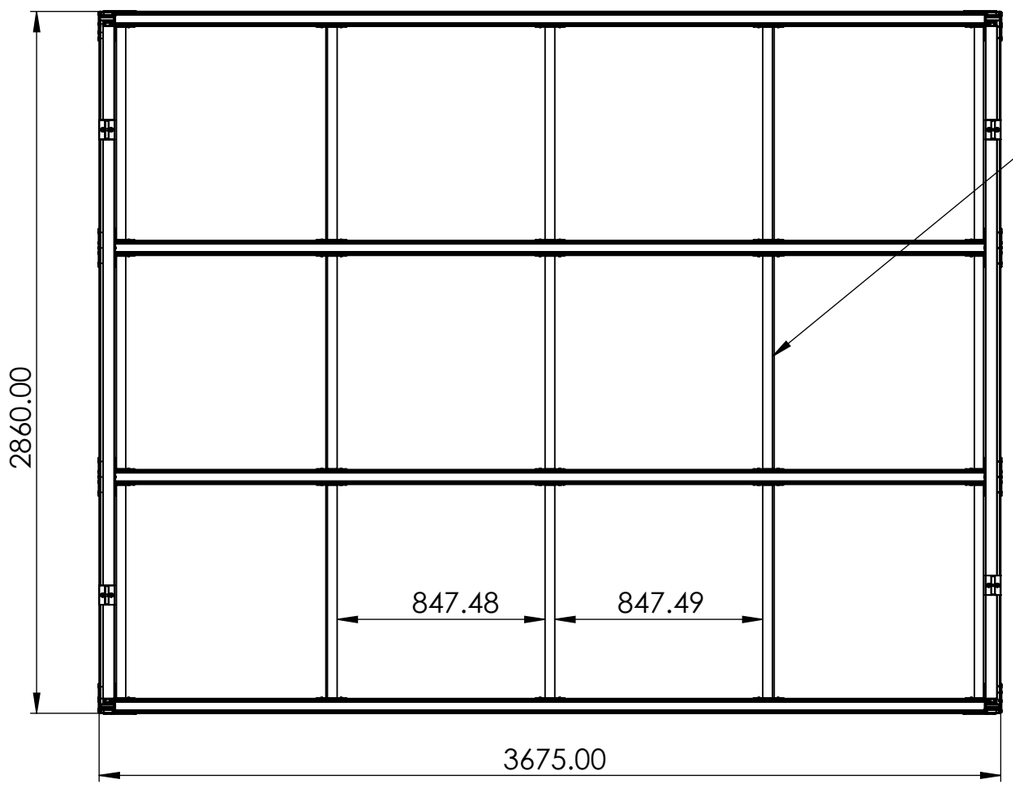


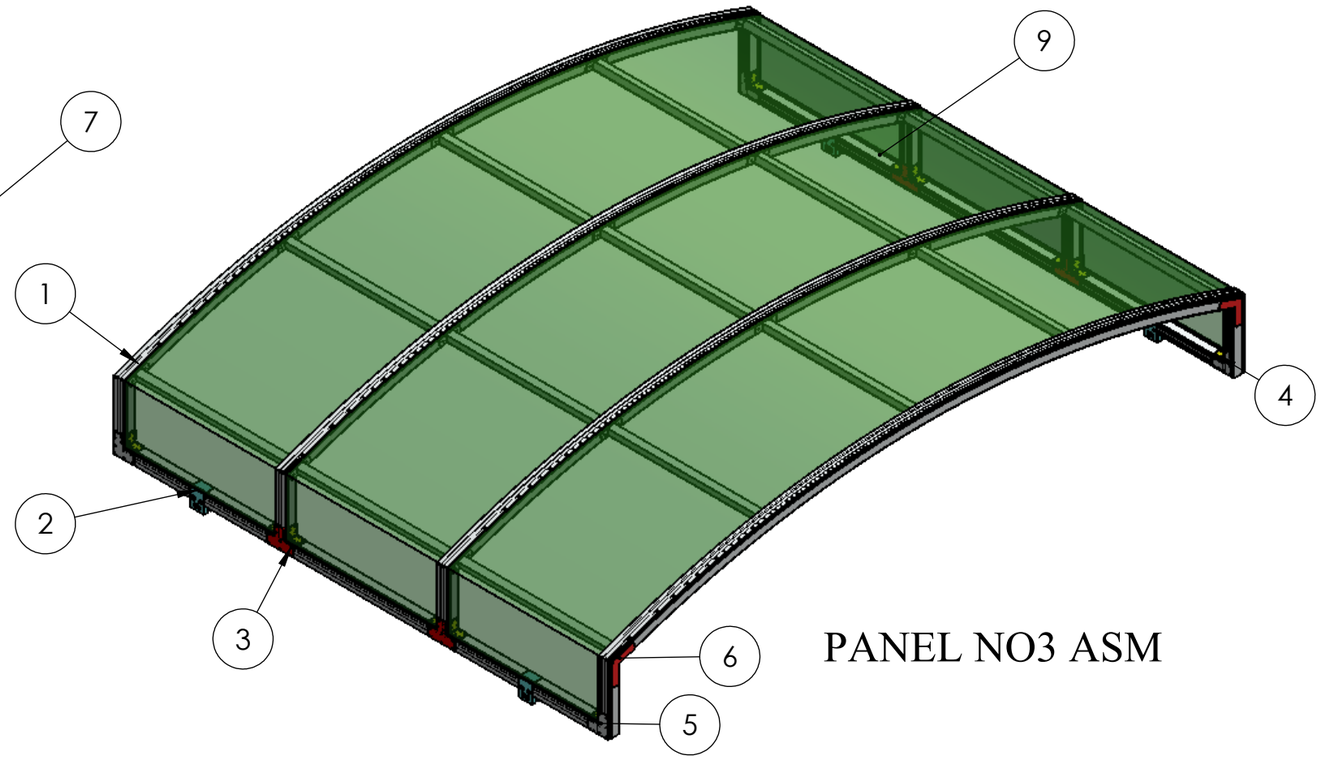

PANEL NO3 ASM


TITLE - RETRACTABLE ROOF				NIHVA TECHNOLOGIES PVT.LTD.PUNE
DWG NO - NTPL-000-PM-001-05-00-00				Website - www.nihva.com
	NAME	SIGNATURE	DATE	PROJECT NO - NTPL-000-PM
DRAWN	V.W		07-04-2025	PRODUCT - RETRACTABLE ROOF
CHK'D	S.W.		07-04-2025	SITE LOCATION - GUJARAT
APPV'D	V.T.		07-04-2025	
if any queries contact - supportautomation@nihva.com				REVISION - QTY - 1
ALL DIMENSION ARE IN mm			A3	SCALE SHEET 16 OF 28

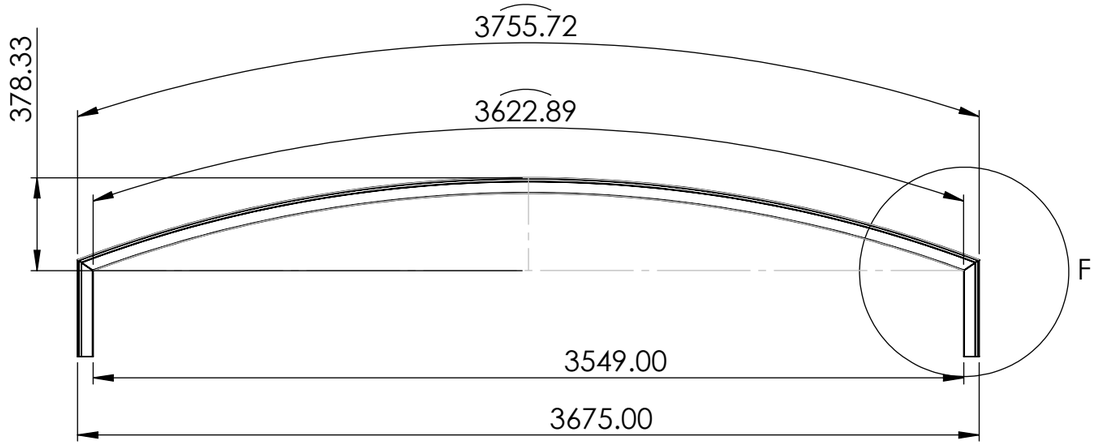

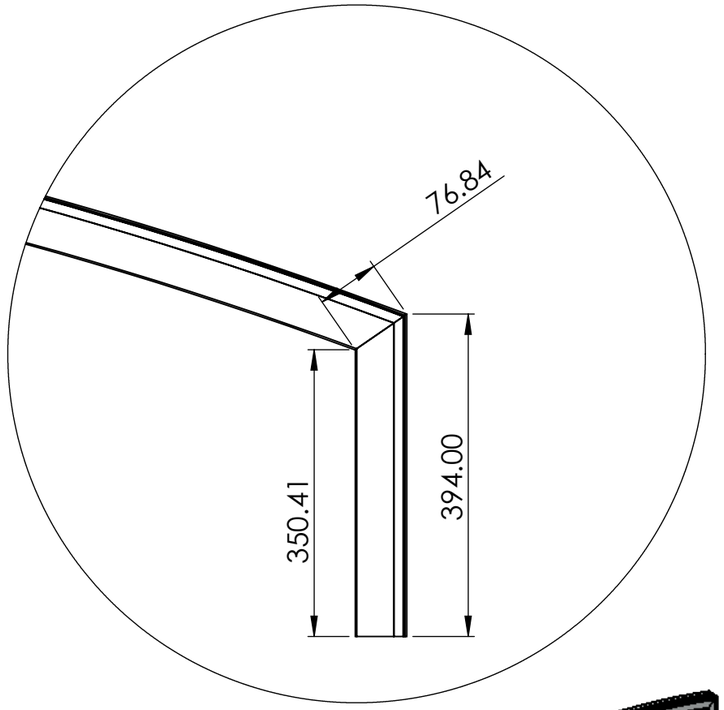

DETAIL F
SCALE 2 : 15




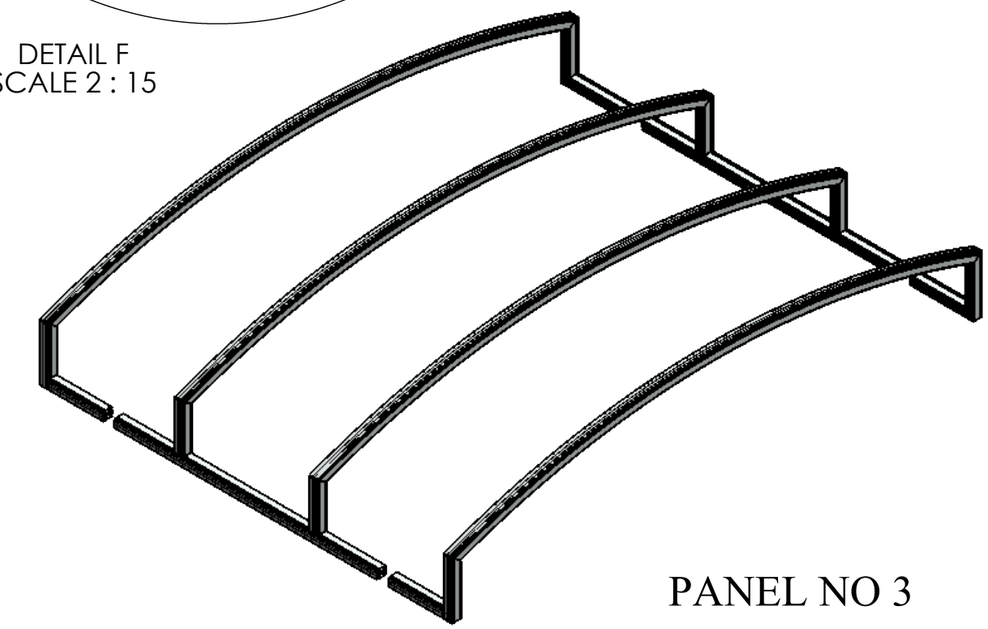



PANEL NO 3

TITLE - RETRACTABLE ROOF				NIHVA TECHNOLOGIES PVT.LTD.PUNE Website - www.nihva.com
DWG NO - NTPL-000-PM-001-05-01-00				
	NAME	SIGNATURE	DATE	PROJECT NO - NTPL-000-PM
DRAWN	V.W		07-04-2025	PRODUCT - RETRACTABLE ROOF
CHK'D	S.W.		07-04-2025	SITE LOCATION - GUJARAT
APPV'D	V.T.		07-04-2025	
if any queries contact - supportautomation@nihva.com				REVISION - / QTY - 1
ALL DIMENSION ARE IN mm			A3	SCALE / SHEET 17 OF 28

ITEM NO.	PART NUMBER	DESCRIPTION	QTY.
1	PANEL NO 4		1
2	VIJAY_BEARING BLOCK ASM WITH SHOULDER BOLT	SLIDING BLOCK	4
3	T PLATE	JOINING PLATE	8
4	L ANGLE PLATE	JOINING PLATE	12
5	L PALTE	JOINING PLATE	8
6	VIJAY_L ANGLE WELDING PLATE	ALUMINIUM JOINING PLATE	4
7	AL Support tube SQ TUBE 40X40X2MM L-873.33 MM	AL INTERMEDIAT SUPPORT TUBE	15
8	VIJAY_Rivet_iso_15977_4_x_16_0	RIVET M4X16	60
9	PANEL NO 4 POLYCARBONET SHEET		3

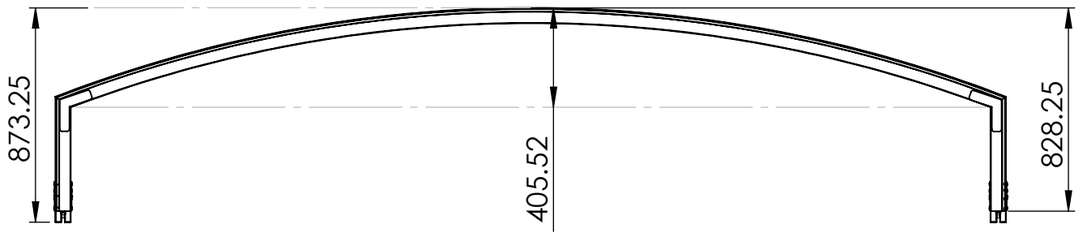


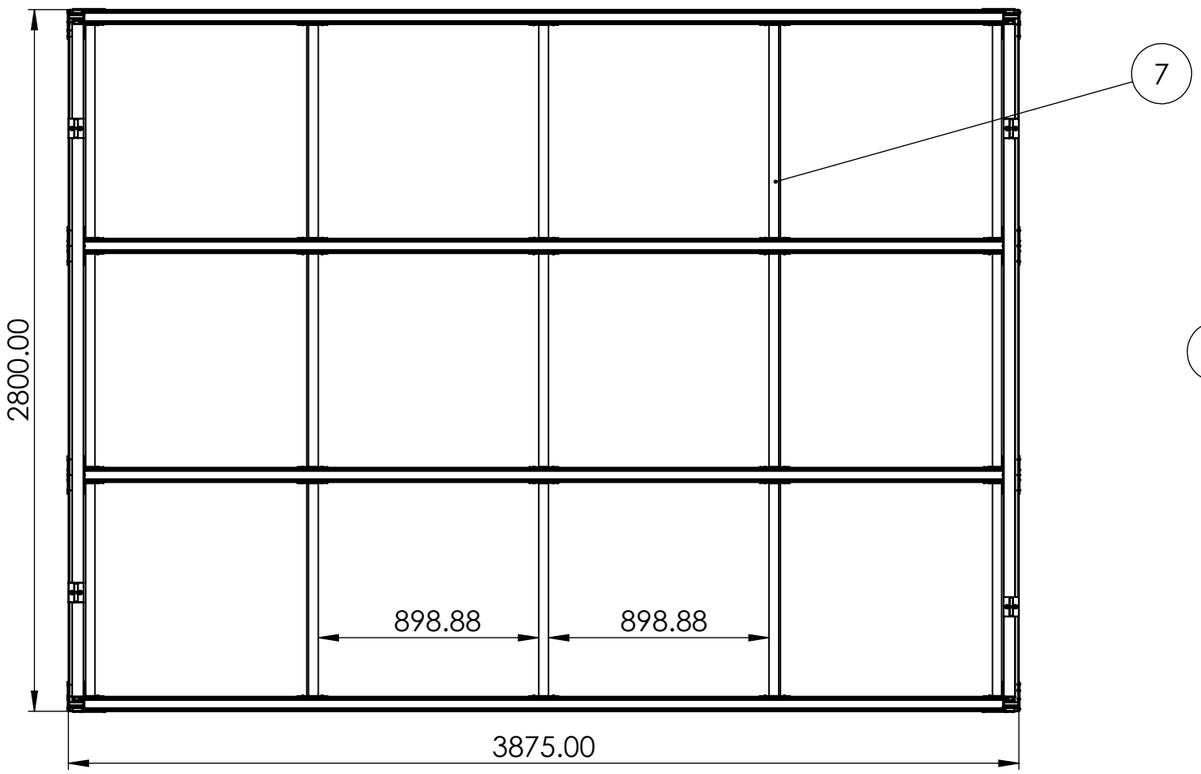


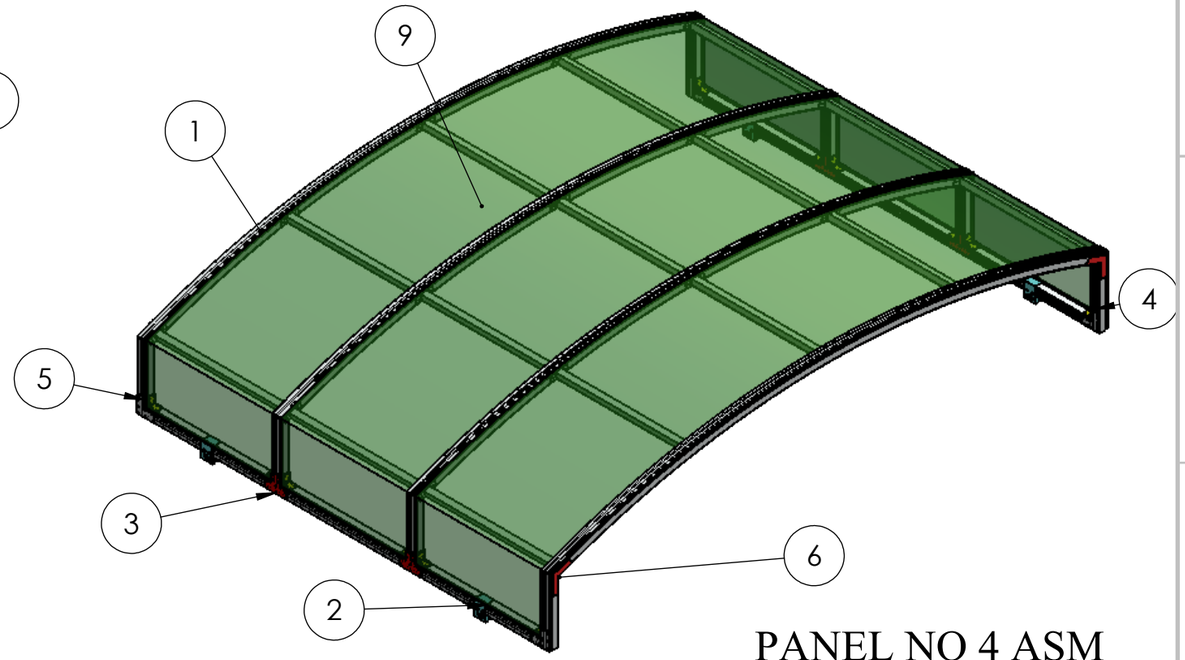

PANEL NO 4 ASM


TITLE - RETRACTABLE ROOF				NIHVA TECHNOLOGIES PVT.LTD.PUNE
DWG NO - NTPL-000-PM-001-06-00-00				Website - www.nihva.com
	NAME	SIGNATURE	DATE	PROJECT NO - NTPL-000-PM
DRAWN	V.W		07-04-2025	PRODUCT - RETRACTABLE ROOF
CHK'D	S.W.		07-04-2025	SITE LOCATION - GUJARAT
APPV'D	V.T.		07-04-2025	
if any queries contact - supportautomation@nihva.com				REVISION - QTY - 1
ALL DIMENSION ARE IN mm			A3	SCALE SHEET 18 OF 28

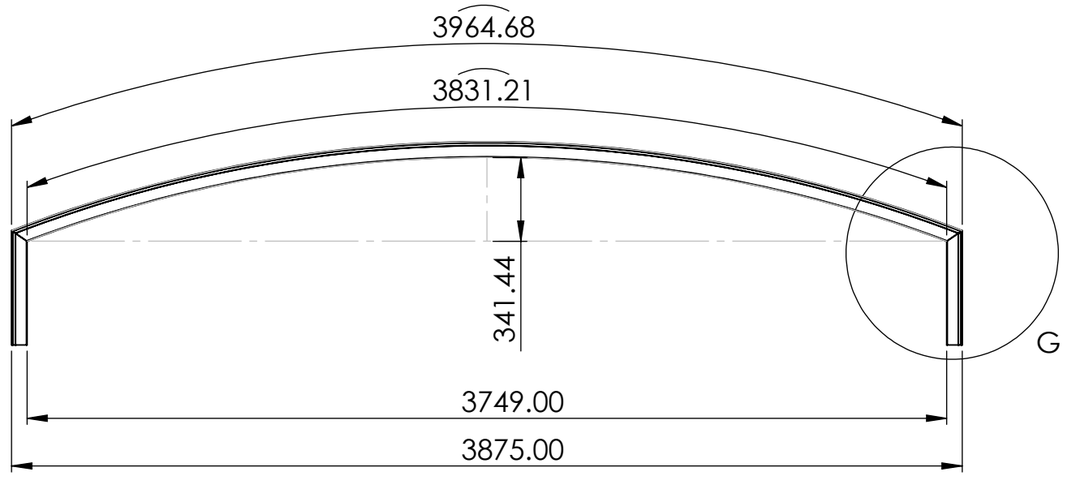

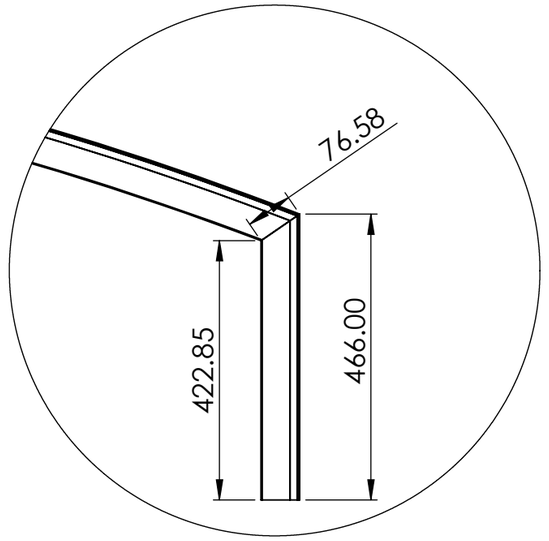


DETAIL G
SCALE 1 : 10



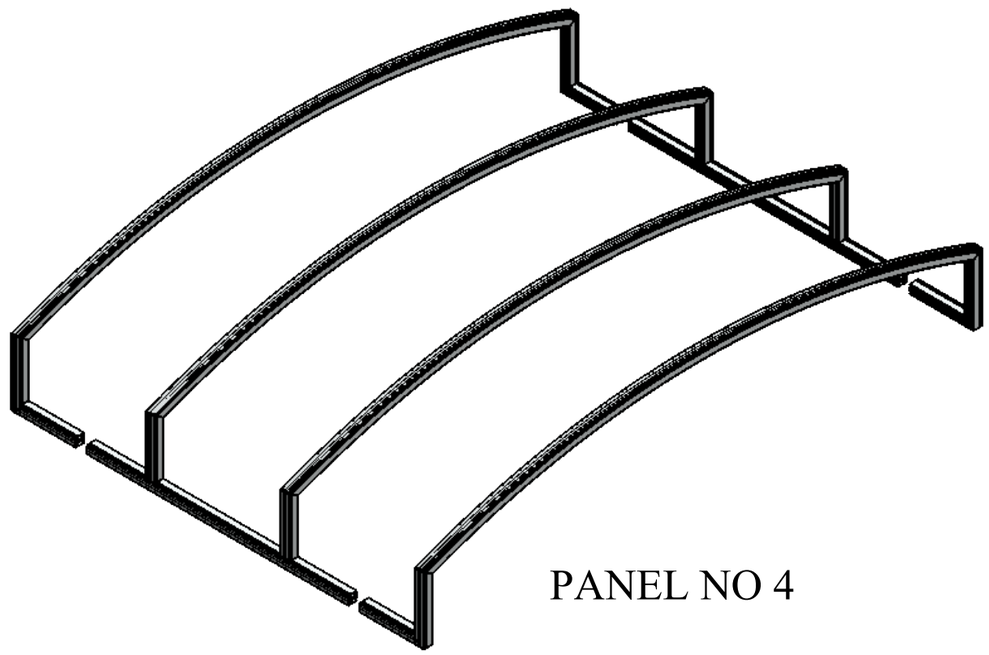


PANEL NO 4

TITLE - RETRACTABLE ROOF				NIHVA TECHNOLOGIES PVT.LTD.PUNE
DWG NO - NTPL-000-PM-001-06-01-00				Website - www.nihva.com
	NAME	SIGNATURE	DATE	PROJECT NO - NTPL-000-PM
DRAWN	V.W		07-04-2025	PRODUCT - RETRACTABLE ROOF
CHK'D	S.W.		07-04-2025	SITE LOCATION - GUJARAT
APPV'D	V.T.		07-04-2025	
if any queries contact - supportautomation@nihva.com				REVISION - QTY - 1
ALL DIMENSION ARE IN mm			A3	SCALE SHEET 19 OF 28

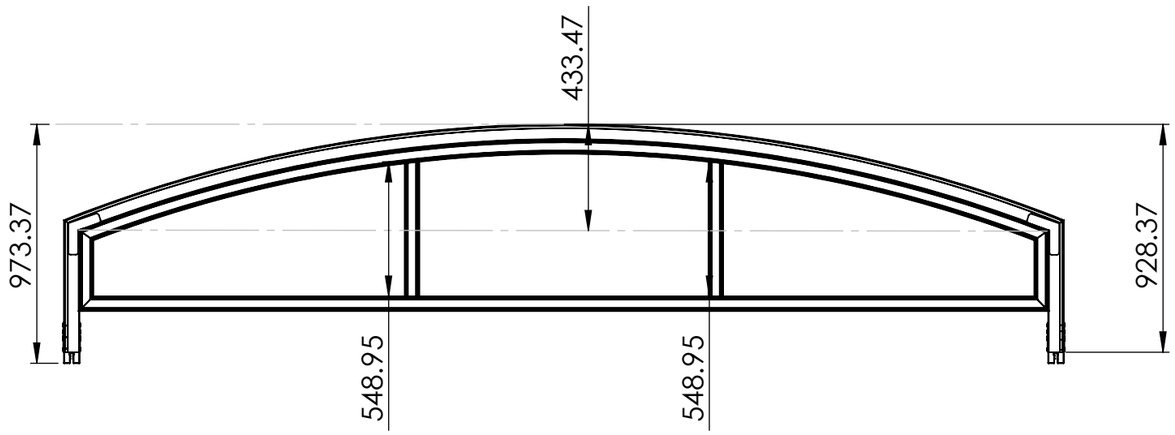



ITEM NO.	PART NUMBER	DESCRIPTION	QTY.
1	PANEL NO 5		1
2	VIJAY_BEARING BLOCK ASM WITH SHOULDER BOLT	SLIDING BLOCK	4
3	T PLATE	JOINING PLATE	8
4	L ANGLE PLATE	JOINING PLATE	12
5	L PALTE	JOINING PLATE	8
6	VIJAY_L ANGLE WELDING PLATE	ALUMINIUM JOINING PLATE	4
7	AL Support tube SQ TUBE 40X40X2MM L-873.33 MM	AL INTERMEDIAT SUPPORT TUBE	15
8	VIJAY_Rivet_iso_15977_4_x_16_0	RIVET M4X16	60
9	PANEL NO5 ENCLOSER		1
10	PANEL NO 5 POLYCARBONET SHEET		3
11	PANEL NO5 ENCLOSER POLYCARBONET SHHET		1

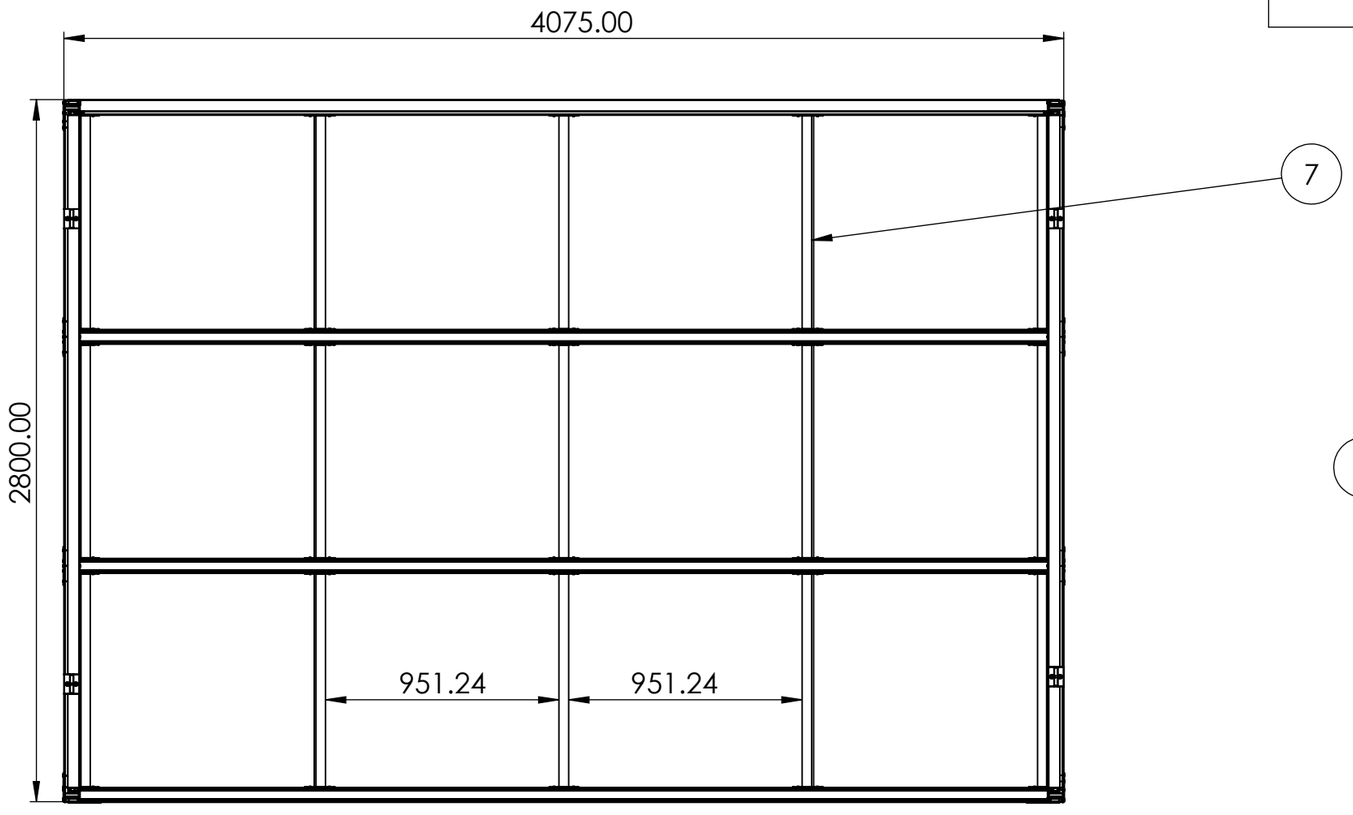

PANEL NO 5 ASM


TITLE - RETRACTABLE ROOF				NIHVA Technologies Pvt. Ltd.	NIHVA TECHNOLOGIES PVT.LTD.PUNE Website - www.nihva.com
DWG NO - NTPL-000-PM-001-07-00-00					
	NAME	SIGNATURE	DATE	PROJECT NO - NTPL-000-PM	
DRAWN	V.W		07-04-2025	PRODUCT - RETRACTABLE ROOF	
CHK'D	S.W.		07-04-2025	SITE LOCATION - GUJARAT	
APPV'D	V.T.		07-04-2025		
if any queries contact - supportautomation@nihva.com				REVISION -	QTY - 1
ALL DIMENSION ARE IN mm			A3	SCALE	SHEET 20 OF 28

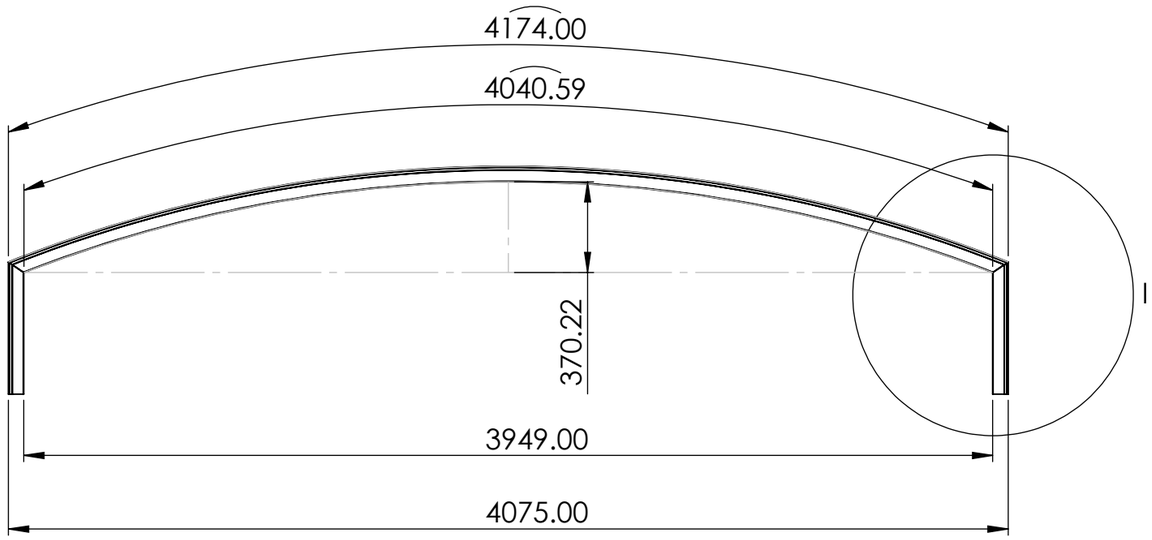

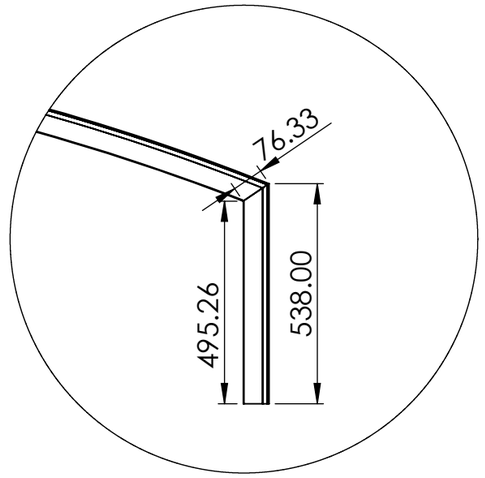


DETAIL I
SCALE 1 : 15




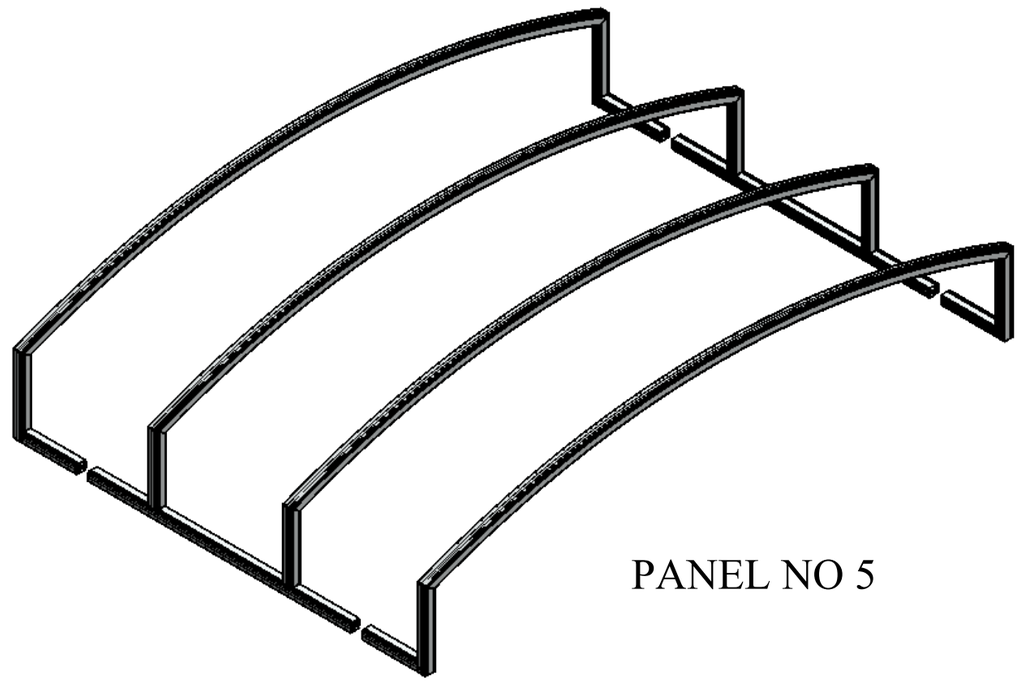

PANEL NO 5

TITLE - RETRACTABLE ROOF				NIHVA TECHNOLOGIES PVT.LTD.PUNE
DWG NO - NTPL-000-PM-001-07-01-00				Website - www.nihva.com
	NAME	SIGNATURE	DATE	PROJECT NO - NTPL-000-PM
DRAWN	V.W		07-04-2025	PRODUCT - RETRACTABLE ROOF
CHK'D	S.W.		07-04-2025	SITE LOCATION - GUJARAT
APPV'D	V.T.		07-04-2025	
if any queries contact - supportautomation@nihva.com				REVISION - / QTY - 1
ALL DIMENSION ARE IN mm			A3	SCALE / SHEET 21 OF 28

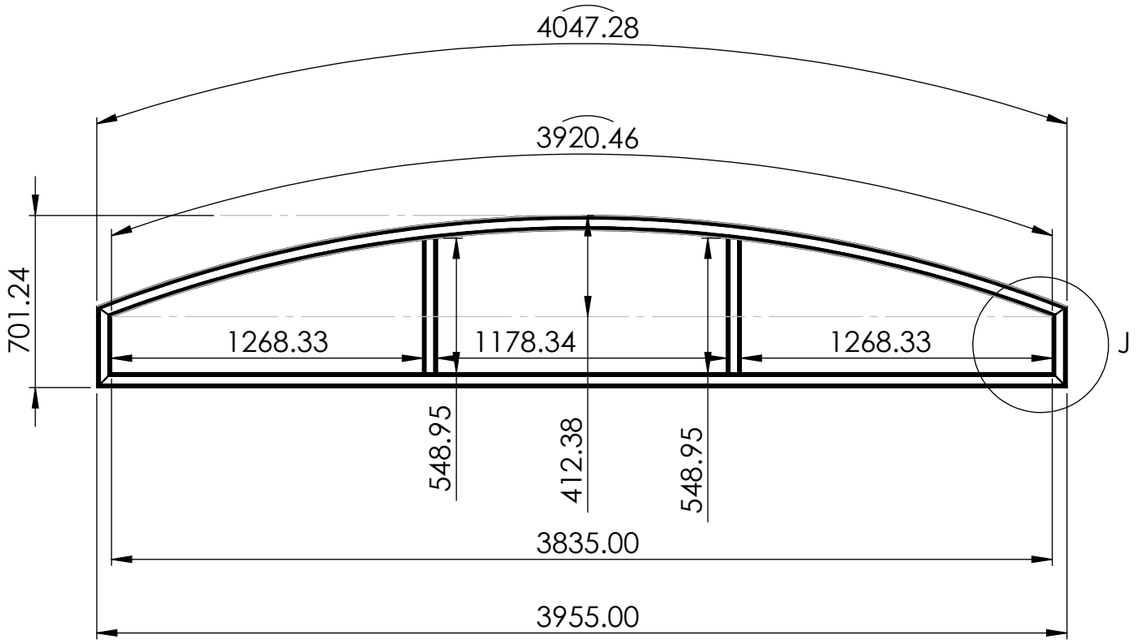


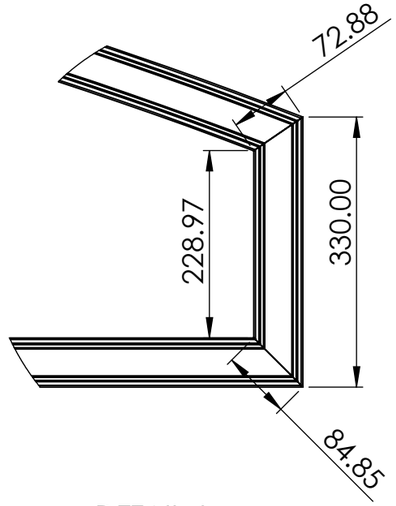



DETAIL J
SCALE 2 : 15


PANEL NO 5 ENCLOSER


TITLE - RETRACTABLE ROOF				NIHVA TECHNOLOGIES PVT.LTD.PUNE
DWG NO - NTPL-000-PM-001-07-02-00				Website - www.nihva.com
	NAME	SIGNATURE	DATE	PROJECT NO - NTPL-000-PM
DRAWN	V.W		07-04-2025	PRODUCT - RETRACTABLE ROOF
CHK'D	S.W.		07-04-2025	SITE LOCATION - GUJARAT
APPV'D	V.T.		07-04-2025	
if any queries contact - supportautomation@nihva.com				REVISION - QTY - 1
ALL DIMENSION ARE IN mm			A3	SCALE SHEET 22 OF 28

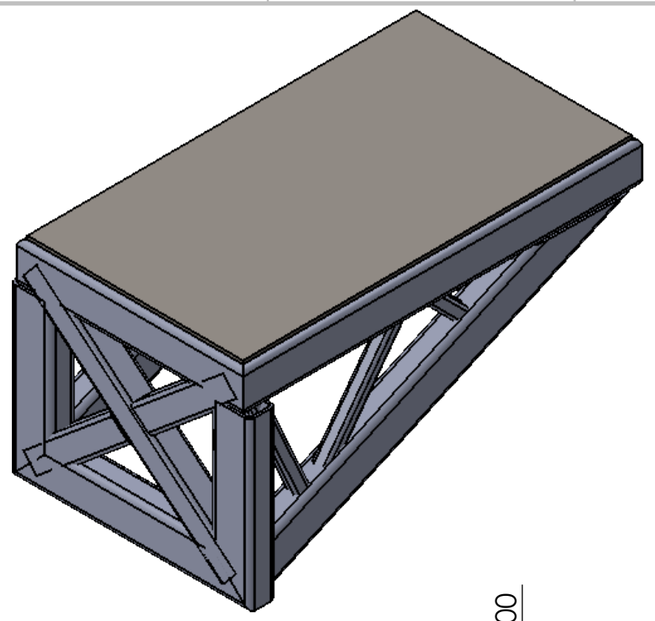

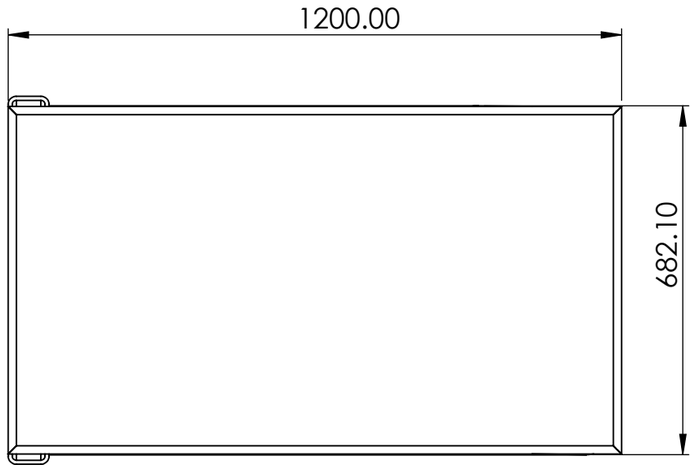

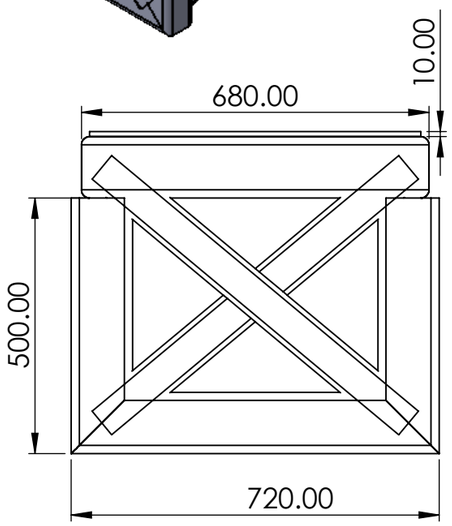

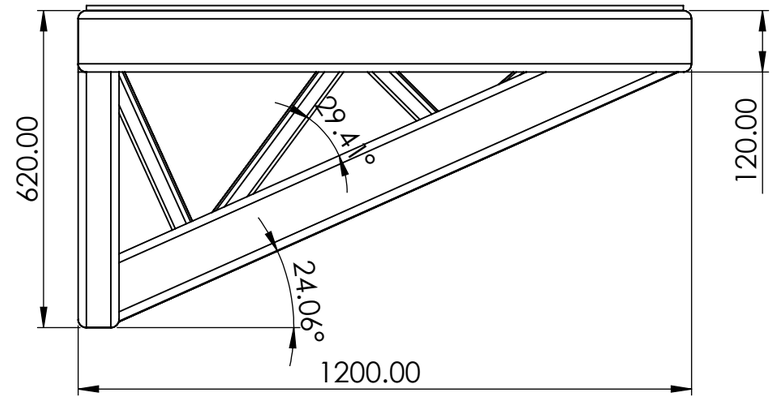

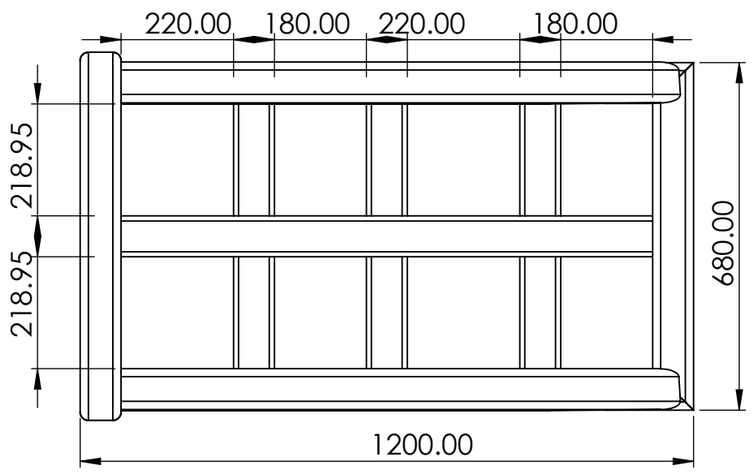


MB RECTANGULAR TUBE STRUCTURE


BOM Table(Restructured)


ITEM NO.	PART NUMBER	DESCRIPTION	QTY.
1		TUBE, RECTANGULAR 120.000000 X 80.000000 X 8.00	2
2		TUBE, RECTANGULAR 120.000000 X 80.000000 X 8.00	2
3		TUBE, RECTANGULAR 120.000000 X 80.000000 X 8.00	2
4		TUBE, RECTANGULAR 120.000000 X 80.000000 X 8.00	1
5		TUBE, RECTANGULAR 120.000000 X 80.000000 X 8.00	2
6		TUBE, SQUARE 80.000000 X 80.000000 X 5.000000	1
7		TUBE, SQUARE 80.000000 X 80.000000 X 5.000000	2
8		TUBE, SQUARE 80.000000 X 80.000000 X 5.000000	1
9		TUBE, SQUARE 80.000000 X 80.000000 X 5.000000	6
10		TUBE, SQUARE 40.000000 X 40.000000 X 4.000000	1
11		TUBE, SQUARE 40.000000 X 40.000000 X 4.000000	1
12		TUBE, SQUARE 40.000000 X 40.000000 X 4.000000	1
13		TUBE, SQUARE 40.000000 X 40.000000 X 4.000000	1
14			1
15		TUBE, SQUARE 40.000000 X 40.000000 X 4.000000	1
16		TUBE, SQUARE 40.000000 X 40.000000 X 4.000000	1
17		TUBE, SQUARE 40.000000 X 40.000000 X 4.000000	1
18		TUBE, SQUARE 40.000000 X 40.000000 X 4.000000	1


TITLE - RETRACTABLE ROOF				NIHVA TECHNOLOGIES PVT.LTD.PUNE
DWG NO - NTPL-000-PM-001-08-00-00				Website - www.nihva.com
	NAME	SIGNATURE	DATE	PROJECT NO - NTPL-000-PM
DRAWN	V.W		07-04-2025	PRODUCT - RETRACTABLE ROOF
CHK'D	S.W.		07-04-2025	SITE LOCATION - GUJARAT
APPV'D	V.T.		07-04-2025	
if any queries contact - supportautomation@nihva.com				REVISION - QTY - 1
ALL DIMENSION ARE IN mm			A3	SCALE SHEET 23 OF 28

ITEM NO.	PART NUMBER	DESCRIPTION	QTY.
1	MOTOR MTG BRACKET NICE 1.8T	MS	1
		Sheet	1

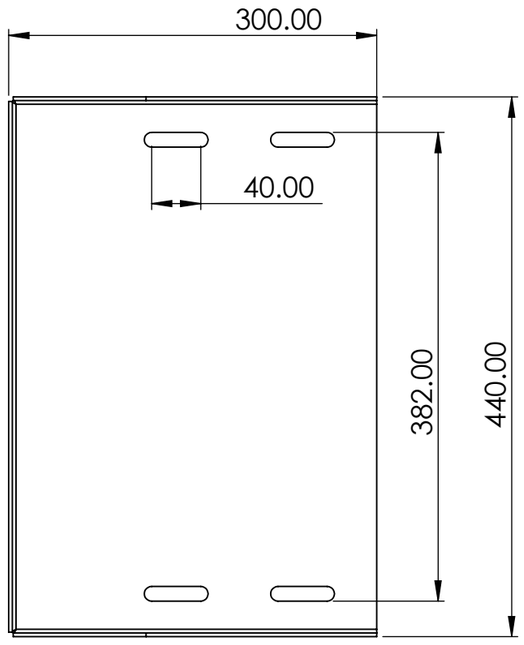

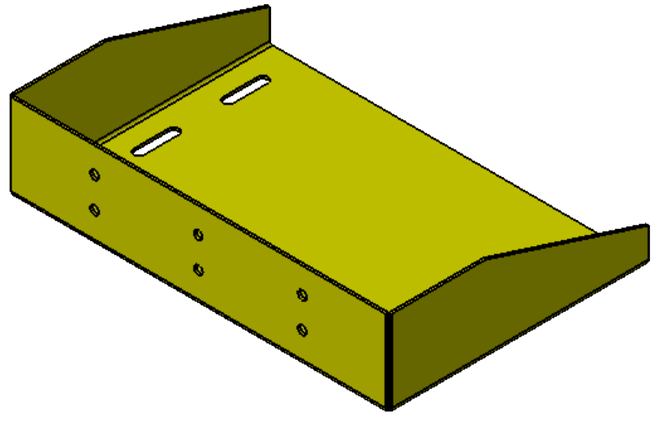

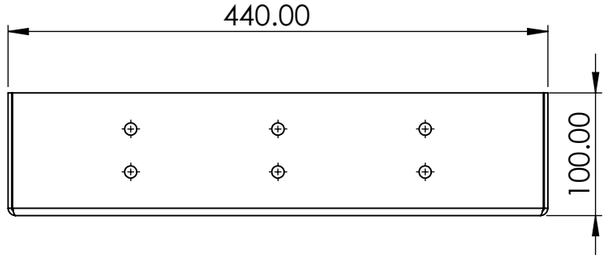


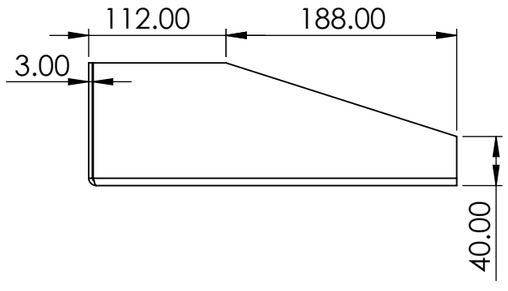



MOTOR MTG BRACKET NICE 1.8T


TITLE - RETRACTABLE ROOF				NIHVA TECHNOLOGIES PVT.LTD.PUNE
DWG NO - NTPL-000-PM-001-09-00-00				Website - www.nihva.com
	NAME	SIGNATURE	DATE	PROJECT NO - NTPL-000-PM
DRAWN	V.W		07-04-2025	PRODUCT - RETRACTABLE ROOF
CHK'D	S.W.		07-04-2025	SITE LOCATION - GUJARAT
APPV'D	V.T.		07-04-2025	
if any queries contact - supportautomation@nihva.com				REVISION - QTY - 1
ALL DIMENSION ARE IN mm		A3		SCALE SHEET 24 OF 28

ITEM NO.	PART NUMBER	DESCRIPTION	QTY.
1	NICE RB 1.8T		1

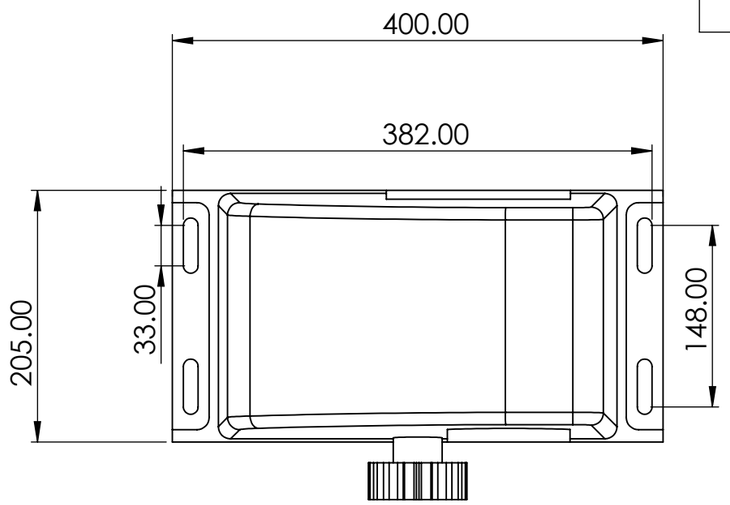

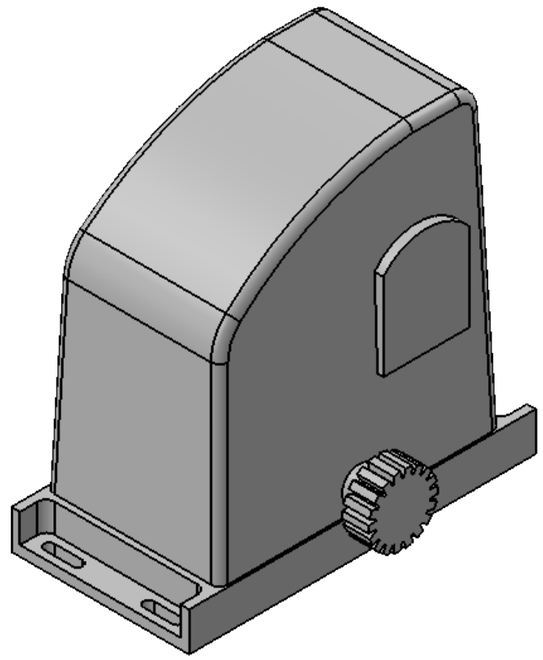


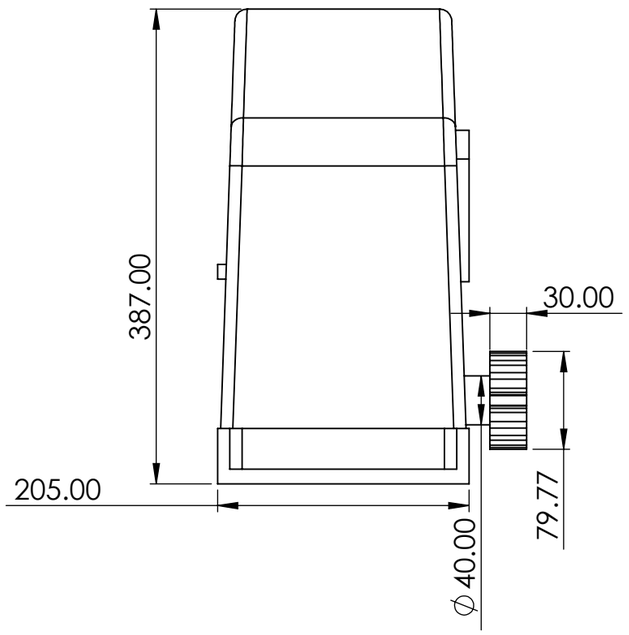

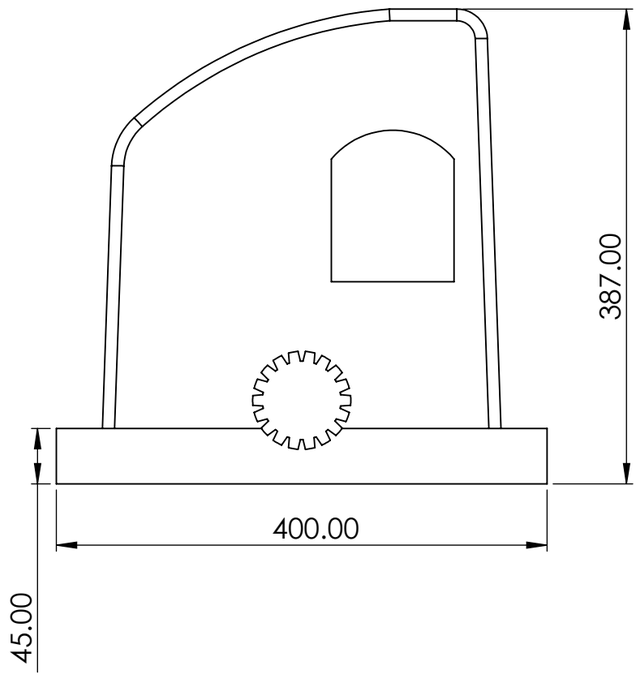



MOTOR NICE 1.8T

TITLE - RETRACTABLE ROOF				NIHVA TECHNOLOGIES PVT.LTD.PUNE
DWG NO - NTPL-000-PM-001-14-00-00				Website - www.nihva.com
	NAME	SIGNATURE	DATE	PROJECT NO - NTPL-000-PM
DRAWN	V.W		07-04-2025	PRODUCT - RETRACTABLE ROOF
CHK'D	S.W.		07-04-2025	SITE LOCATION - GUJARAT
APPV'D	V.T.		07-04-2025	
if any queries contact - supportautomation@nihva.com				REVISION - QTY - 1
ALL DIMENSION ARE IN mm		A3		SCALE SHEET 25 OF 28

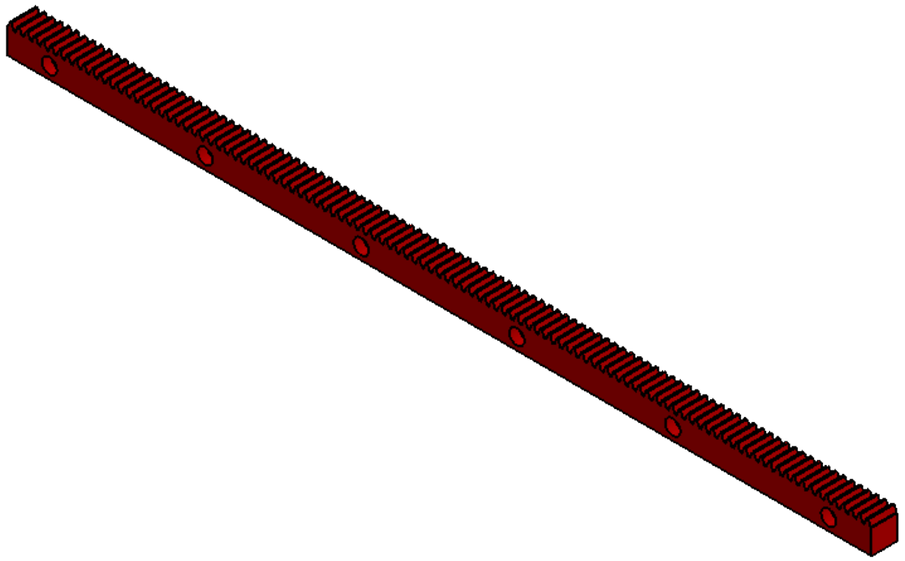

ITEM NO.	PART NUMBER	DESCRIPTION	QTY.
1	VIJAY RACK	STD (M4 RACK, 30x8x1000 mm, ZINC COATED WITH SPACERS AND SCREWS.)	16

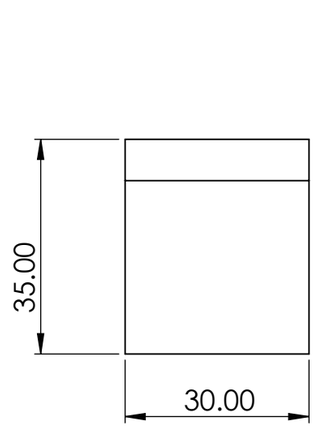


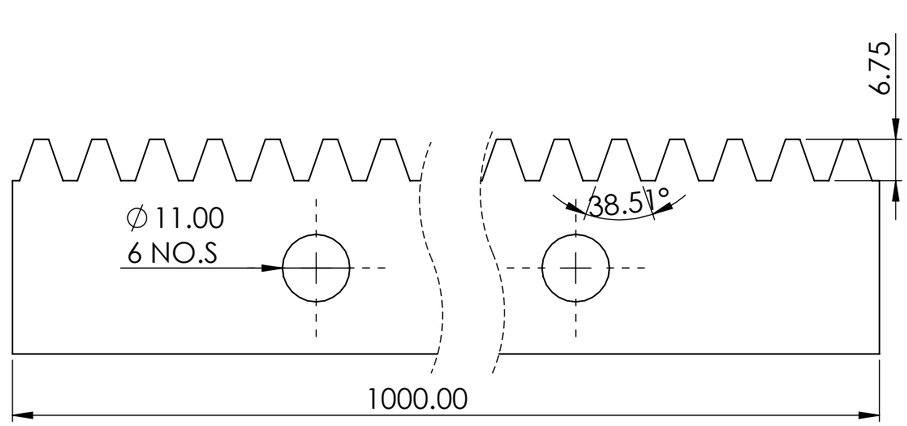


RACK

TITLE - RETRACTABLE ROOF				NIHVA TECHNOLOGIES PVT.LTD.PUNE
DWG NO - NTPL-000-PM-001-11-00-00				Website - www.nihva.com
	NAME	SIGNATURE	DATE	PROJECT NO - NTPL-000-PM
DRAWN	V.W		07-04-2025	PRODUCT - RETRACTABLE ROOF
CHK'D	S.W.		07-04-2025	SITE LOCATION - GUJARAT
APPV'D	V.T.		07-04-2025	
if any queries contact - supportautomation@nihva.com				REVISION - QTY - 1
ALL DIMENSION ARE IN mm		A3		SCALE SHEET 26 OF 28

ITEM NO.	PART NUMBER	DESCRIPTION	QTY.
1	C- CHANEL MTG BASE PLATE	320X50X10MM THK	17
2	C - CHANEL	70X30X575	34
3	C- CHANEL JOINING PLATE	35X40X10MM THK	34
4	VIJAY BUSBAR MTG PLATE		34

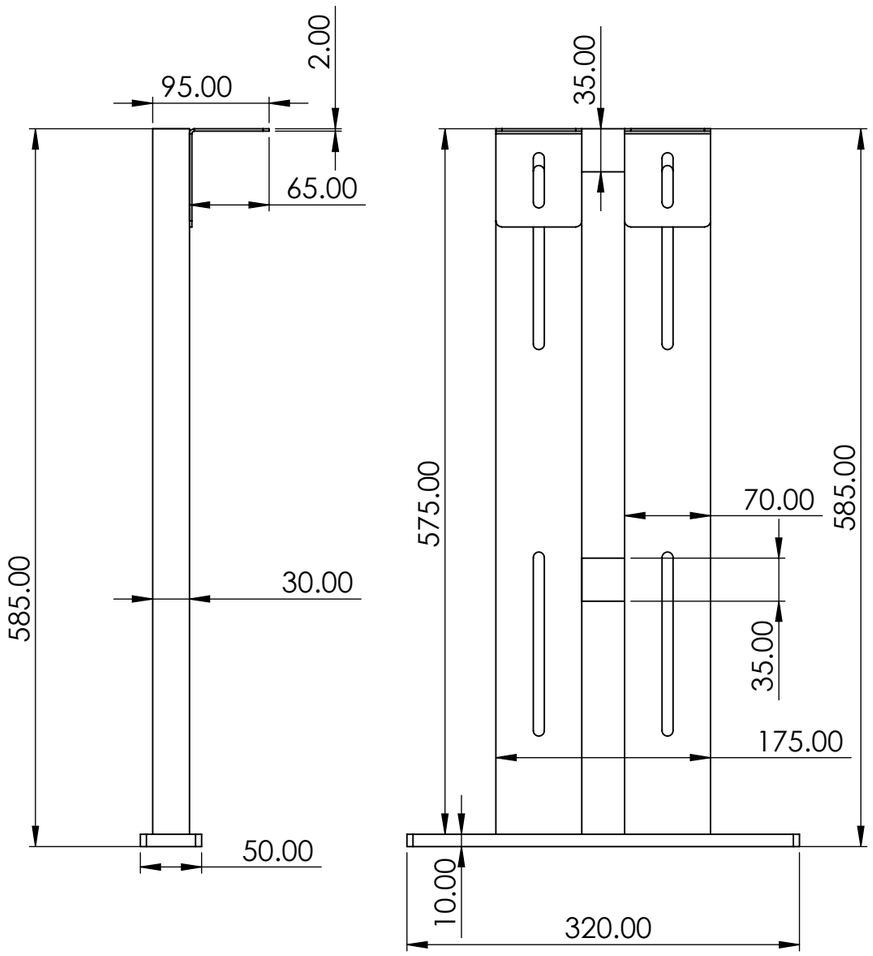


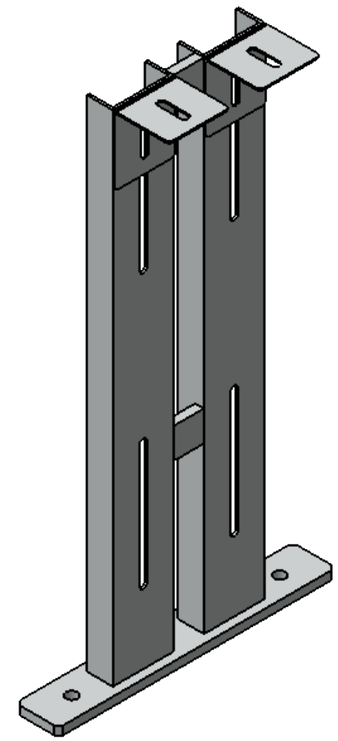



RACK SUPPORT ASM

TITLE - RETRACTABLE ROOF				NIHVA TECHNOLOGIES PVT.LTD.PUNE
DWG NO - NTPL-000-PM-001-12-00-00				Website - www.nihva.com
	NAME	SIGNATURE	DATE	PROJECT NO - NTPL-000-PM
DRAWN	V.W		07-04-2025	PRODUCT - RETRACTABLE ROOF
CHK'D	S.W.		07-04-2025	SITE LOCATION - GUJARAT
APPV'D	V.T.		07-04-2025	
if any queries contact - supportautomation@nihva.com				REVISION - QTY - 1
ALL DIMENSION ARE IN mm		A3		SCALE SHEET 27 OF 28

ITEM NO.	PART NUMBER	DESCRIPTION	QTY.
1	VIJAY BUSBAR FLASHER	STD (LOOSE PART)	8
		Sheet	1

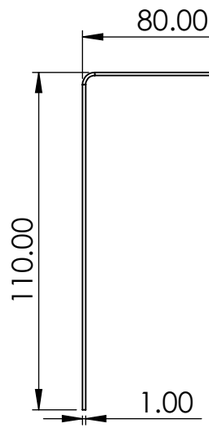

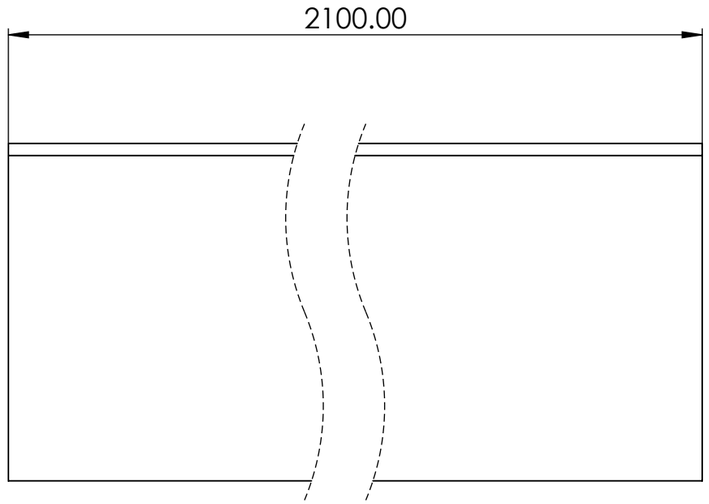

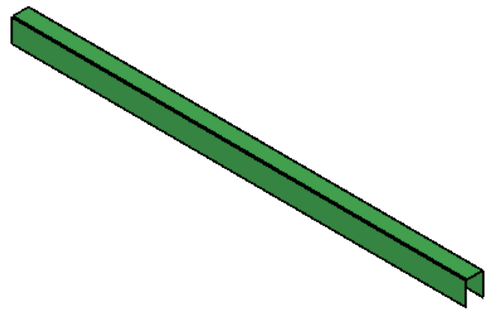

TITLE - RETRACTABLE ROOF				NIHVA TECHNOLOGIES PVT.LTD.PUNE
DWG NO - NTPL-000-PM-001-13-00-00				Website - www.nihva.com
	NAME	SIGNATURE	DATE	PROJECT NO - NTPL-000-PM
DRAWN	V.W		07-04-2025	PRODUCT - RETRACTABLE ROOF
CHK'D	S.W.		07-04-2025	SITE LOCATION - GUJARAT
APPV'D	V.T.		07-04-2025	
if any queries contact - supportautomation@nihva.com				REVISION - QTY - 1
ALL DIMENSION ARE IN mm		A3		SCALE SHEET 28 OF 28