




ELEVATION

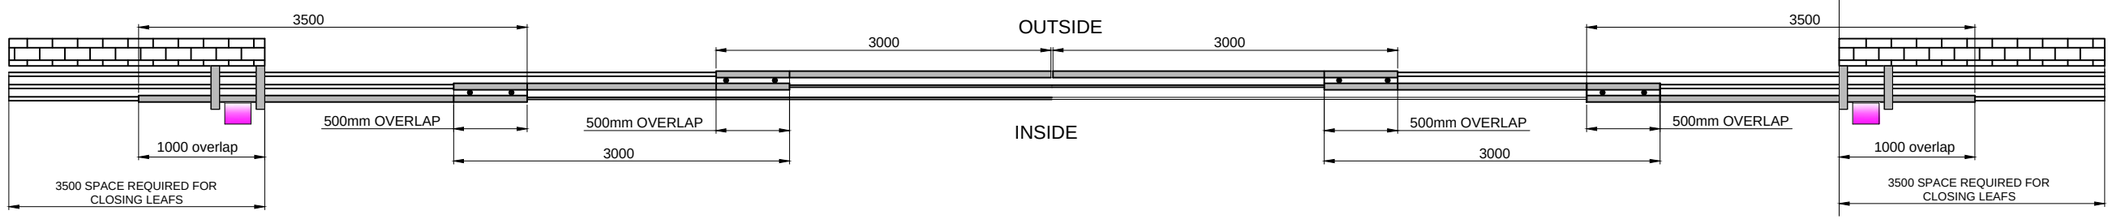

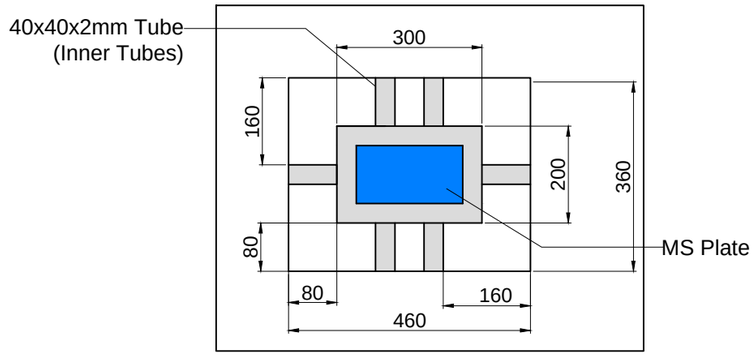

DETAILED VIEW OF A

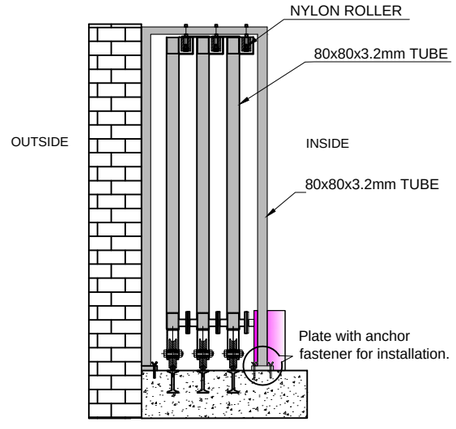

TOLERANCE - ±10mm

Clear Opening size -15000mm x 1500mm
Total No. of Leaf - 6 Leaf
Outer Tube Size-80x80x3.2mm
Inner Tube Size-40x40x2mm
NOTE :- *ALL REQ. CIVIL WORK WILL BE IN CLIENT SCOPE.

SR NO	CLEAR WIDTH	CLEAR WIDTH	QTY.
1	15000mm	1500mm	01NOS

This drawing & design is the property of NIHVA TECHNOLOGIES. Not to be sold or copied to any other concern.

TITLE

TELESCOPIC GATE

	NAME	SIGN	DATE
DRAWN	SURAJ		19-03-2018
CHECK	OMKAR		19-03-2018
APPRD.	PRADEEP		19-03-2018

NIHVA TECHNOLOGIES PVT. LTD.
NIHVA TECHNOLOGIES
PVT. LTD. PUNE
Tel : 020 66304033
Email:- info@nihva.com
Website:- www.nihva.com

CLIENT - ARA CONSTRUCTION.
PROJECT - AUTOGEN INDIA
SITE LOCATION - KHED.
If any queries contact : design@nihva.com
DWG. NO. : NIHVA/17-18/0401
REV- 0
ALL DIMENSION ARE IN mm
SCALE: NTS
WT:
SHEET: 01 OF 01

19-03-2018 15:19:23