CAPACITY	15 TON
PLATFORM SIZE	2500(L) X 2000(W)
POWER PACK	15 HP, 3 PH
SHUT HEIGHT	1000 MM
LIFT HEIGHT	1200 MM
OPEN HEIGHT	2200 MM
RAILING	1000 MM HEIGHT

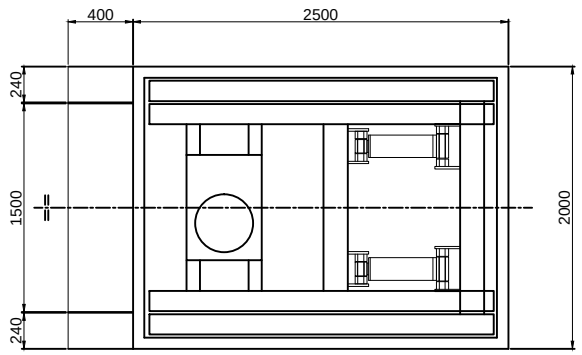

PLAN VIEW

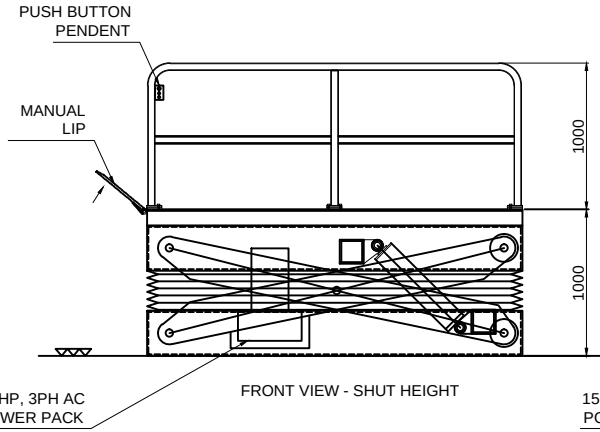

FRONT VIEW - SHUT HEIGHT

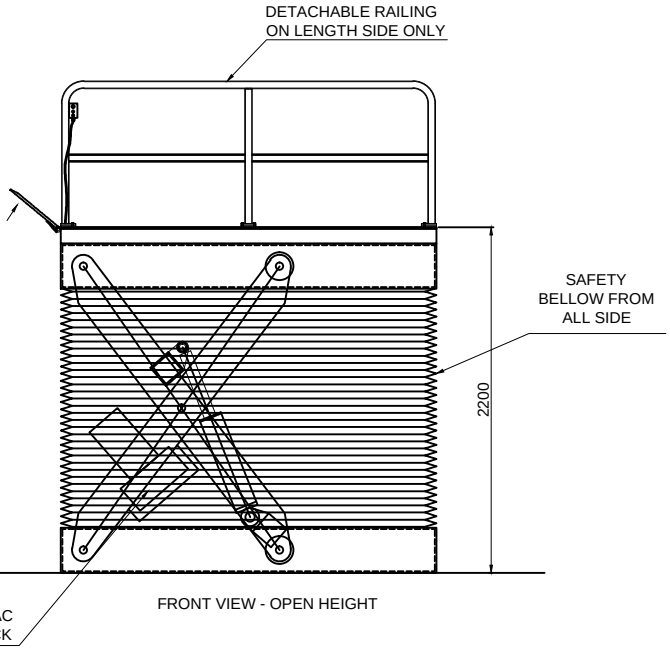

FRONT VIEW - OPEN HEIGHT

NOTE :
1. CONTROL PANEL MOUNTING WILL BE 5 MTR AWAY FROM PIT LOCATION.
2. ALL REQ. TECHNICAL CIVIL WORK WILL BE IN CLIENT SCOPE.

This drawing & designing is the property of NIHVA TECHNOLOGIES. Not to be sold or copied to any other concern.

	NAME	SIGN	DATE
DRAWN	P.A		19.09.20
CHECK	G.J		19.09.20
APPROVAL			

TITLE: ELECTRO HYDRAULIC SCISSOR LIFT

NIHVA TECHNOLOGIES PVT. LTD.
NIHVA TECHNOLOGIES PVT. LTD. PUNE
Tel : 020 66304033
Email:- info@nihva.com
Website:- www.nihva.com

CLIENT - Endress + Hauser Flowtec (India) Pvt. Ltd.
PROJECT - Endress + Hauser Flowtec (India) Pvt. Ltd.
SITE LOCATION - AURANGABAD

If any queries contact : design@nihva.com
DWG. NO. : NIHVA/20-21/0056 REV- R00
ALL DIMENSION ARE IN mm
SCALE: NTS WT: SHEET: 01 OF 01