

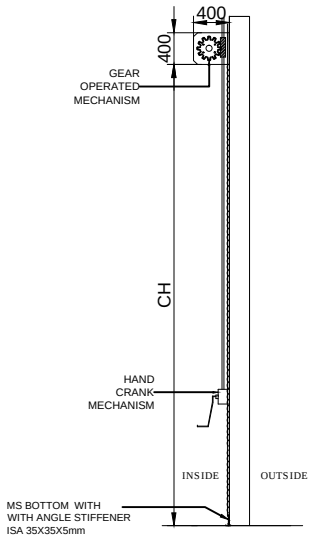



SIDE VIEW

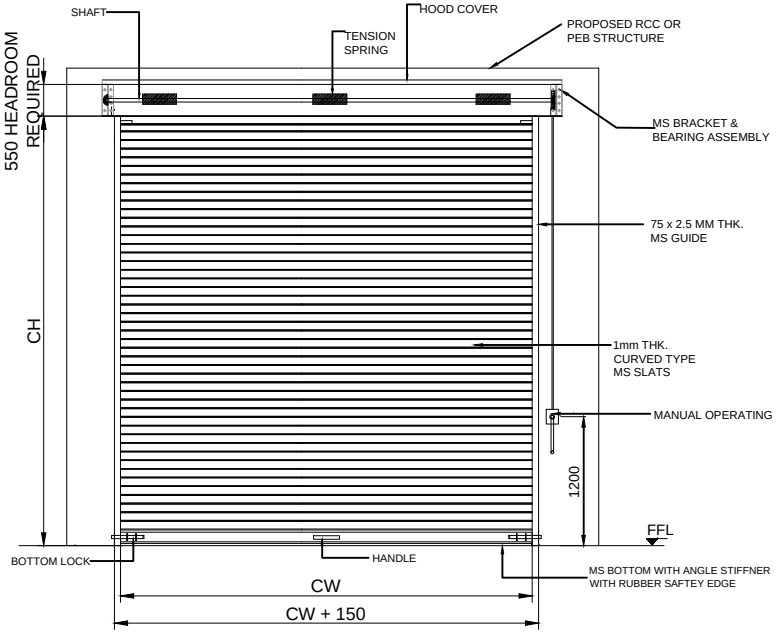


INSIDE ELEVATION

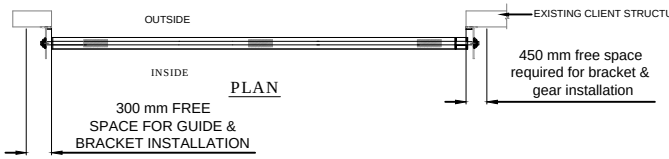


PLAN

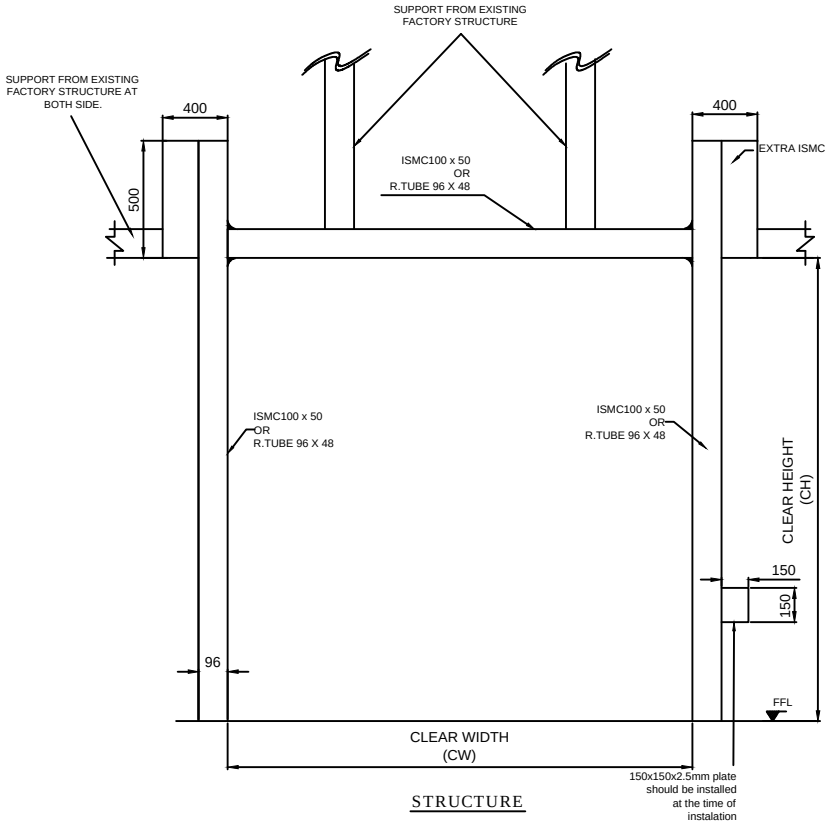

STRUCTURE

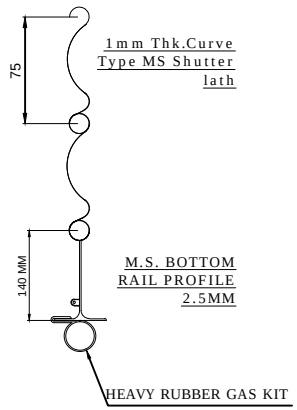

M.S. BOTTOM RAIL PROFILE 2.5MM

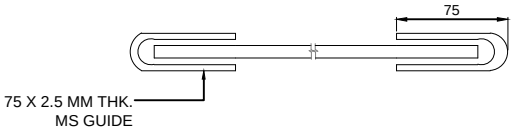

RAL 9010	PURE WHITE	
RAL 9002	GREY WHITE	
RAL 7035	LIGHT GREY	
RAL 5002	ULT. M. BLUE	
RAL CODE	RAL COLOR	APPROVED

SR NO	(CW) CLEAR WIDTH	(CH) CLEAR HEIGHT	QUANTITY
3	2500	3600	01 NO
2	2400	3600	01 NO
1	2400	3000	02 NOS

NOTE-
1. ALL CIVIL WORK WILL BE CLIENT'S SCOPE.
2.IF STRUCTURE REQUIRED FOR SHUTTER IS IN CLIENT'S SCOPE.

TOLERANCE - ±10mm

REV NO	DATE	DRAWN	REMARK
R01	23.06.20	P.A	1.STRUCTURE DETAIL ADDED

This drawing & design is the property of NIHVA TECHNOLOGIES. Not to be sold or copied to any other concern.

TITLE
GEAR OPERATED ROLLING SHUTTER

	NAME	SIGN	DATE
DRAWN	P.A		20.06.2020
CHECK	G.J		20.06.2020
APPRD.			

NIHVA TECHNOLOGIES PVT. LTD.
NIHVA TECHNOLOGIES PVT. LTD. PUNE
Tel : 020 66304033
Email:- info@nihva.com
Website:- www.nihva.com

CLIENT - RMK INFRASTRUCTURE
PROJECT -
SITE LOCATION - TALEGAON,PUNE.
If any queries contact : design@nihva.com
DWG. NO. : NIHVA/20-21/0023/R01
REV- R01
ALL DIMENSION ARE IN mm
SCALE: NTS
WT:
SHEET: 01 OF 01