


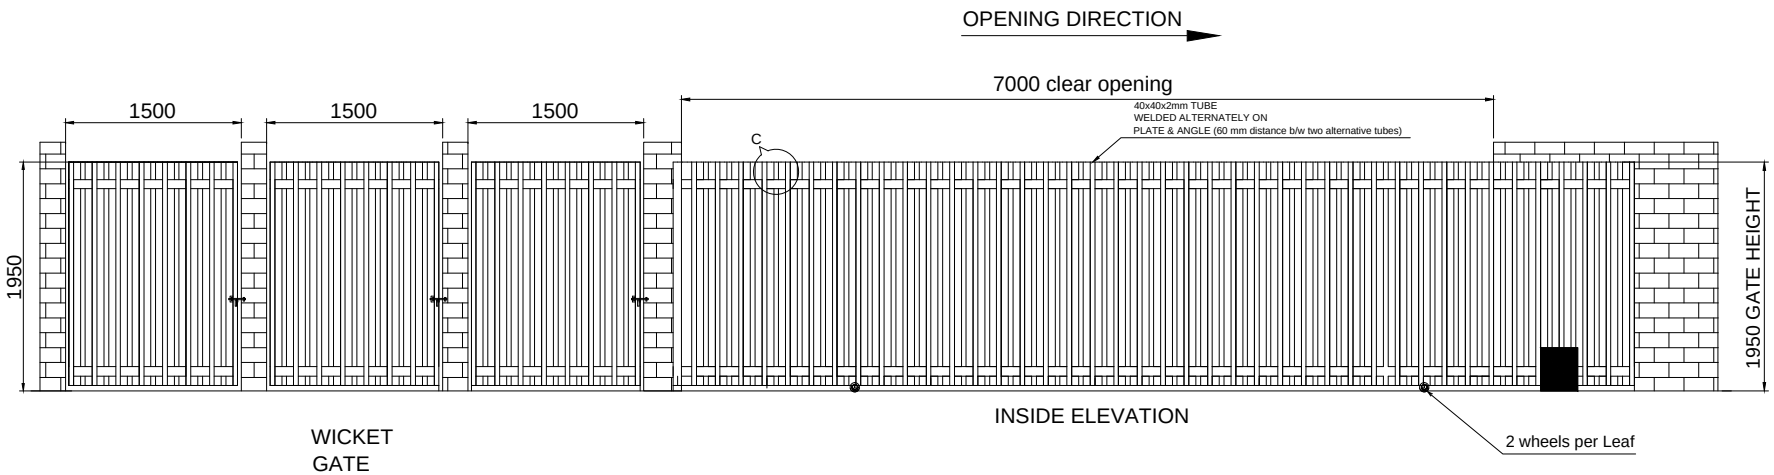


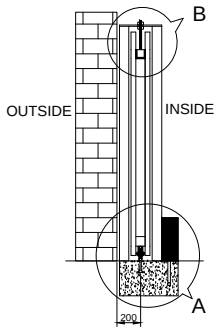


SIDE VIEW

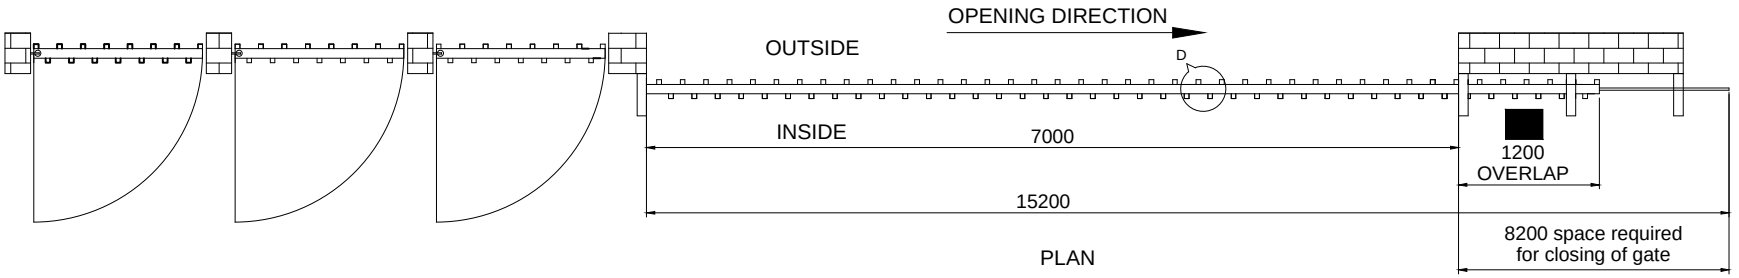


PLAN

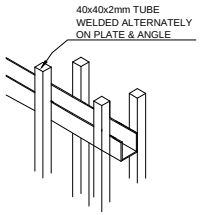


DETAIL VIEW OF C

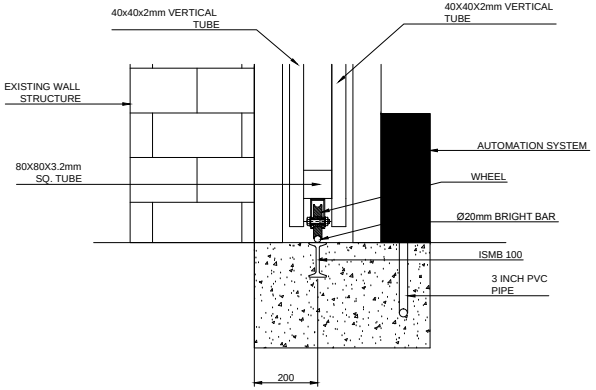

DETAILED VIEW OF A

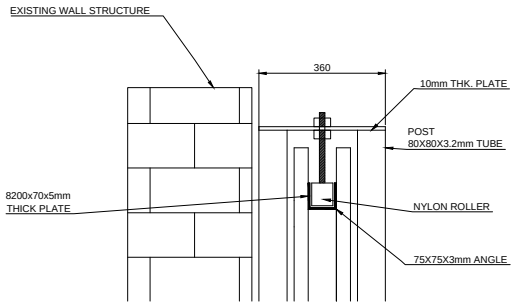

DETAILED VIEW OF B

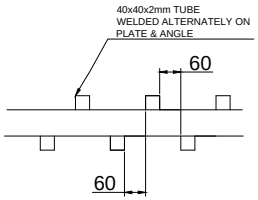

DETAILED VIEW OF D

MOTORISED SINGLE LEAF SLIDING GATE & WICKET GATE

DESCRIPTION	CLEAR WIDTH	OVERALL WIDTH	CLEAR HEIGHT	QTY.
SLIDING GATE	7000	8200	1950	1 NOS
WICKET GATE	1500		1950	3 NOS

NOTE- ALL REQUIRED CIVIL WORK WILL BE IN CLIENT'S SCOPE.

This drawing & designing is the property of NIHVA TECHNOLOGIES. Not be sold or copy to any other concern.

TITLE: SINGLE LEAF MOTORIZED SLIDING GATE & WICKET GATE

NIHVA TECHNOLOGIES PVT. LTD.
NIHVA TECHNOLOGY PVT. LTD. PUNE
Tel : 020 66304033
Email:- info@nihva.com
Website:- www.nihva.com

	SIGN	DATE
DRAWN	OMKAR	05/07/16
CHECK	ANIL	05/07/16
REV.	02	
APPROVAL		

If any queries contact : projects@nihva.com

ALL DIMENSION ARE IN mm

CLIENT - MAHENDRA WINDOOR SOLUTIONS

PROJECT - AUROBINDO PHARMA LIMITED

SITE -

DWG. NO. : NIHVA/16-17/0026/R03

SCALE: NTS | WT: | SHEET: 01 OF 01