

THIS PRINT IS THE PROPERTY OF NIHVA IT IS TO BE USED ONLY FOR THE PURPOSE FOR WHICH IT WAS LENT AND MUST NOT BE USED IN ANY WAY DERTIMENTAL TO THE INTEREST OF THIS COMPANY AND IS SUBJECT TO RETURN ON DEMAND.

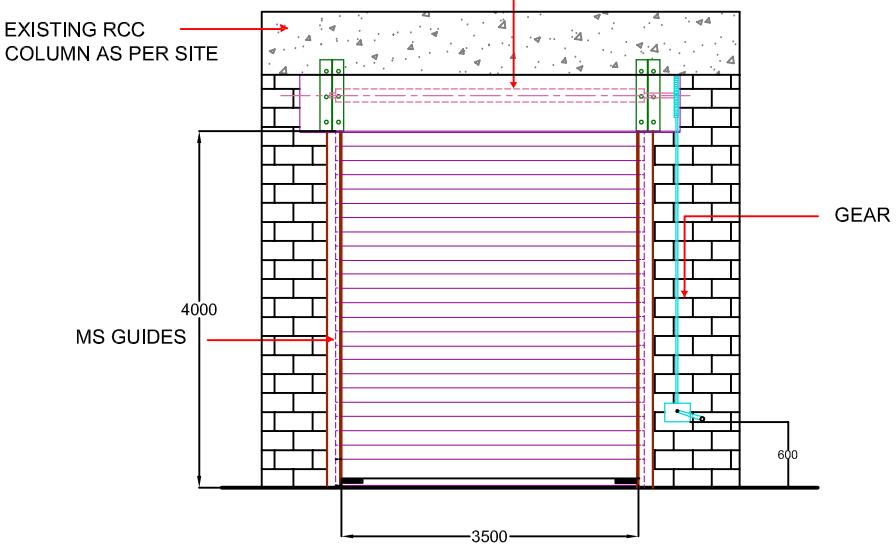


INSIDE ELEVATION


Clear Opening size:-
(W)3.5m x (H)4.0m

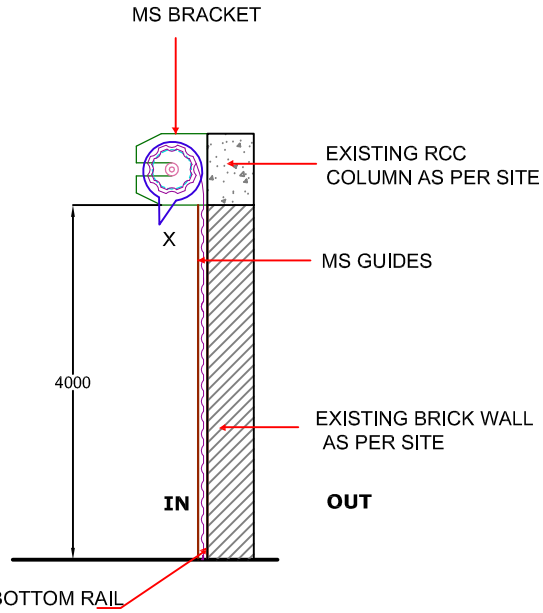


SIDE VIEW

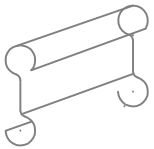


Box/Straight Type Slat Profile

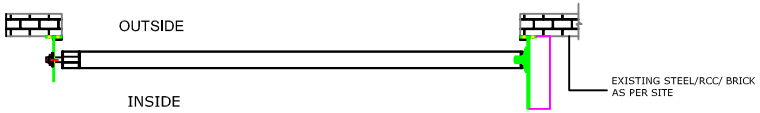

PLAN

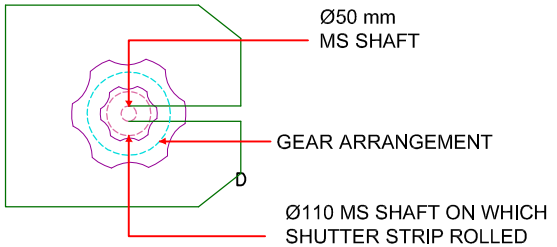

Bracket

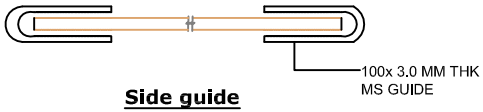

Side guide

Location :- Substation
Size :- 3.5m(W) X 4.0M (H)
Qty :- 03 nos
Type :- RS5

TITLE: Manual Gear Operated Rolling Shutter	DO NOT SCALE DRAWING		NIHVA TECHNOLOGIES PVT. LTD. Pune:-411044 Tel :- 020 66304033 Email :- info@nihva.com
CLIENTS APPROVEL:-		SIGN / DATE	
	DRAWN	Anil	CLIENT: Shapoorji Palonji Co. Ltd
	CHECK		PROJECT / SITE: GE,CHAKAN
	ENG		PRODUCT NAME:
	APPRD.		DWG. NO.: NVA/SP/04R
UNLESS & OTHERWISE SPECIFIED DIMENSION ARE IN M.M.	PROD		REV.: 0
	MFG		SCALE: NTS WT: SHEET: 1 OF 1
	Ref. No.		