


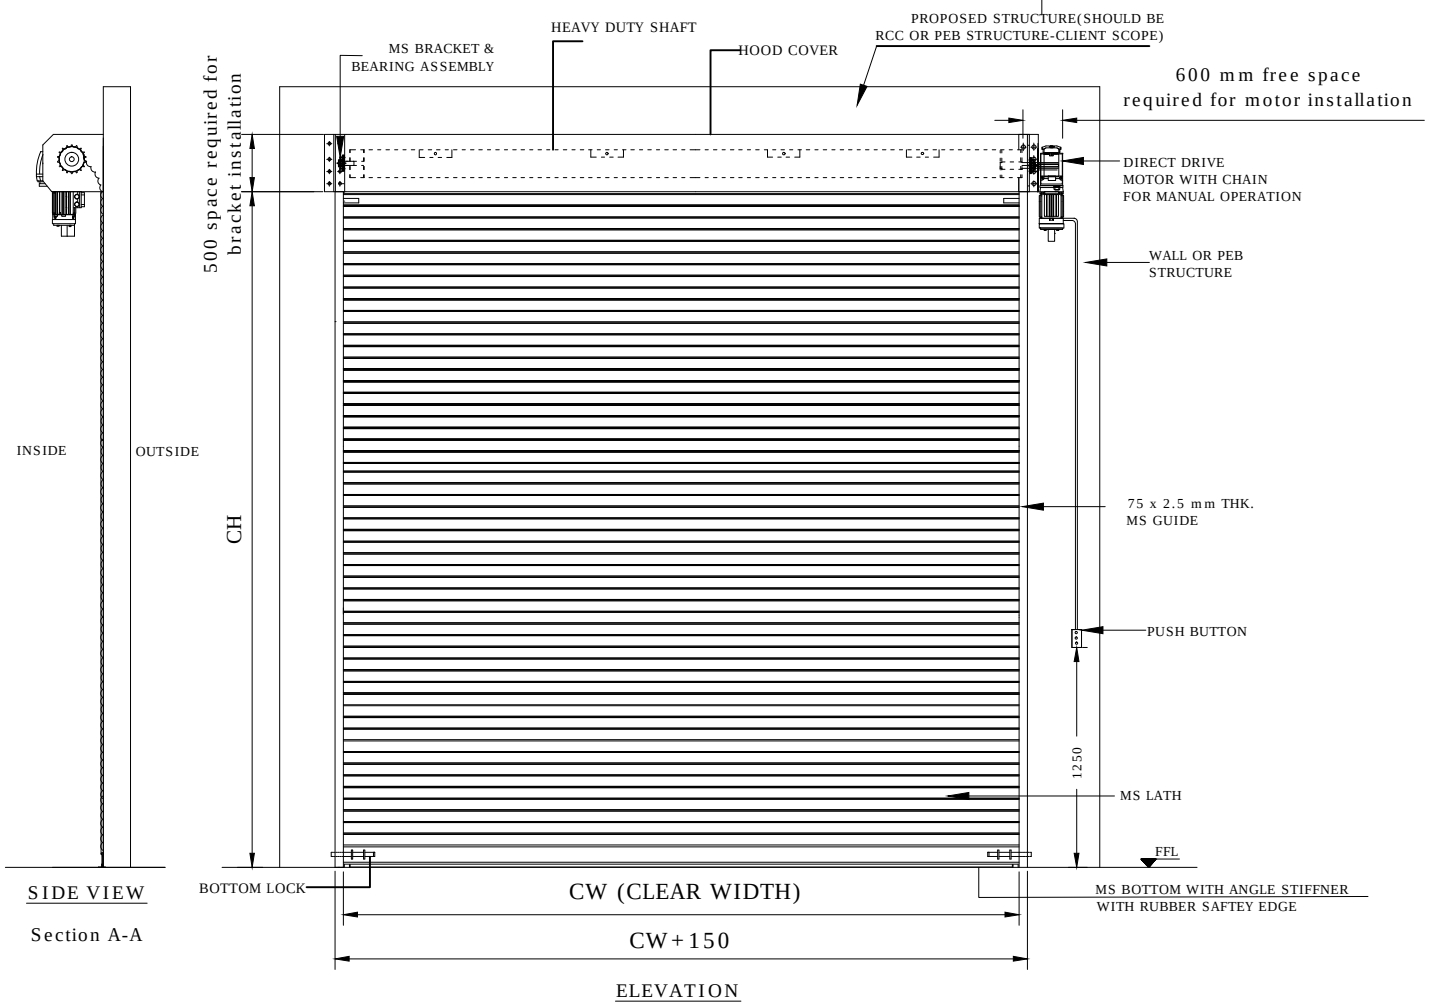


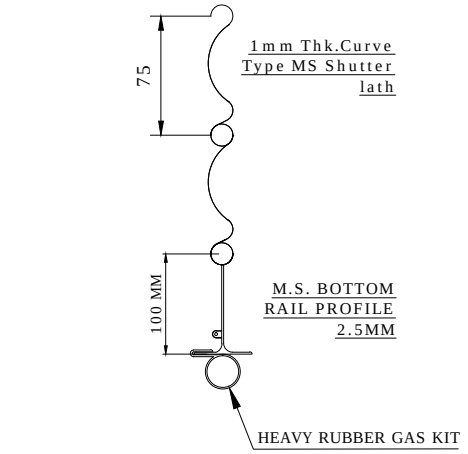

M.S. BOTTOM RAIL PROFILE 2.5MM

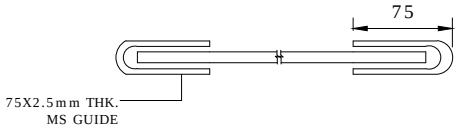

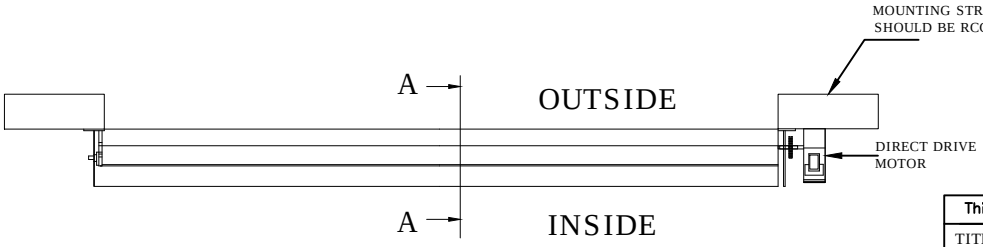

TOLERANCE - ±10mm

CLEAR WIDTH (CW)	CLEAR HEIGHT (CH)	QUANTITY
4000	4000	02 NO

NOTE-
1.ONE COAT OF RED OXIDE WILL BE GIVEN TO SHUTTER (ONLY MS PART). PAINT OF APPROVED RAL SHADE WILL BE GIVEN TO THE SHUTTER.
2. HOOD COVER WILL BE IN GI.
3.THREE PHASE SUPPLY SHOULD BE GIVEN TO THE SHUTTER.
4.ALL CIVIL WORK & STRUCTURE WILL BE IN CLIENT'S SCOPE.

This drawing & design is the property of NIHVA TECHNOLOGIES. Not to be sold or copied to any other concern.

TITLE: MOTORIZED ROLLING SHUTTER

	NAME	SIGN	DATE
DRAWN	SURAJ		20.09.2018
CHECK	P.A		20.09.2018
APPRD.	R.D		20.09.2018

NIHVA TECHNOLOGIES PVT. LTD.
NIHVA TECHNOLOGIES PVT. LTD. PUNE
Tel : 020 66304033
Email:- info@nihva.com
Website:- www.nihva.com

CLIENT -RELIABLE CONSTROTECH ENTERPRISES.

PROJECT -

SITE LOCATION - SATARA.

If any queries contact : design@nihva.com

DWG. NO. : NIHVA/18-19/0130 | REV- 0

ALL DIMENSION ARE IN mm | SCALE: NTS | WT: | SHEET: 01 OF 01