NIHVA
NIHVA Technologies Pvt. Ltd.

OPERATION & MAINTENANCE MANUAL FOR HIGH SPEED DOOR

CLIENT: CONGLOMERATE

PROJECT: CONGLOMERATE

MFG.YEAR: 2021



DESIGNED, DEVELOPED & MARKETED BY

NIHVA
NIHVA Technologies Pvt. Ltd.

Address- G-BLOCK, 1ST FLOOR, THERMAX CHOWK MIDC, ABOVE RENAULT SHOWROOM CHINCHWAD, PUNE-411019
TEL.NO: - +912066304033
EMAIL: -info@nihva.com

www.nihva.com

PRODUCT - HIGH SPEED DOOR	
PRODUCT SIZE	3415 mm (CW) X 4300 mm (CH)
PO NO	
PREPARED BY	SIDDHESHWAR SHELAKE
DATE	25.01.2021

DESPATCH & UNLOADING

1. Loading, for dispatch, will be our responsibility. On receipt of the High speed door at site, please check and ensure that there is no physical damage to the equipment.

2. While unloading the equipment from the transporting vehicle, please ensure to use slings with rated capacity higher than the gross weight of the Stationary lift in packed condition.

ORDERING OF SPARES

1. When ordering for spare, please specify the following in your Purchase Order.

   - High speed door Size
   - Part name / Description
   - Quantity required
   - Delivery period / time
   - Mode of dispatch

   This would avoid ambiguity and help us serve you better.

❖ EMERGENCY CONTACT DETAILS: -

1) Service Department - 9168938333
2) Project Department - 8551095333

NIHVA
NIHVA Technologies Pvt. Ltd.

SPECIFICATIONS:

1. SIZE: 3400 (CW) X 4300(CH)
2. MANUFACTURING YEAR – 2021
3. OPENING SPEED – 1.5M/SEC
4. CLOSING SPEED- 0.8M/SEC
5. MOTOR POWER- 1.1 kW
6. CONNECTING VOLTAGE- 230V, 50Hz
7. PROTECTION CATEGORY – IP54

INTRODUCTION: -

HIGH SPEED DOOR is the result of many years' experience in Door Automation Technologies. "NIHVA" offers the best possible factor of safety with simple, easy to use controls. The high quality of manufacture gives a robust construction and many years of useful life.

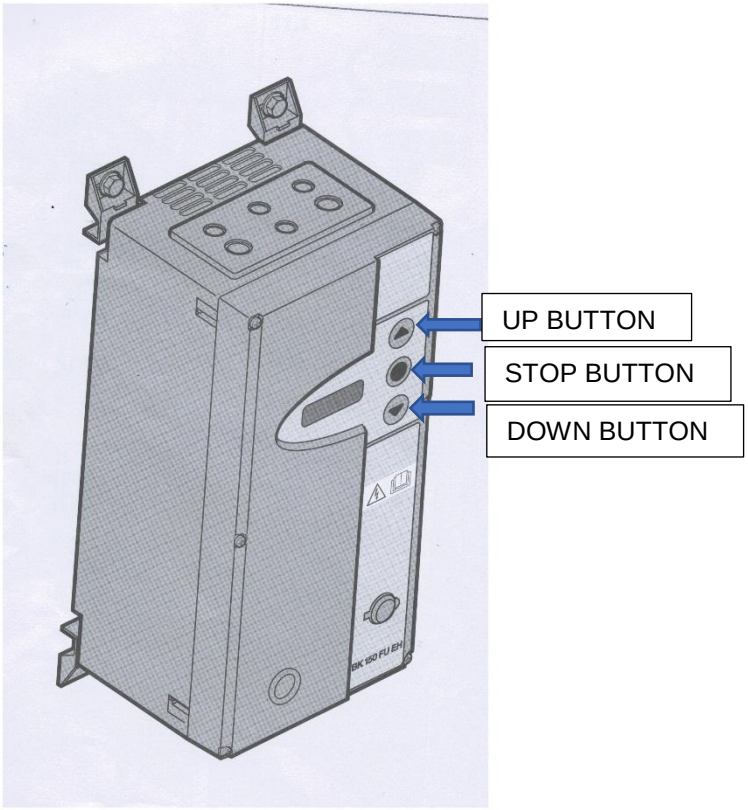
We take pride that our product & service range is offered with a high level of working safety, comfort, functionality and supported by services and added value solutions.

PRE – OPERATING INSTRUCTIONS: -

1. The door system may only be operated by persons who have been instructed in its proper use.
2. The door system opens & closes vertically upwards & downwards. When in operation, make sure that neither persons-children in particular- nor objects are located within the door's area of travel.
3. You are responsible for ensuring that children cannot operate door system, neither via the control nor control elements.
4. Wait until the door has come to a complete halt before walking/driving into the door's area of travel.
5. Never use the door to lift objects and/or persons.
6. Whenever driving in or out of the opening, always check that the door curtain has travelled up far enough to provide the necessary passage height.
7. Only ever operate the door system when all the protective devices & safety equipment's are fitted & are in perfect working order.

8. Do not dismantle or alter any of the protective devices. Do not put any of the protective devices out of operation.
9. Protect the door from aggressive & caustic substances in order to avoid damage due to incorrect handling of door system.
10. The door system is intended for temperature range of -20^0C to $+60^0$C & relative humidity is 0% to 60%.
11. In the case of malfunction call NIHVA immediately for inspect & repair the door system.
12. Only use original spare parts. They always meet the technical requirements laid out by us.

OPERATING PUSH BUTTONS: -



ROUTINE MAINTENANCE

As the owner or operator of the door, you must have the system inspected & maintained by NIHVA/specialist once a year in. In the case of more than 50000 door cycles per year, every 6 months.

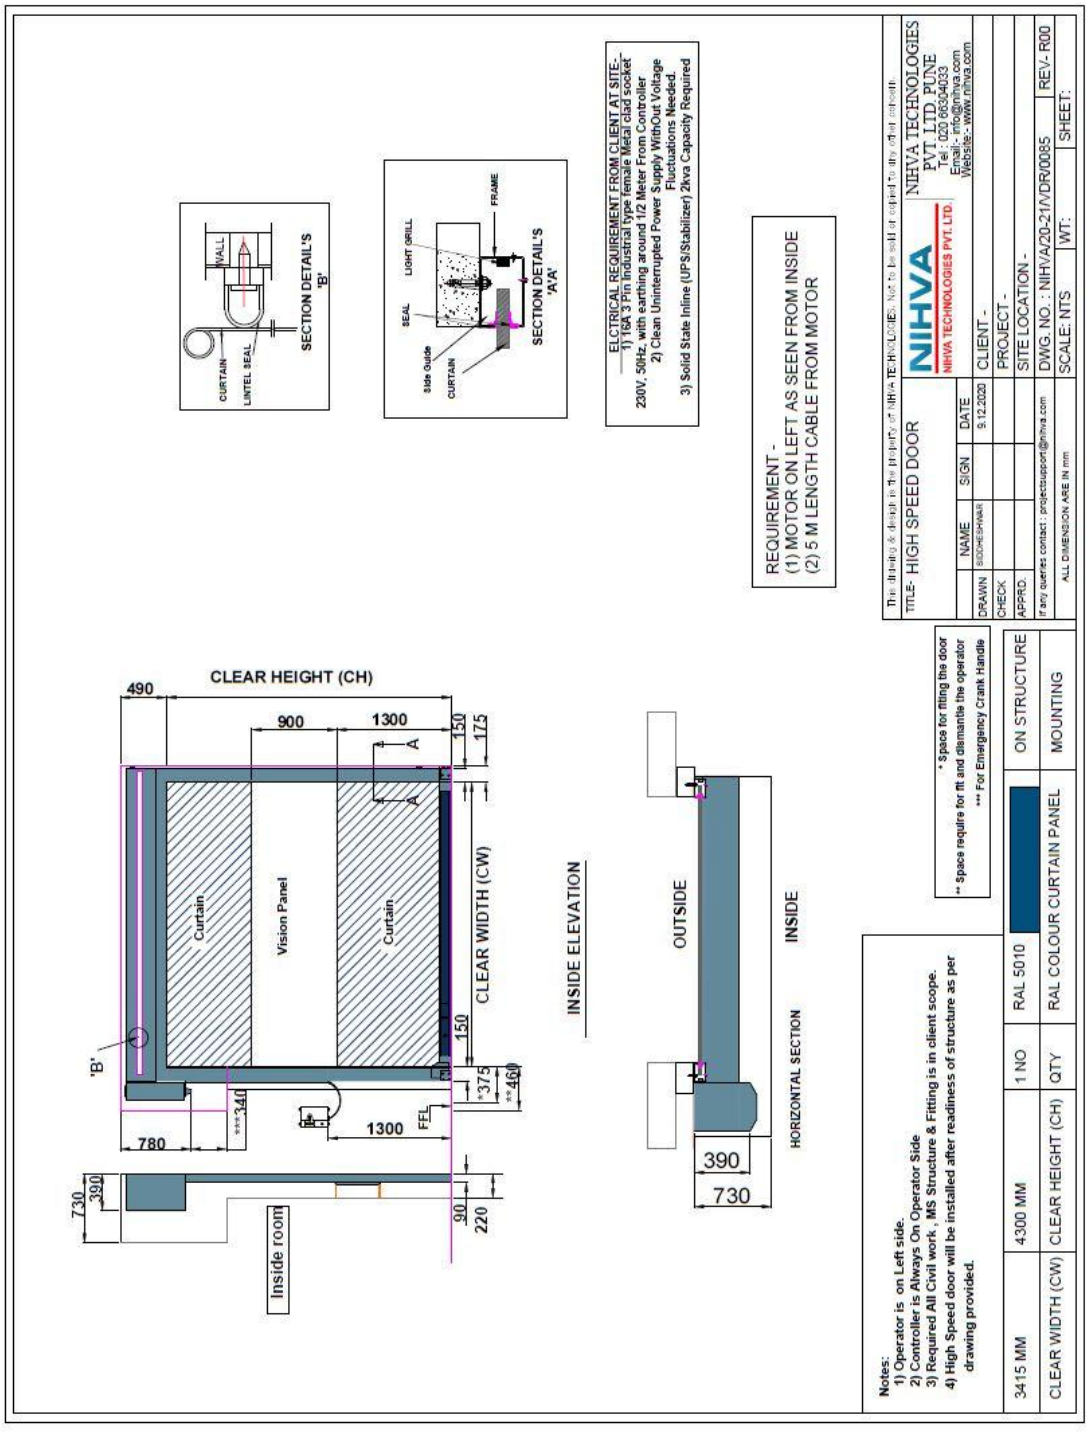
DAILY:

1. Do visual inspection for mechanical damage to product.
2. Ensure proper voltage & all electrical connections are proper before operating.
3. Clean the lenses & reflectors regularly with a soft, dry lint-free towel.

EMERGENCY OFF-

In emergency situations, de-energize the control by actuating the main switch, pulling the mains plug or, if available, actuating the red emergency-OFF button.

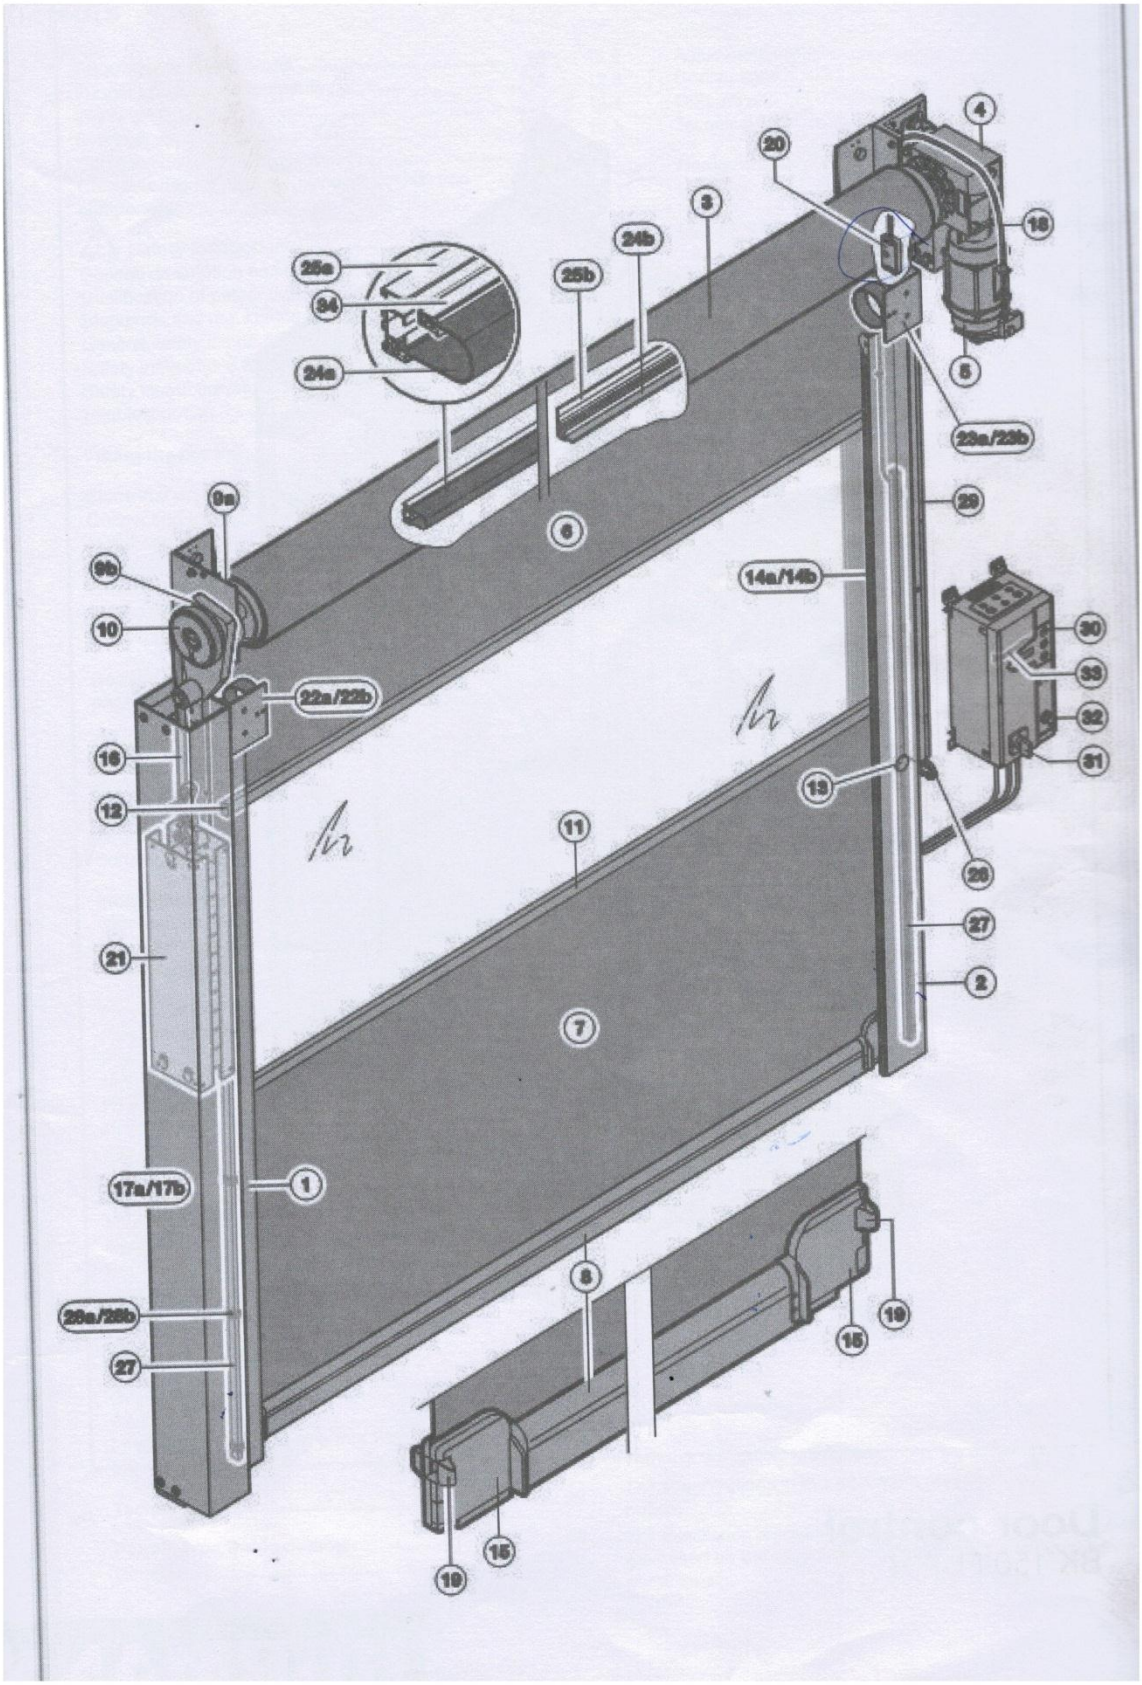
GA DRAWING:


CLEAR HEIGHT (CH)
490
900
1300
150
175
A
A
Curtain
Vision Panel
Curtain
CLEAR WIDTH (CW)
150
375
460
340
780
1300
FFL
'B'
730
390
90
220
Inside room
INSIDE ELEVATION
OUTSIDE
INSIDE
390
730
HORIZONTAL SECTION
SECTION DETAIL'S 'B'
WALL
CURTAIN
LINTEL SEAL
SECTION DETAIL'S 'A'A'
SEAL
LIGHT GRILL
FRAME
Side Guide
CURTAIN
ELCTRICAL REQUIREMENT FROM CLIENT AT SITE:-
1) 16A 3 Pin Industrial type female Metal clad socket
230V, 50Hz, with earthing around 1/2 Meter From Controller
2) Clean Uninterrupted Power Supply WithOut Voltage Fluctuations Needed.
3) Solid State Inline (UPS/Stabilizer) 2kva Capacity Required
REQUIREMENT -
(1) MOTOR ON LEFT AS SEEN FROM INSIDE
(2) 5 M LENGTH CABLE FROM MOTOR
* Space for fitting the door
** Space require for fit and dismantle the operator
*** For Emergency Crank Handle
Notes:
1) Operator is on Left side.
2) Controller is Always On Operator Side
3) Required All Civil work , MS Structure & Fitting is in client scope.
4) High Speed door will be installed after readiness of structure as per drawing provided.
3415 MM | 4300 MM | 1 NO | RAL 5010 | ON STRUCTURE
CLEAR WIDTH (CW) | CLEAR HEIGHT (CH) | QTY | RAL COLOUR CURTAIN PANEL | MOUNTING
NIHVA TECHNOLOGIES PVT. LTD. PUNE
Tel: 020 66304033
Email: info@nihva.com
Website: www.nihva.com
NIHVA TECHNOLOGIES PVT. LTD.
TITLE- HIGH SPEED DOOR
NAME | SIGN | DATE
DRAWN | SIDDHESHWAR | | 9.12.2020
CHECK
APPRD.
CLIENT -
PROJECT -
SITE LOCATION -
If any queries contact : projectsupport@nihva.com
DWG. NO. : NIHVA/20-21/V/DR/0085 | REV- R00
ALL DIMENSION ARE IN mm
SCALE: NTS | WT: | SHEET:

SPARE PARTS-

Sr No	Item
1	Side assembly bearing side
2	Side assembly operator side
3	Shaft
4	Operator
5	Brake
6	Anti-static curtain
7	Anti-static curtain section
8	Complete bottom part
9a	Flange bearing
9b	Bearing with groove + bearing shell
10	Complete emergency opening guide roller
11	Aluminium wind lock
12	Wind lock end piece
13	Cover plug
14a	Seal for guide
14b	Side assembly brush seal
15	Plastic end piece
16	Transmission
17a	Left counter weight guide box
17b	Right counter weight guide box
18	Bowden cable
19	Radio crash switch
20	Radio crash receiver
21	Counter weight sheet
22a	Automatic re-feed left complete
22b	Complete left return guide bush
23a	Automatic re-feed right complete
23b	Complete right return guide brush
24a	Curtain loop complete

24b	Brush seal
25a	Sealing frame channel
25b	Lintel brush Aluminium
26	Emergency opening Bowden cable handle
27	Light grille
28a	Light grille support
28b	Light grille support
29	Cable duct
30	Keypad
31	Lockable main switch
32	Rotary release emergency-off button
33	Keypad extension
34	Sealing frame clips


4
20
3
18
24b
25a
34
25b
24a
5
22a/22b
9a
29
6
9b
14a/14b
10
30
33
22a/22b
32
16
31
12
13
11
28
27
21
2
7
17a/17b
1
8
28a/28b
19
27
15
19
15