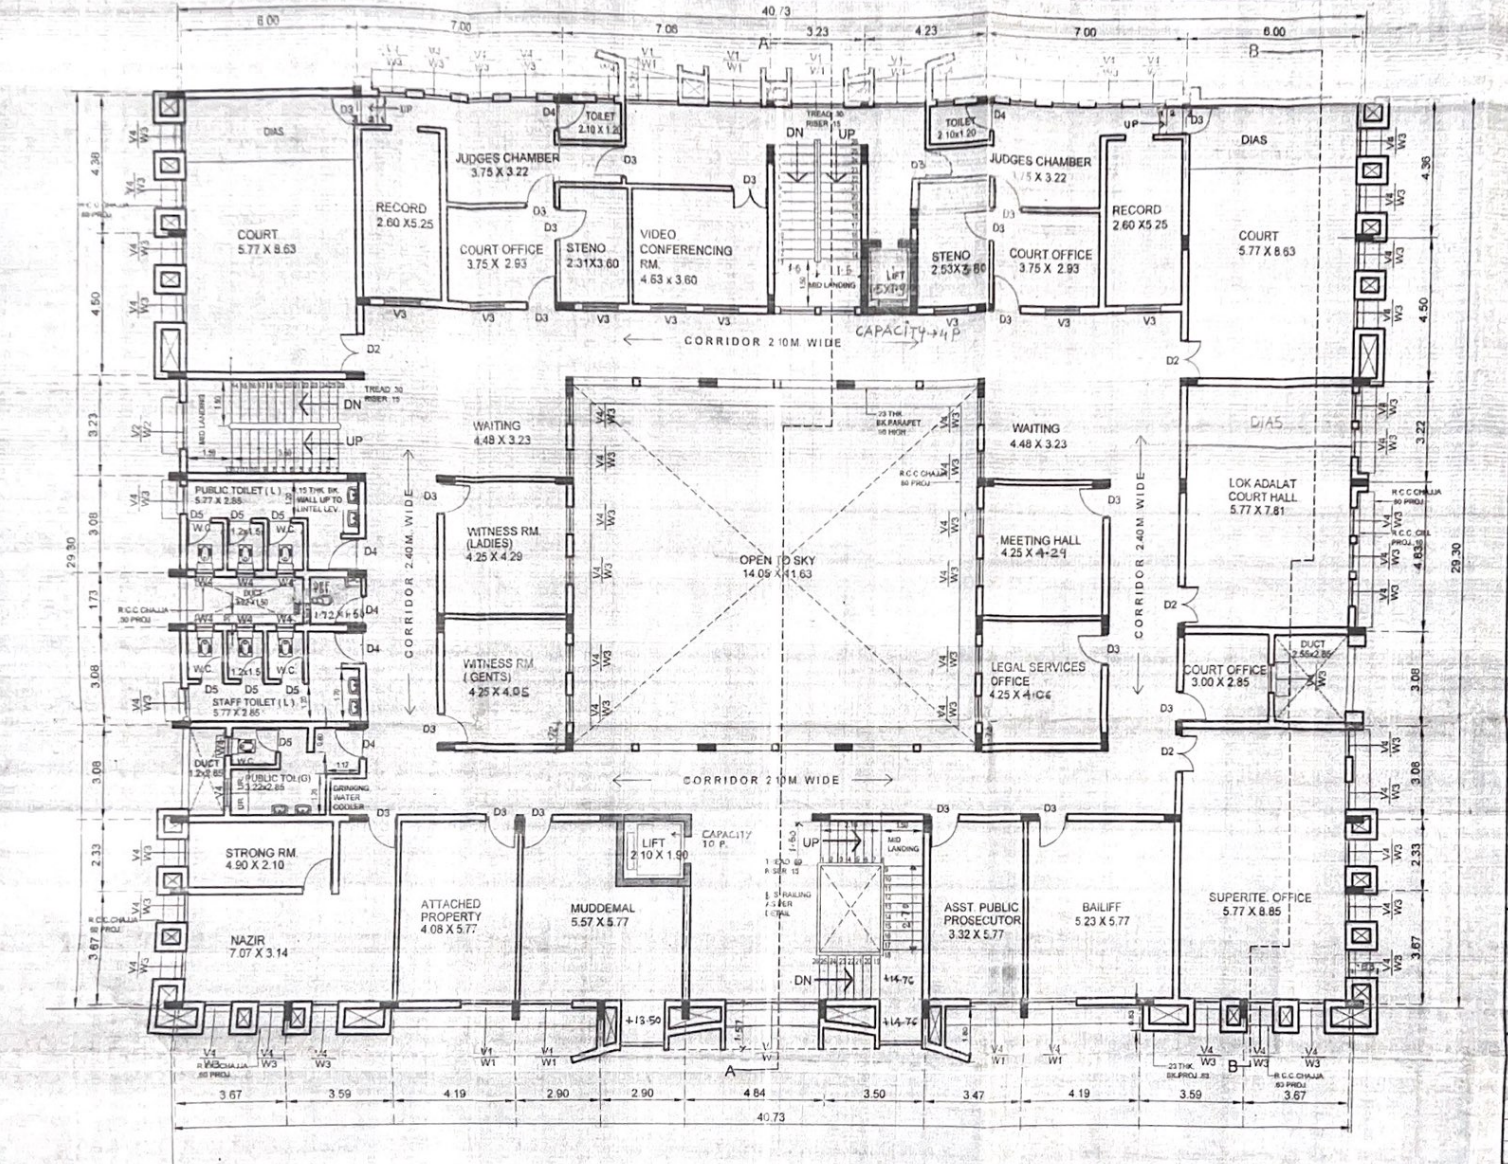
40.73
6.00
7.00
7.06
3.23
4.23
7.00
6.00
A
B
DIAS
JUDGES CHAMBER
3.75 X 3.22
TOILET
2.10 X 1.20
RECORD
2.60 X5.25
COURT
5.77 X 8.63
COURT OFFICE
3.75 X 2.93
STENO
2.31X3.60
VIDEO CONFERENCING RM.
4.63 x 3.60
TREAD 30
RISER 15
DN
UP
MID LANDING
LIFT
STENO
2.53X3.60
CORRIDOR 2.10M WIDE
CAPACITY 4 P
WAITING
4.48 X 3.23
WITNESS RM. (LADIES)
4.25 X 4.29
WITNESS RM. (GENTS)
4.25 X 4.05
OPEN TO SKY
14.05 X 11.63
23 THK. BK PARAPET 90 HIGH
R.C.C CHAJJA 60 PROJ.
MEETING HALL
4.25 X 4.29
LEGAL SERVICES OFFICE
4.25 X 4.06
CORRIDOR 2.40M WIDE
LOK ADALAT COURT HALL
5.77 X 7.81
COURT OFFICE
3.00 X 2.85
DUCT
2.55x2.85
PUBLIC TOILET (L)
5.77 X 2.85
115 THK. BK WALL UP TO LINTEL LEV.
STAFF TOILET (L)
5.77 X 2.85
W.C.
1.2x1.5
DUCT
PUBLIC TOI.(G)
3.22x2.85
GRINDING WATER COOLER
STRONG RM.
4.90 X 2.10
NAZIR
7.07 X 3.14
ATTACHED PROPERTY
4.08 X 5.77
MUDDEMAL
5.57 X 5.77
LIFT
2.10 X 1.90
CAPACITY 10 P.
SS RAILING AS PER DETAIL
ASST. PUBLIC PROSECUTOR
3.32 X 5.77
BAILIFF
5.23 X 5.77
SUPERITE. OFFICE
5.77 X 8.85
+13.50
+14.76
D2
D3
D4
D5
V1
W1
V2
W2
V3
V4
W3
4.38
4.50
3.23
3.08
1.73
3.08
3.08
2.33
3.67
29.30
4.36
4.50
3.22
4.836
3.08
3.08
2.33
3.67
3.59
4.19
2.90
2.90
4.84
3.50
3.47
4.19
3.59
3.67
40.73
23 THK. BK.PROJ. 83
R.C.C CHAJJA 60 PROJ

THIRD FLOOR PLAN
BUILT UP AREA =1012.64SQ.M.

AUTHORITY.

THIS WORKING DRAWING IS PREPARED ON THE BASIS OF LINE PLANS APPROVED BY THE PRINCIPAL DISTRICT & SESSIONS [illegible] COMMITTED TO THIS OFFICE BY [illegible]

NOTES

ANY DISCREPANCY NOTICED IN THIS DRAWING SHALL BE BROUGHT TO NOTICED OF THE CHIEF ARCHITECT, M.S.P.W.D., MUMBAI BEFORE EXECUTION OF WORK.

ALL DIMENSIONS ARE IN MTS EXCEPT WHEREVER MENTIONED BY UNITS.

ONLY WRITTEN DIMENSIONS ARE TO BE FOLLOWED.

NO.	DATE	SIGN	CONTENTS

REVISIONS

OFFICE OF THE
CHIEF ARCHITECT
MAHARASHTRA STATE P.W.D.
MUMBAI.

B.M. SANKHE
CHIEF ARCHITECT
CA/90/12830

PS Baliwant
P. S. BALIWANT
DY CHIEF ARCHITECT
CA/83/7574

M Kumbhare
M. S. KUMBHARE
ARCHITECT
CA/94/17559

PROPOSED MEERA BHAINDER, JUDICIAL AND CRIMINAL COURT, BUILDING AT MAUJE, GHODBANDER TALUKA - THANE, DIST. THANE. (6 COURT HALLS)

WORKING DRG.
THIRD FLOOR PLAN.

1:100	12/10/12	K.J.KARVE
SCALE	DATE	DELT BY

JOB NO. TNE - 372 / I
DRG. NO. 4

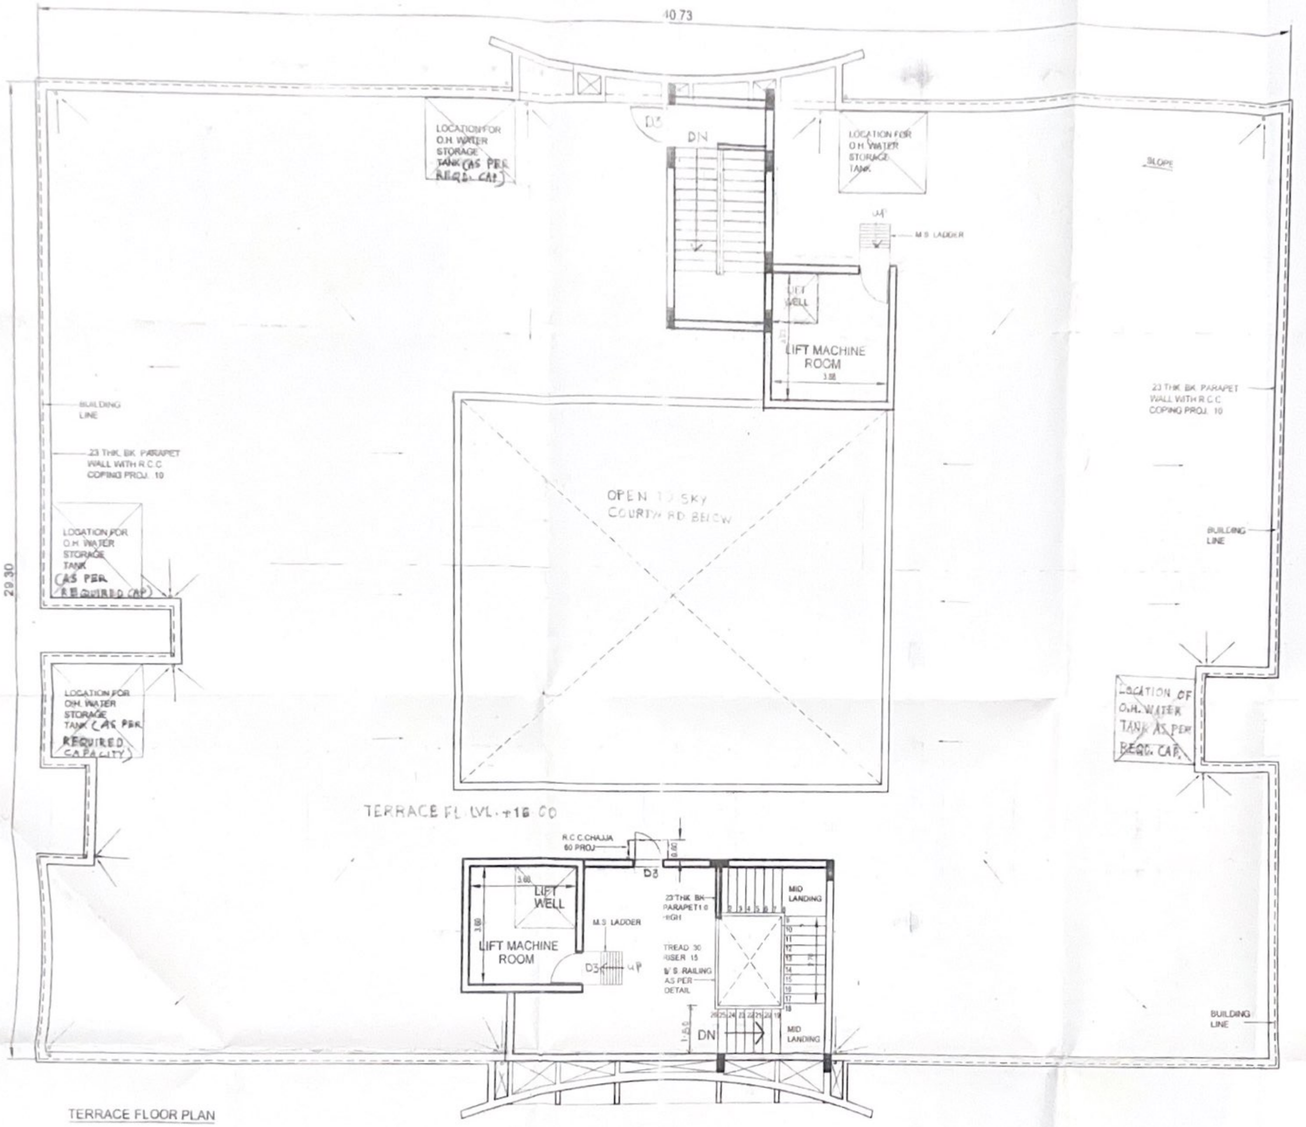
40.73
29.30
LOCATION FOR O.H. WATER STORAGE TANK (AS PER REQD. CAP.)
LOCATION FOR O.H. WATER STORAGE TANK
LOCATION FOR O.H. WATER STORAGE TANK (AS PER REQUIRED CAP)
LOCATION FOR OH. WATER STORAGE TANK (AS PER REQUIRED CAPACITY)
LOCATION OF O.H. WATER TANK AS PER REQD. CAP.
D3
DN
UP
M.S. LADDER
LIFT WELL
LIFT MACHINE ROOM
3.88
SLOPE
BUILDING LINE
23 THK. BK. PARAPET WALL WITH R.C.C. COPING PROJ. 10
OPEN TO SKY COURTYARD BELOW
TERRACE FL. LVL. +16.00
R.C.C. CHAJJA 60 PROJ.
0.60
3.60
23 THK BK PARAPET 1.0 HIGH
TREAD 30 RISER 15
M.S. RAILING AS PER DETAIL
MID LANDING
1.50

TERRACE FLOOR PLAN

AUTHORITY-

THIS WORKING DRAWING IS PREPARED ON THE BASIS OF, **LINE PLANS** APPROVED BY THE PRINCIPAL DISTRICT & SESSIONS JUDGE THANE, CONVEYED TO THIS OFFICE BY EX. ENG. SPECIAL PROJECT (P.W.) DIV. THANE. VIDE HIS LETTER NO. VIPRAVIPRASHA-3/2052 DT 28/06/2012

NOTES

-ANY DISCREPANCY NOTICED IN THIS DRAWING SHALL BE BROUGHT TO NOTICED OF THE CHIEF ARCHITECT, M.S.P.W.D., MUMBAI BEFORE EXECUTION OF WORK

ALL DIMENSIONS ARE IN MTS EXCEPT WHEREVER MENTIONED BY UNITS.

-ONLY WRITTEN DIMENSIONS ARE TO BE FOLLOWED

NO	DATE	SIGN	CONTENTS
1	22.8.13		STAIRCASE BLOCK AT REAR SIDE & WATER TANK AT RIGHT SIDE SHOWN AS PER LR. NO. विप्रवि/मा.वां./अभा-3/2250, DATED-17.07.13 FROM THE EX. ENGR., PW (SP)D, THANE

REVISIONS

OFFICE OF THE
CHIEF ARCHITECT
MAHARASHTRA STATE P.W.D.
MUMBAI.

B.M. SANKHE
CHIEF ARCHITECT
CA/90/12830

P. S. BALWANT
DY CHIEF ARCHITECT
CA/83/7574

Mskumbhare
M. S. KUMBHARE
ARCHITECT
CA/94/17559

PROPOSED MEERA BHAINDER,
JUDICIAL AND CRIMINAL COURT,
BUILDING AT MAUJE,
GHODBANDER TALUKA - THANE,
DIST. THANE. (G COURT HALLS)

WORKING DRG.
TERRACE FLOOR PLAN.

1:100	12/10/12	K.J. KARVE
SCALE	DATE	DELT BY

JOB NO. TNE - 372 / I
DRG. NO. 5

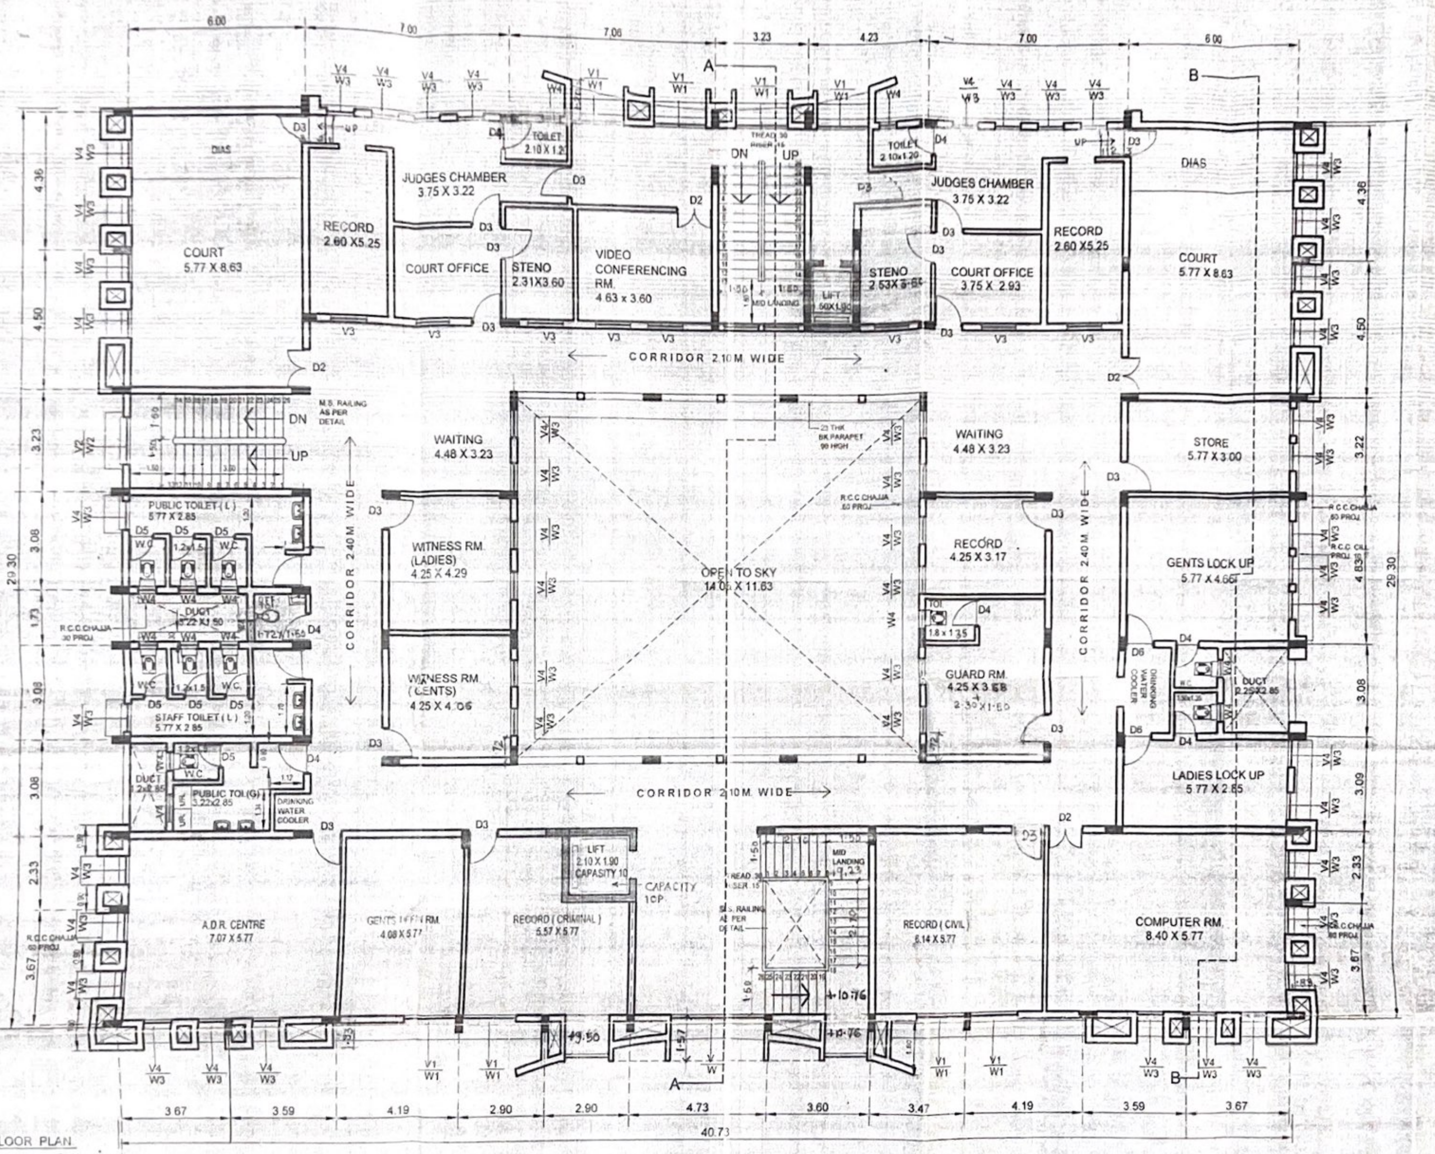
COURT 5.77 X 8.63
DIAS
RECORD 2.60 X5.25
JUDGES CHAMBER 3.75 X 3.22
COURT OFFICE
STENO 2.31X3.60
VIDEO CONFERENCING RM. 4.63 x 3.60
TOILET 2.10 X 1.2
DN
UP
LIFT
STENO 2.53 X 3.6
JUDGES CHAMBER 3.75 X 3.22
COURT OFFICE 3.75 X 2.93
RECORD 2.60 X5.25
COURT 5.77 X 8.63
DIAS
CORRIDOR 2.10M WIDE
WAITING 4.48 X 3.23
WITNESS RM. (LADIES) 4.25 X 4.29
WITNESS RM. (GENTS) 4.25 X 4.06
OPEN TO SKY 14.06 X 11.63
WAITING 4.48 X 3.23
RECORD 4.25 X 3.17
GUARD RM. 4.25 X 3.58
STORE 5.77 X 3.00
GENTS LOCK UP 5.77 X 4.66
LADIES LOCK UP 5.77 X 2.85
DRINKING WATER COOLER
CORRIDOR 2.40M WIDE
PUBLIC TOILET (L) 5.77 X 2.85
STAFF TOILET (L) 5.77 X 2.85
PUBLIC TOI (G) 3.22 X 2.85
DUCT
W.C.
CORRIDOR 2.10M WIDE
A.D.R. CENTRE 7.07 X 5.77
GENTS LEFT RM. 4.08 X 5.77
RECORD (CRIMINAL) 5.57 X 5.77
LIFT 2.10 X 1.90 CAPACITY 10
CAPACITY 10P
RECORD (CIVIL) 6.14 X 5.77
COMPUTER RM. 8.40 X 5.77
M.S. RAILING AS PER DETAIL
R.C.C. CHAJJA
6.00
7.00
7.06
3.23
4.23
7.00
6.00
3.67
3.59
4.19
2.90
2.90
4.73
3.60
3.47
4.19
3.59
3.67
40.73
29.30
4.36
4.50
3.22
3.08
1.73
3.08
3.08
2.33
3.67
A
B

SECOND FLOOR PLAN

BUILT UP AREA =1012.64SQ.M.

AUTHORITY-

THIS WORKING DRAWING IS PREPARED ON THE BASIS OF LINE PLANS APPROVED BY THE PRINCIPAL DISTRICT & SESSIONS JUDGE THANE, CONVEYED TO THIS OFFICE BY EX. ENG. SPECIAL PROJECT (P.W.) DIV., THANE. VIDE HIS LETTER NO.VIPRAVIPRASHA-3/2052 DT 28/06/2012.

NOTES

- ANY DISCREPANCY NOTICED IN THIS DRAWING SHALL BE BROUGHT TO NOTICED OF THE CHIEF ARCHITECT M.S.P.W.D., MUMBAI BEFORE EXECUTION OF WORK.
- ALL DIMENSIONS ARE IN MTS EXCEPT WHEREVER MENTIONED BY UNITS.
- ONLY WRITTEN DIMENSIONS ARE TO BE FOLLOWED.

NO.	DATE	SIGN	CONTENTS

REVISIONS

OFFICE OF THE
CHIEF ARCHITECT
MAHARASHTRA STATE P.W.D.
MUMBAI.

B.M. SANKHE CA/80/12830
CHIEF ARCHITECT

P. S. BALIWANT CA/83/7574
DY.CHIEF ARCHITECT

Mkumbhare

M. S. KUMBHARE CA/94/175
ARCHITECT

PROPOSED MEERA BHAINDER,
JUDICIAL AND CRIMINAL COURT,
BUILDING AT MAUJE,
GHODBANDER TALUKA - THANE,
DIST. THANE. (6 COURT HALLS)

WORKING DRG.
SECOND FLOOR PLAN.

1:100	12/10/12	K.J.KARVE
SCALE	DATE	DELT BY
JOB NO.	TNE - 372 / 1	
DRG. NO.	3	

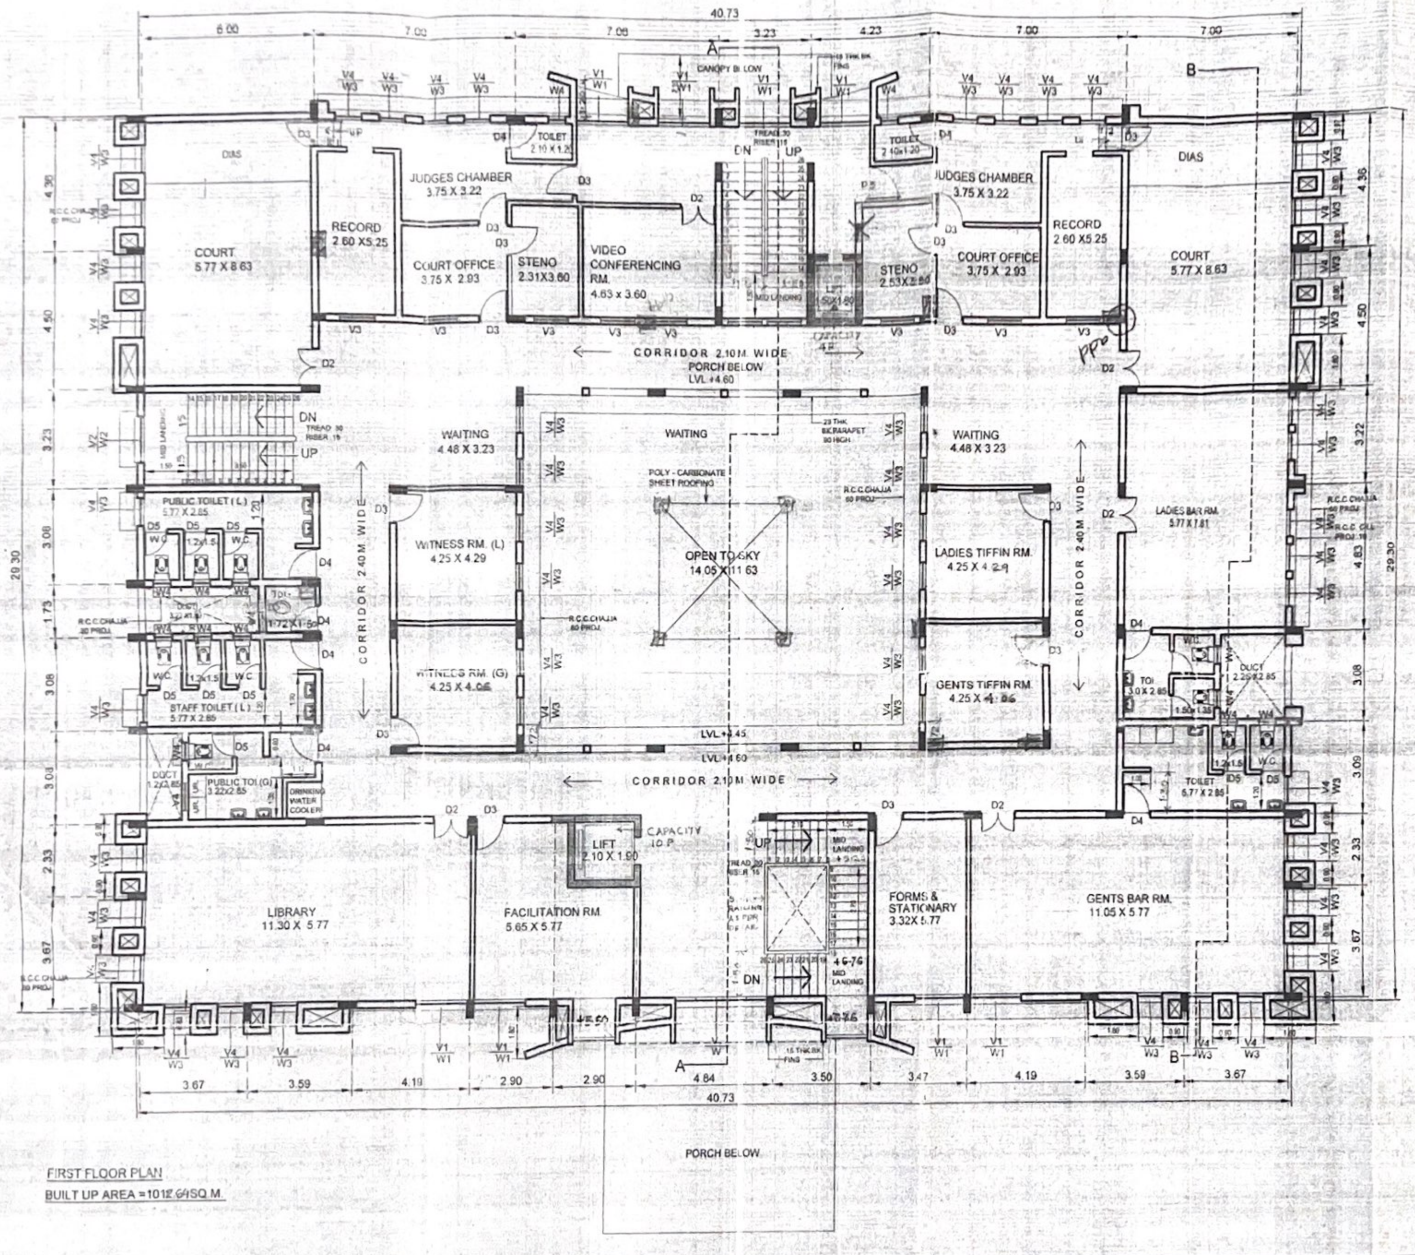
40.73
6.00
7.00
7.06
3.23
4.23
7.00
7.00
CANOPY BELOW
DIAS
RECORD 2.60 X5.25
JUDGES CHAMBER 3.75 X 3.22
COURT 5.77 X 8.63
COURT OFFICE 3.75 X 2.93
STENO 2.31X3.60
VIDEO CONFERENCING RM. 4.63 x 3.60
TOILET 2.10 X 1.20
DN
UP
TREAD 30 RISER 15
MID LANDING
LIFT
CAPACITY
STENO 2.53X2.60
JUDGES CHAMBER 3.75 X 3.22
COURT OFFICE 3.75 X 2.93
RECORD 2.60 X5.25
COURT 5.77 X 8.63
DIAS
CORRIDOR 2.10M WIDE
PORCH BELOW
LVL +4.60
WAITING 4.48 X 3.23
WAITING
POLY - CARBONATE SHEET ROOFING
23 THK. BK.PARAPET 90 HIGH
R.C.C.CHAJJA 60 PROJ.
OPEN TO SKY 14.05 X 11.63
WAITING 4.48 X 3.23
WITNESS RM. (L) 4.25 X 4.29
WITNESS RM. (G) 4.25 X 4.06
LADIES TIFFIN RM. 4.25 X 4.29
GENTS TIFFIN RM. 4.25 X 4.06
CORRIDOR 2.40M WIDE
LADIES BAR RM. 5.77 X 1.81
PUBLIC TOILET (L) 5.77 X 2.85
STAFF TOILET (L) 5.77 X 2.85
PUBLIC TOI.(G) 3.22X2.85
DUCT
DRINKING WATER COOLER
W.C.
TOILET 5.77 X 2.85
LVL +4.45
LVL +4.60
CORRIDOR 2.10M WIDE
LIBRARY 11.30 X 5.77
FACILITATION RM. 5.65 X 5.77
LIFT 2.10 X 1.80
CAPACITY 10 P.
FORMS & STATIONARY 3.32X 5.77
GENTS BAR RM. 11.05 X 5.77
MID LANDING
A
B
29.30
3.67
3.59
4.19
2.90
2.90
4.84
3.50
3.47
4.19
3.59
3.67
40.73
PORCH BELOW

FIRST FLOOR PLAN

BUILT UP AREA =1012.64SQ.M.

AUTHORITY-

THIS WORKING DRAWING IS PREPARED ON THE BASIS OF LINE PLANS APPROVED BY THE PRINCIPAL DISTRICT & SESSIONS JUDGE THANE, CONVEYED TO THIS OFFICE BY EX.ENG. SPECIAL PROJECT (P.W.) DIV., THANE. VIDE HIS LETTER NO.VIPRA/VIPRA/SHA/3/2042 DT.28/09/2012

NOTES

- ANY DISCREPANCY NOTICED IN THIS DRAWING SHALL BE BROUGHT TO NOTICED OF THE CHIEF ARCHITECT M.S.P.W.D., MUMBAI BEFORE EXECUTION OF WORK.
- ALL DIMENSIONS ARE IN MTS EXCEPT WHEREVER MENTIONED BY UNITS.
- ONLY WRITTEN DIMENSIONS ARE TO BE FOLLOWED.

NO.	DATE	SIGN	CONTENTS

REVISIONS

OFFICE OF THE
CHIEF ARCHITECT
MAHARASHTRA STATE P.W. D.
MUMBAI.

B.M. SANKHE CA/90/12830
CHIEF ARCHITECT

P. S. BALWANT CA/83/7574
DY.CHIEF ARCHITECT

Mskumbhare
M. S. KUMBHARE CA/94/17559
ARCHITECT

PROPOSED MEERA BHAINDER,
JUDICIAL AND CRIMINAL COURT.
BUILDING AT MAUJE
GHODBANDER TALUKA - THANE
DIST. THANE. (6 COURT HALLS)

WORKING DRG.
FIRST FLOOR PLAN.

1:100	12/10/12	K.J.KARVE
SCALE	DATE	DELT BY
JOB NO.	TNE - 372 / I	
DRG. NO.	2	

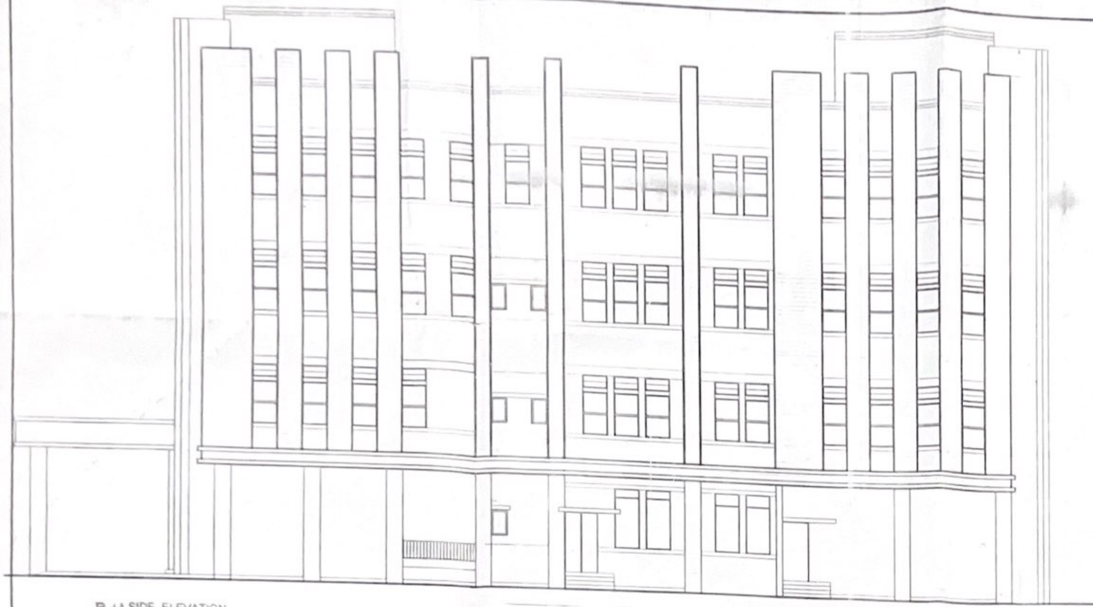

R.H SIDE ELEVATION

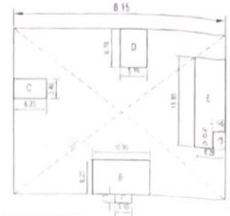

AREA DIAGRAM
STILT FLOOR PLAN
SCALE -1 500

AREA CALCULATION

B - 10.89 X 6.23 = 3.42 SQ M
C - 6.23 X 3.46 = 5.85 SQ M
D - 5.19 X 6.76 = 6.41 SQ M
E - 15.85X 6.29 = 163.40SQ M
F - 3.30X1.50 = 4.95SQ M
TOTAL (B+F) = 184.03 SQ M

DEDUCTIONS

1 2.48 x 3.07 = 7.61SQ M
184.03 - 7.61 = 176.42SQ M
TOTAL (B+F)-1 = 176.42SQ M
TOTAL AREA OF STILT FL = 176.42SQ M

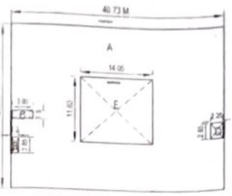

AREA DIAGRAM
TYPICAL (1st TO 3rd) FLOOR PLAN
SCALE -1 500

AREA CALCULATION

A - 40.73 X 29.30 = 1193.39 SQ M

DEDUCTIONS
B - 1.43X 2.85 = 4.08 SQ M
C - 4.13X 1.50 = 6.20 SQ M
D - 2.48X 2.85 = 7.07SQ M
E - 14.05X 11.63 = 163.40SQ M
TOTAL DEDUCTIONS (B+E) = 180.75SQ M
TOTAL = A - (B+E) = 1193.39 - 180.75 = 1012.64 SQ M
TOTAL AREA OF TYPICAL FL (1st+3rd)
1012.64+1012.64+1012.64= 3037.92SQ M
TOTAL AREA OF BUILDING = 3037.92SQ M
STILT + (1st TO 3rd) = 184.03 + 3037.92SQ M = 3214.34SQ M

AUTHORITY-
THIS WORKING DRAWING IS PREPARED [illegible]
LINE PLANS APPROVED BY [illegible]
JUDGE THANE, CONVEYED TO THIS OFFICE BY [illegible]
PROJECT (P.W.) DIV. THANE VIDE [illegible]
NO VIPRAVIPRASHA 3/2002 DT [illegible] 2012

NOTES
- ANY DISCREPANCY NOTICED IN THIS DRAWING SHALL BE BROUGHT TO NOTICED OF THE CHIEF ARCHITECT M.S.P.W.D., MUMBAI BEFORE EXECUTION OF WORK.
- ALL DIMENSIONS ARE IN MTS EXCEPT WHERE [illegible] MENTIONED BY UNITS.
- ONLY WRITTEN DIMENSIONS ARE TO BE FOLLOWED

BRIEF SPECIFICATION		
STRUCTURE		R C C FRAMED STRUCTURE
FOUNDATION		R C C FOUNDATION AS PER SOIL CONDITION
WALLS	a) EXTERNAL	23 CM THK BRICK MASONARY IN CEMENT MORTAR WITHOUT PLASTER
	b) INTERNAL	15 CM THK BRICK MASONARY IN CEMENT MORTAR INCLUDING PLASTER
PLASTER	a) EXTERNAL	SAND FACED CEMENT PLASTER
	b) INTERNAL	CEMENT PLASTER WITH NEERU FINISH
FLOORING	a) ENT STEPS	GRANITE
	b) ENT FOYER CORRIDORS	GRANITE STONE FLOORING WITH MARBLE /GRANITE STRIPE SHED AND QUALITY SHALL BE GOT APPROVED FROM THE CHIEF ARCHIECT
	c) STAIRCASE	MIRROR POLISHED KOTAH STONE FLOORING
	d) GENERAL ROOMS	POLISHED KOTAH STONE
	f) TOILET BLOCK ATTACHED TOILET	GRANITE STONE
	g) JUDGES CHAMBER ANTI RM OFFICE STENO WAITING GENTS&LADIES BAR RM ADM AGP/DGP JUDICIAL ADVOCATE LIBRARY ADR MEMBER SECRETERY	VITRIFIED TILES
SKIRTING		HALF TILE SKIRTING AS PER FLOORING FLUSH TO WALL
DADO	a) KITCHEN	CERAMIC TILES UP TO DOOR HT
	c) TOILET	CERAMIC TILES UP TO DOOR HT
DOORS	a) MAIN ENTRANCE	T W FRAMED PARTLY GLAZED PARTLY PANELLED DOOR AS PER DETAILS
	b) COURT HALL	T W FRAMED DOUBLE SHUTTERED PANELLED DOOR AS PER DETAILS
	c) ANCILLARIES ROOMS	T W FREAME SOLID CORE FLUSH DOOR LAMINATED ON BOTH SIDES SINGLE SHUTTERED DOOR AS PER DETAILS
	d) TOILET	MARBLE/GRANITE FRAME WITH F R P SHUTTERED DOOR

BRIEF SPECIFICATION		
		ALUMINIUM POWDER COATED FRAME, FULLY GLAZED COMPOSITE WINDOWS VENTILATORS AS PER DETAILS SHUTTERS WITH 2/3 TRACK AS PER DETAIL
		ALUMINIUM POWDER COATED FRAME GLAZED VENTILATOR
		AS PER DETAIL
	a) EXTERNAL	70% SYNTHETIC TEXTURED PAINT 30% AGGREATE SYNTHETIC PLASTER APPROVED SHADE SHADE AND QUALITY
	b) INTERNAL WALLS	OIL BOUND DISTEMPER OF APPROVED SHADE AND QUALITY
	c) ALL CEILING	O B D PAINT
WOOD WORK & STEEL WORK		SYNTHETIC ENAMEL PAINT OF APPROVED SHADE AND QUALITY
ROOF		R C C SLAB WITH WATER PROOFING
ELECTRICITY		CONCEALED WIRING WITH P V C CASEMENT
FIXTURES AND FASTENINGS		BRASS FIXTURES WHEREVER NECESSARY
PLUMBING AND SANITATION		ANGLO INDIAN W C PAN AND EUROPEAN PAN WITH LOW LEVEL FLUSHING CISTERN, ORRISA PAN WITH HALF TURN CLOCK, W H B URINALS WITH MARBLE PARTITIONS
S S RAILING AND M S GRILL/ALU GRILL		AS PER DESION DETAIL APPROVED BY CHIEF ARCHITECT
MISCELLANEOUS	a) OVERHEAD WATER STORAGE TANK	R C C OVERHEAD WATER STORAGE TANK OF REQUIRED CAPACITY
	b) PLINTH PROTECTION	100 CM WIDE P C C BEDDING ALL AROUND THE BUILDING AND TERMITE TREATMENT SHALL BE GIVEN TO FOUNDATION AND PLINTH LEVEL AS PER REQUIRMENT
	c) PLATFORMS	GRANITE FINISH
	d) WINDOW	SILL FINISHED IN GRANITE

SCHEDULE OF WINDOWS

1	W	3.24 X 1.50	ANODISED ALLUMINIUM FRAMED FULLY GLAZED FOUR TRACK SLIDING WINDOW AS PER DETAIL
2	W1	1.80 X 1.50	ANODISED ALLUMINIUM FRAMED, FULLY GLAZED THREE TRACK SLIDING WINDOW AS PER DETAIL
2	W2	1.50 X 1.50	ANODISED ALLUMINIUM FRAMED FULLY GLAZED TWO TRACK SLIDING WINDOWS AS PER DETAILS
3	W3	0.90 X 1.50	ANODISED ALLUMINIUM FRAMED FULLY GLAZED SINGLE SHUTTERED OPENABLE WINDOWS AS PER DETAIL
4	W4	60 X 0.90	ANODISED ALLUMINIUM FRAMED,FULLY GLAZED,PARTLY FIXED PARTLY LOUVERED WINDOWS AS PER DETAIL
5	V	3.24 X 0.45	ANODISED ALLUMINIUM FRAMED FIXED GLAZED,COMPOSITE VENTILATOR AS PER DETAIL
7	V1	1.80 X 0.45	ANODISED ALLUMINIUM FRAMED, FIXED GLAZED,COMPOSITE VENTILATOR AS PER DETAIL
8	V2	1.50X 0.45	ANODISED ALLUMINIUM FRAMED, FIXED GLAZED,COMPOSITE VENTILATOR AS PER DETAIL
9	V3	1.20X 0.45	ANODISED ALLUMINIUM FRAMED FIXED GLAZED,COMPOSITE VENTILATOR AS PER DETAIL
10	V4	0.90X 0.45	ANODISED ALLUMINIUM FRAMED, FIXED GLAZED,COMPOSITE VENTILATOR AS PER DETAIL

SCHEDULE OF DOORS

NO	TYPE	SIZE	DESCRIPTION
1	D	3.24X2.70	T W FRAMED SOLID CORE DOUBLE SHUTTER PARTLY FIXED PARTLY OPENABLE WITH FANIGHT AS PER DETAIL
2	D1	1.80 X 2.70	T W FRAMED SOLID CORE DOUBLE SHUTTER WITH FANLIGHT AS PER DETAIL
3	D2	1.20 X 2.10	T W FRAMED SOLID CORE DOUBLE SHUTTER AS PER DETAIL
4	D3	1.00 X 2.10	T W FRAMED SOLID CORE SINGLE SHUTTER FLUSH DOOR AS PER DETAIL
5	D4	1.00X 2.10	GRANITE/ MARBLE WITH P V C SHUTTERS AS PER DETAIL
6	D4A	1.00X 2.10	GRANITE/ MARBLE WITH P V C SHUTTERS AS PER DETAIL FOR HANDICAPPED
7	D5	0.80 X 2.10	GRANITE/ MARBLE WITH P V C SHUTTERS AS PER DETAIL
8	D6	1.00 X 2.10	M S GRILL DOOR AS PER DETAIL

NO	DATE	SIGN	CONTENTS

REVISIONS

OFFICE OF THE
CHIEF ARCHITECT
MAHARASHTRA STATE P.W.D.
MUMBAI.

B.M. SANKHE
CHIEF ARCHITECT

P. S. BALWANT
DY CHIEF ARCHITECT

Mskumbhare
M. S. KUMBHARE
ARCHITECT

PROPOSED MEERA [illegible]
JUDICIAL AND CRIMINAL COURT
BUILDING AT MAUJE,
GHODBANDER TALUKA THANE,
DIST. THANE [illegible]

WORKING DRG.
ELEVATION, AREA DIAGRAM
SPECIFICATIONS, DOOR, WINDOW
SCHEDULE

1:100	12/10/12
SCALE	DATE
JOB NO.	TNE
DRG. NO.	8

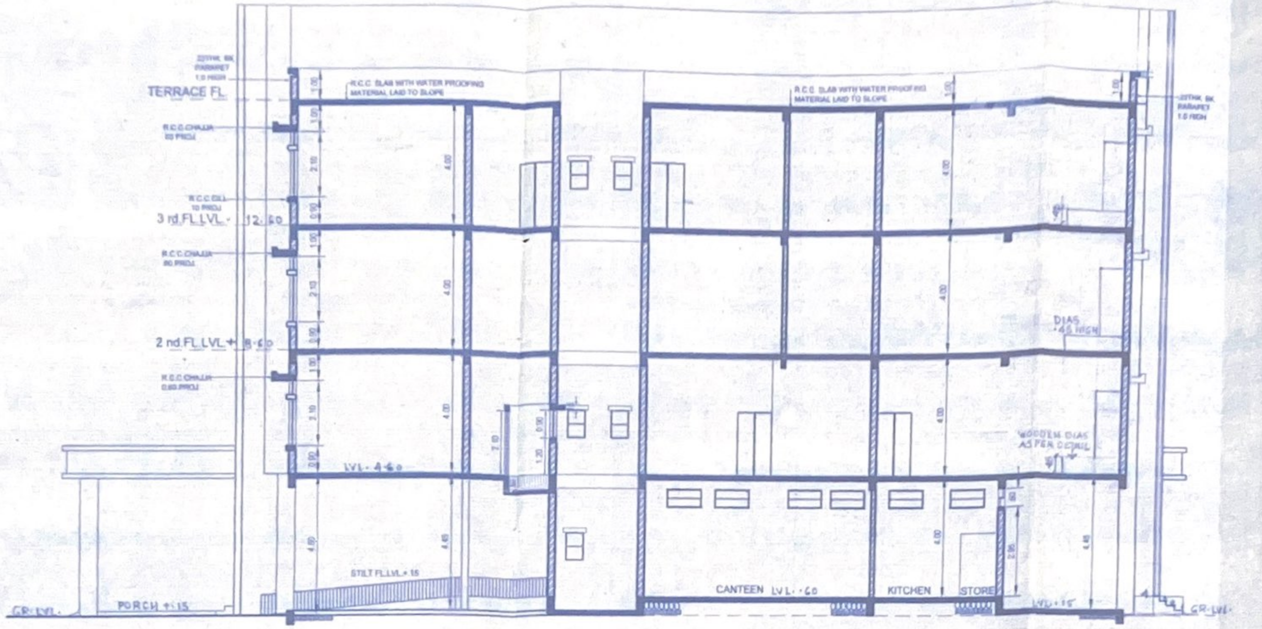
23THK. BK. PARAPET 1.0 HIGH
TERRACE FL.
R.C.C. SLAB WITH WATER PROOFING MATERIAL LAID TO SLOPE
R.C.C.CHAJJA 60 PROJ
R.C.C.SILL 10 PROJ
3 rd.FL.LVL - 12.60
2 nd.FL.LVL + 8.60
R.C.C.CHAJJA 0.60 PROJ
LVL - 4.60
STILT FL.LVL+.15
DIAS .45 HIGH
WOODEN DIAS AS PER DETAIL
CANTEEN LVL - .60
KITCHEN
STORE
LVL - .15
GR. LVL.
PORCH + .15
4.00
4.45
2.10
0.90
1.00

SECTION B-B

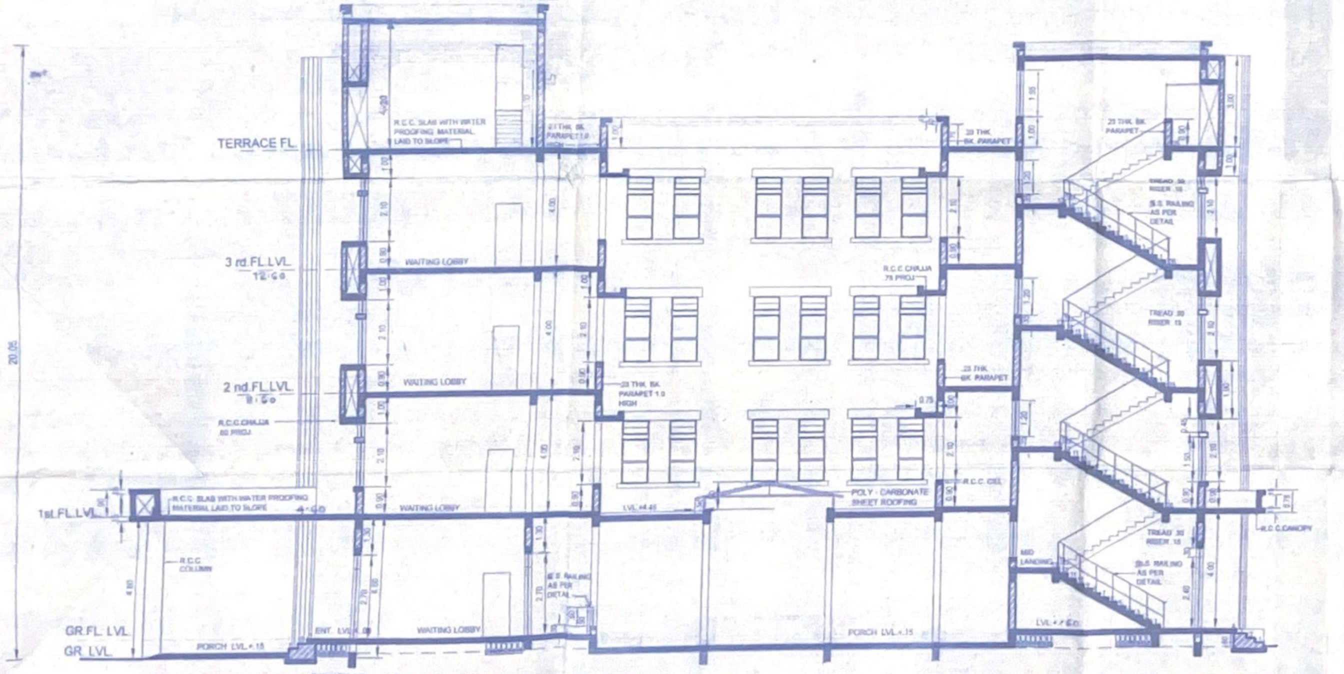
20.05
TERRACE FL.
3 rd.FL.LVL. 12.60
2 nd.FL.LVL. 8.60
1st.FL.LVL. 4.60
GR.FL. LVL.
GR. LVL.
R.C.C. SLAB WITH WATER PROOFING MATERIAL LAID TO SLOPE
23 THK. BK. PARAPET 1.0
R.C.C.CHAJJA 60 PROJ
R.C.C. COLUMN
WAITING LOBBY
ENT. LVL. +.60
PORCH LVL.+.15
M.S. RAILING AS PER DETAIL
23 THK. BK. PARAPET 1.0 HIGH
R.C.C.CHAJJA 75 PROJ
POLY - CARBONATE SHEET ROOFING
R.C.C. CILL
LVL.+4.45
23 THK. BK. PARAPET
TREAD 30 RISER 15
S.S. RAILING AS PER DETAIL
MID LANDING
LVL. + .60
R.C.C.CANOPY
4.00
2.10
0.90
1.00
1.20
1.50
2.40
2.70
3.00

SECTION A- A

AUTHORITY.
THIS WORKING DRAWING IS PREPARED ON THE BASIS OF,
LINE PLANS APPROVED BY THE PRINCIPAL DISTRICT & SESSIONS
JUDGE THANE, CONVEYED TO THIS OFFICE BY EX. ENG. SPECIAL
PROJECT (P.W.) DIV., THANE, VIDE HIS LETTER
NO VIPRA/VIPRASHA-3/2052 DT 28/06/2012

NOTES
-ANY DISCREPANCY NOTICED IN THIS DRAWING SHALL BE BROUGHT TO NOTICED OF THE CHIEF ARCHITECT, M.S.P.W.D., MUMBAI BEFORE EXECUTION OF WORK.
-ALL DIMENSIONS ARE IN MTS EXCEPT WHEREVER MENTIONED BY UNITS.
-ONLY WRITTEN DIMENSIONS ARE TO BE FOLLOWED

NO.	DATE	SIGN	CONTENTS

REVISIONS

OFFICE OF THE
CHIEF ARCHITECT
MAHARASHTRA STATE P.W.D.
MUMBAI.

B.M. SANKHE CA/90/12830
CHIEF ARCHITECT

P. S. Baliwant

P. S. BALIWANT CA/83/7574
DY CHIEF ARCHITECT

Mskumbhare

M. S. KUMBHARE CA/94/17559
ARCHITECT

PROPOSED MEERA BHAINDER,
JUDICIAL AND CRIMINAL COURT,
BUILDING AT MAUJE,
GHODBANDER TALUKA - THANE,
DIST. THANE. (6 COURT HALLS)

WORKING DRG.
SECTIONS .

1:100	12/10/12	M.S. KUMBHARE K.J.KARVE
SCALE	DATE	DELT BY

JOB NO. TNE - 372 / I
DRG. NO. 7