

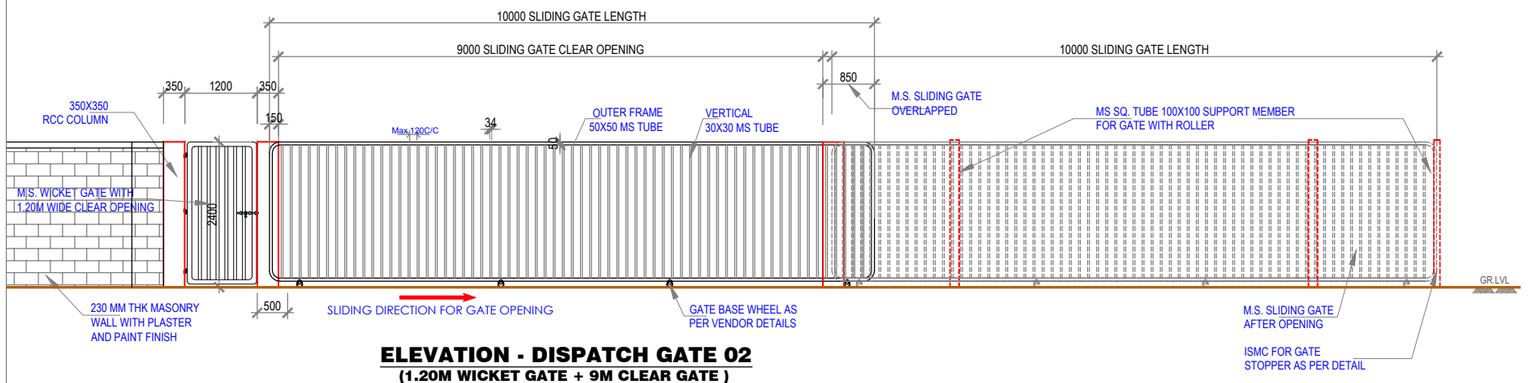


ELEVATION - DISPATCH GATE 02

(1.20M WICKET GATE + 9M CLEAR GATE)

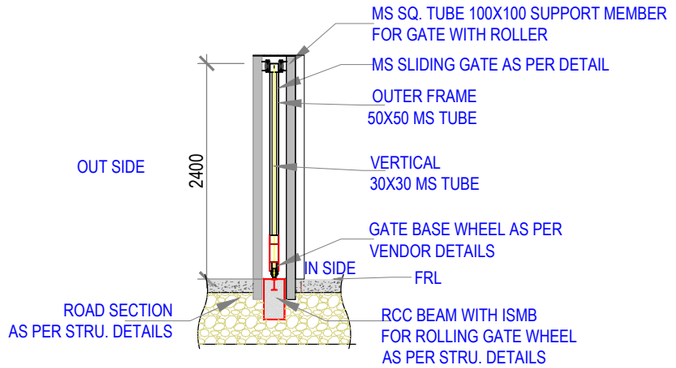

TYP. SECTION

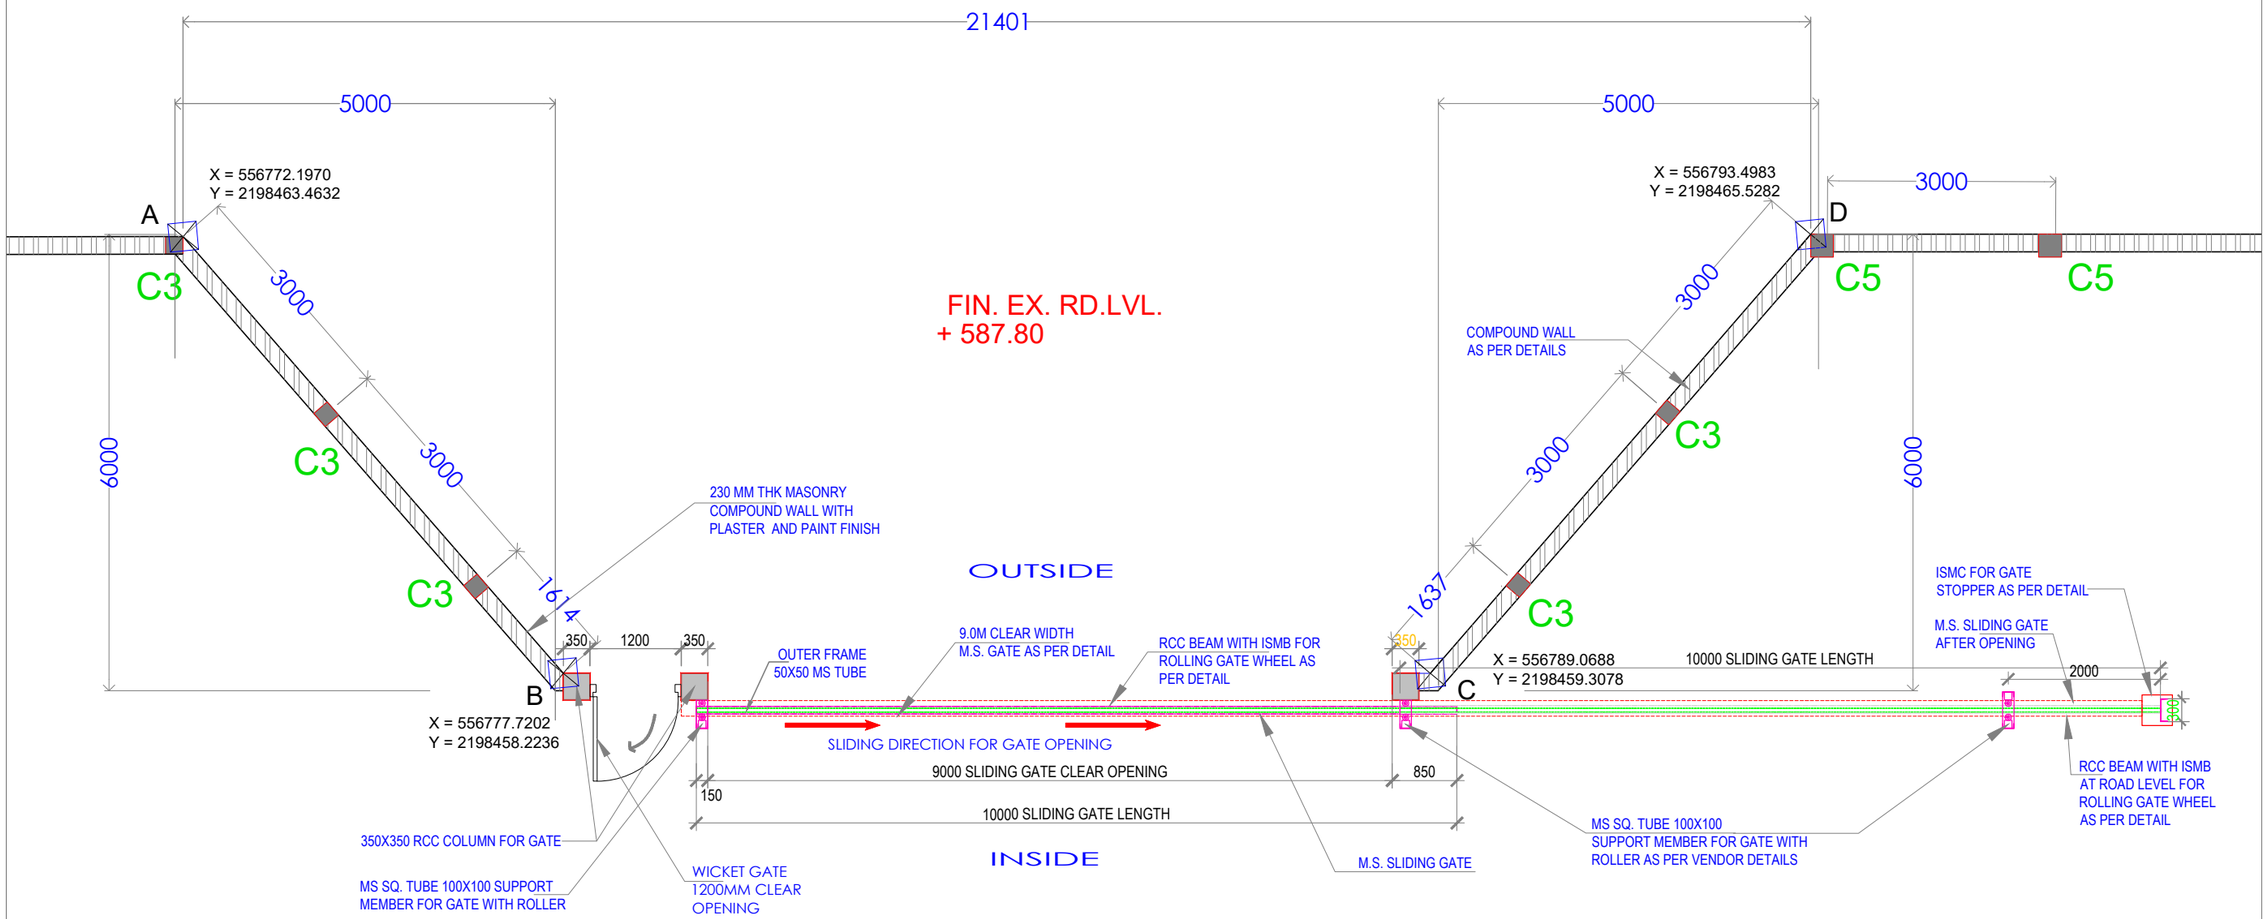

PLAN DISPATCH GATE 02

(1.20M WICKET GATE + 9M CLEAR GATE)

ACAD# KOHL_PCPL_ARCH_GFC_DISP.GATE2_R0