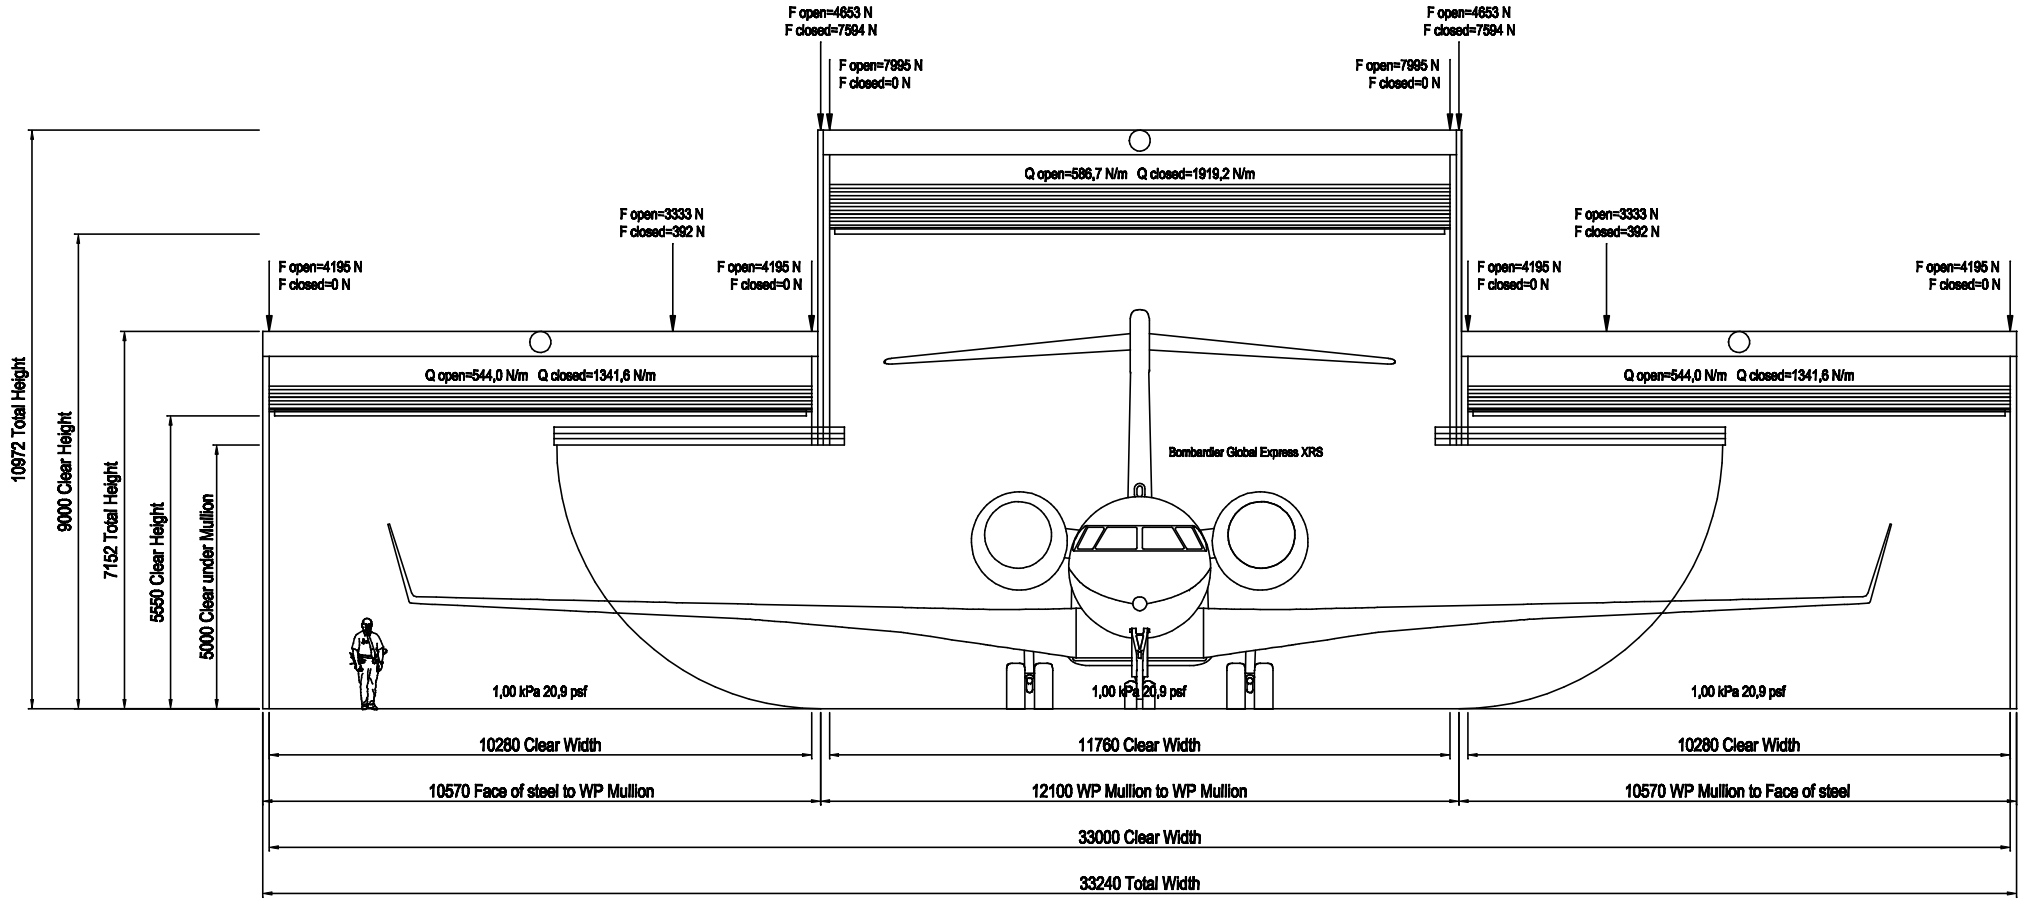



**Contact Information**

Ashish Nair
Sales Manager - Middle East
MEGADOOR/
ASSA ABLOY Entrance Systems
P.O. Box 80983
Dubai, United Arab Amirates
Visiting address: Dubai Investment Park 1
Phone: +971 (0)4 88 52888
Mobile: +971 (0)50 632 04 95
E-mail: ashish.achuthan@assaabloy.com
www.assaabloyentrance.ae

Quotation only. Do not use for design.
Nominal static vertical loads are indicated.
A dynamic surload factor of 1.25 should be added to door leaf loads in open position.
Includes items provided by ASSA ABLOY Entrance Systems only.
Total weight: 6956 kg
Total static weight: 6848 kg
Total motor power: 10,4 kW
Total rated current: 23,3 A
Total peak current: 75,3 A
Power supply: 400V/50Hz/3ph
(max. allowed voltage drop at start: 5%)
Control system: 24V
Mains power to control panel supplied by others than ASSA ABLOY Entrance Systems.

ASSA ABLOY

| | |
|---|---|
| SALES REP. Ashish Nair | DATE ISSUED 2020-05-15 |
| SALES No. | DATE DRAWN 2020-05-15 |
| SCALE N.T.S. | |
| DRAWING No. | REVISION |

Raymond
Mumbai
India

Load diagram