



DWG.NO: SALT_1729_STR_05_R0

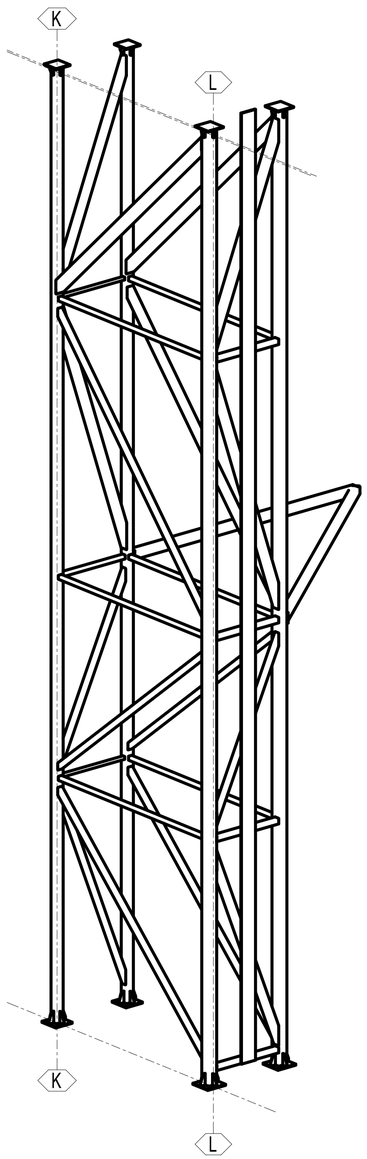


ISOMETRIC VIEW
1:50

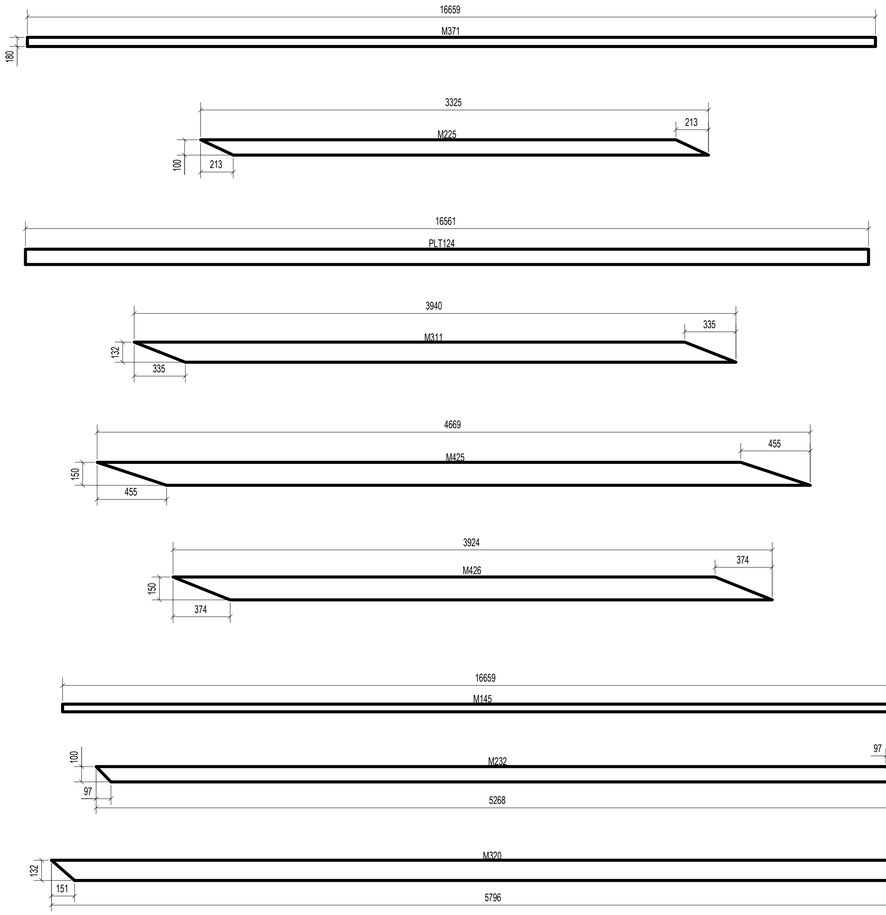


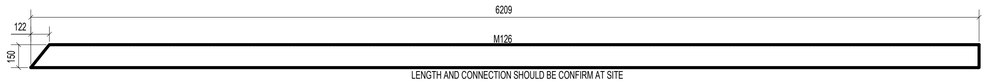

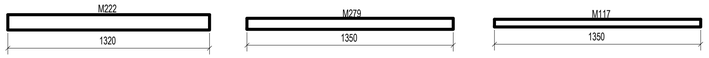

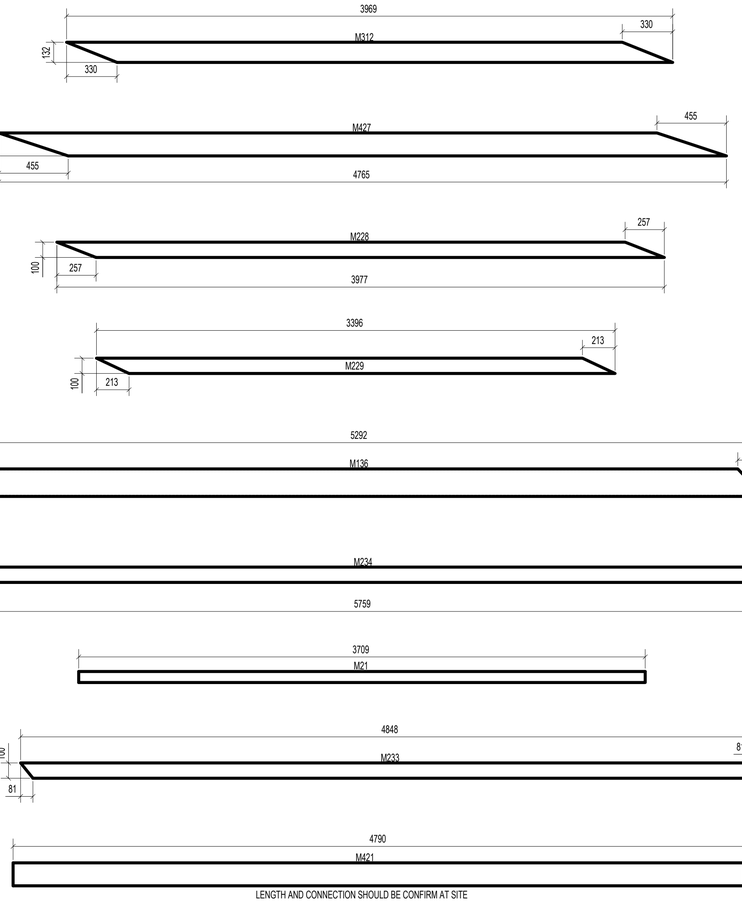

LENGTH AND CONNECTION SHOULD BE CONFIRM AT SITE

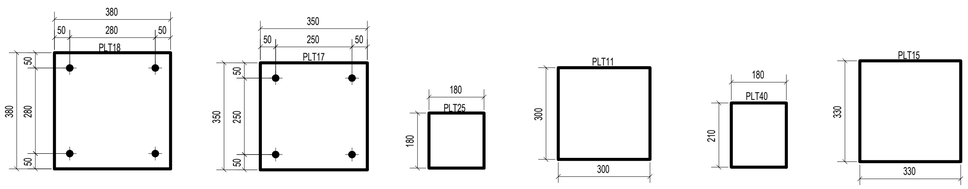

CUTTING DETAIL BETWEEN GRID K & GRID L						
PartPos	Profile	No.	Material	Length	Net Weight(kg	Gross Weight(kg
M21	SHS72.0X72.0X3.2	6	IS2062	3709	24.86	149.16
M117	SHS50*3.6	2	IS2062	1350	7.08	14.16
M126	SHS150*8	1	IS2062	6209	219.31	219.31
M136	SHS180.0X180.0X8.0	2	IS2062	5292	217.34	434.68
M145	SHS150*8	2	IS2062	16659	594.23	1188.46
M222	SHS100.0X100.0X6.0	4	IS2062	1320	22.41	89.64
M225	SHS100.0X100.0X6.0	1	IS2062	3325	52.68	52.68
M228	SHS100.0X100.0X6.0	1	IS2062	3977	62.98	62.98
M229	SHS100.0X100.0X6.0	1	IS2062	3396	53.88	53.88
M232	SHS100.0X100.0X6.0	2	IS2062	5268	87.73	175.46
M233	SHS100.0X100.0X6.0	2	IS2062	4848	80.89	161.78
M234	SHS100.0X100.0X6.0	1	IS2062	5759	95.75	95.75
M279	SHS72*5	1	IS2062	1350	14.2	14.2
M311	SHS132.0X132.0X4.8	1	IS2062	3940	67.28	67.28
M312	SHS132.0X132.0X4.8	1	IS2062	3969	67.91	67.91
M320	SHS132.0X132.0X4.8	1	IS2062	5796	105.51	105.51
M371	SHS180.0X180.0X8.0	2	IS2062	16659	707.48	1414.96
M421	SHS150.0X150.0X5.0	1	IS2062	4790	106.64	106.64
M425	SHS150.0X150.0X5.0	1	IS2062	4669	93.59	93.59
M426	SHS150.0X150.0X5.0	1	IS2062	3924	78.83	78.83
M427	SHS150.0X150.0X5.0	1	IS2062	4765	95.72	95.72
PLT11	PL16*300	2	IS2062	300	11.3	22.6
PLT15	PL16*330	2	IS2062	330	13.68	27.36
PLT17	PL20*350	2	IS2062	350	19.23	38.46
PLT18	PL20*380	2	IS2062	380	22.67	45.34
PLT25	PL10*180	1	IS2062	180	2.54	2.54
PLT40	PL10*180	1	IS2062	210	2.97	2.97
PLT121	PL10*100	16	IS2062	200	1.21	19.36
PLT122	PL10*75	16	IS2062	150	0.66	10.56
PLT124	PLT16*300	1	IS2062	16561	624.02	624.02
	TOTAL					5535.79

NOTES :–

1. ALL DIMENSIONS ARE IN MM & LEVEL ARE IN METER.
2. ALL STRUCTURAL STEEL AS PER IS:2062.
3. PROVIDE WELDING AS PER IS:816.
4. PROVIDE MIN. 6MM WELD WITH MIN. WELD LENGTH OF 150MM.
5. USE ELECTRODS AS PER IS:814 (PT.–I).
6. FILLET/ BUTT WELD SHALL BE OF 6MM SIZE AND SHALL BE CONTINUOUS.
7. FABRICATION AND ERECTION SHALL BE AS PER IS:800 AND IS:803.
8. WELD SHALL BE GROUND SMOOTH.
9. ALL GUSSET PLATES SHALL BE MIN. 10 THK.
10. ALL M.S. BLACK BOLTS AND NUTS SHALL CONFORM TO IS:1363(PT. 1 TO 3).
11. STRUCTURE SHALL BE APPLIED WITH ONE COAT OF RED OXIDE ZINC CROMATE PRIMER AFTER FABRICATION FOLLOWED ONE MORE COAT BEFORE ERECTION. FINALLY APPLY 2 COATS OF SYNTHETIC ENAMAL OF APPROVED QUALITY.

REV.NO.	DESCRIPTION.	REV.DATE	DRAWN.	CHKD.	APPD.
0	DRAWING FOR APPROVAL	27.12.22	AAK	HAB	HAB

DWG.TITLE :- CUTTING DETAIL BETWEEN GRID K & L
DRAWING FOR DOOR FRAME

PROJECT: MEGADOOR INSTALLATION AT HYDRABAD AIRPORT

CLIENT: GMR

SALT Design Services
NIHVA NIHVA TECHNOLOGIES PVT.LTD.

SALT DESIGN SERVICES

NIHVA TECHNOLOGIES PVT. LTD. PUNE
Tel : 020 66304033
Email:- info@nihva.com
Website:- www.nihva.com

DRAWN :AAK	CHECKED : HAB	SCALE: 1:100
APPROVED : HAB	JOB CODE. : 1729	DATE: 27.12.2022

DWG.NO: SALT_1729_STR_05_R0 (SH-1OF1) REV. - R0 SIZE. - A0

A1 [841 x 594]